
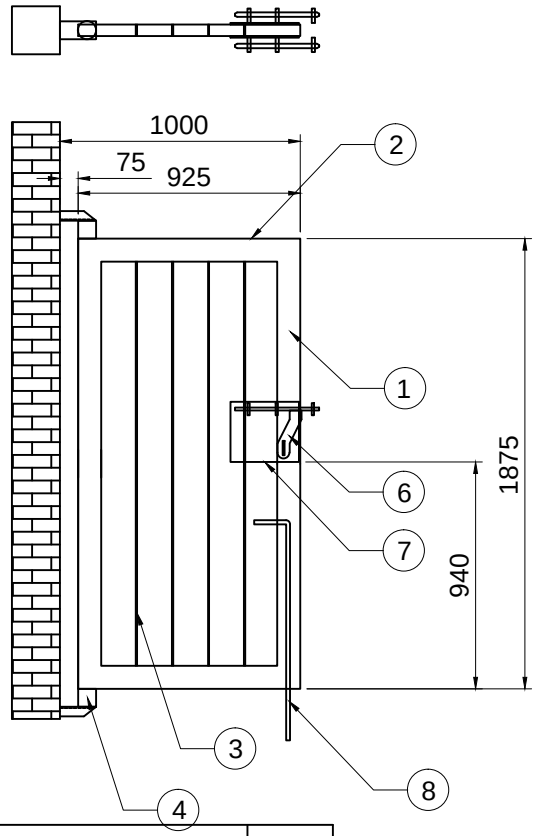


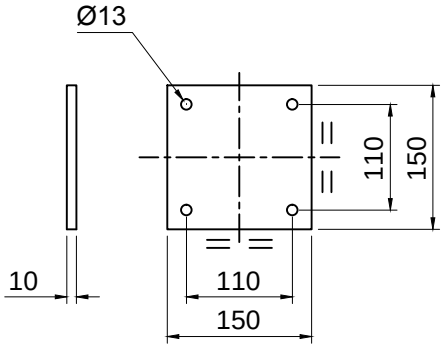

SR NO	DESCRIPTION	SPECIFICATION	QTY
8	M.S BAR	DIA 16 X 1000L	1 NO
7	FLAT	150 X 10 X 150L	2 NOS
6	TOWER BOLT	SET	2 NOS
5	HINGE BRG	STD 3 INCH	2 NOS
4	HINGE BRG	STD 3 INCH	2 NOS
3	FLAT	50 X 5 THK X 1680L	4 NOS
2	R.TUBE	96 x 48 x 4.8 THK X 925L	2 NOS
1	R.TUBE	96 x 48 x 4.8 THK X 1875L	2 NOS

TOLERANCE - ±2mm

This drawing & design is the property of NIHVA TECHNOLOGIES. Not to be sold or copied to any other concern.

TITLE: WICKET GATE

	NAME	SIGN	DATE
DRAWN	P.V.A		18.11.2019
CHECK	G.J		18.11.2019
APPRD.			

If any queries contact : design@nihva.com

ALL DIMENSION ARE IN mm

NIHVA TECHNOLOGIES PVT. LTD. PUNE
Tel : 020 66304033
Email:- info@nihva.com
Website:- www.nihva.com

CLIENT -

PROJECT -

SITE LOCATION -

DWG. NO. : NIHVA/19-20/VDR/225 | REV- 0

SCALE: NTS | WT: | SHEET: 01 OF 01