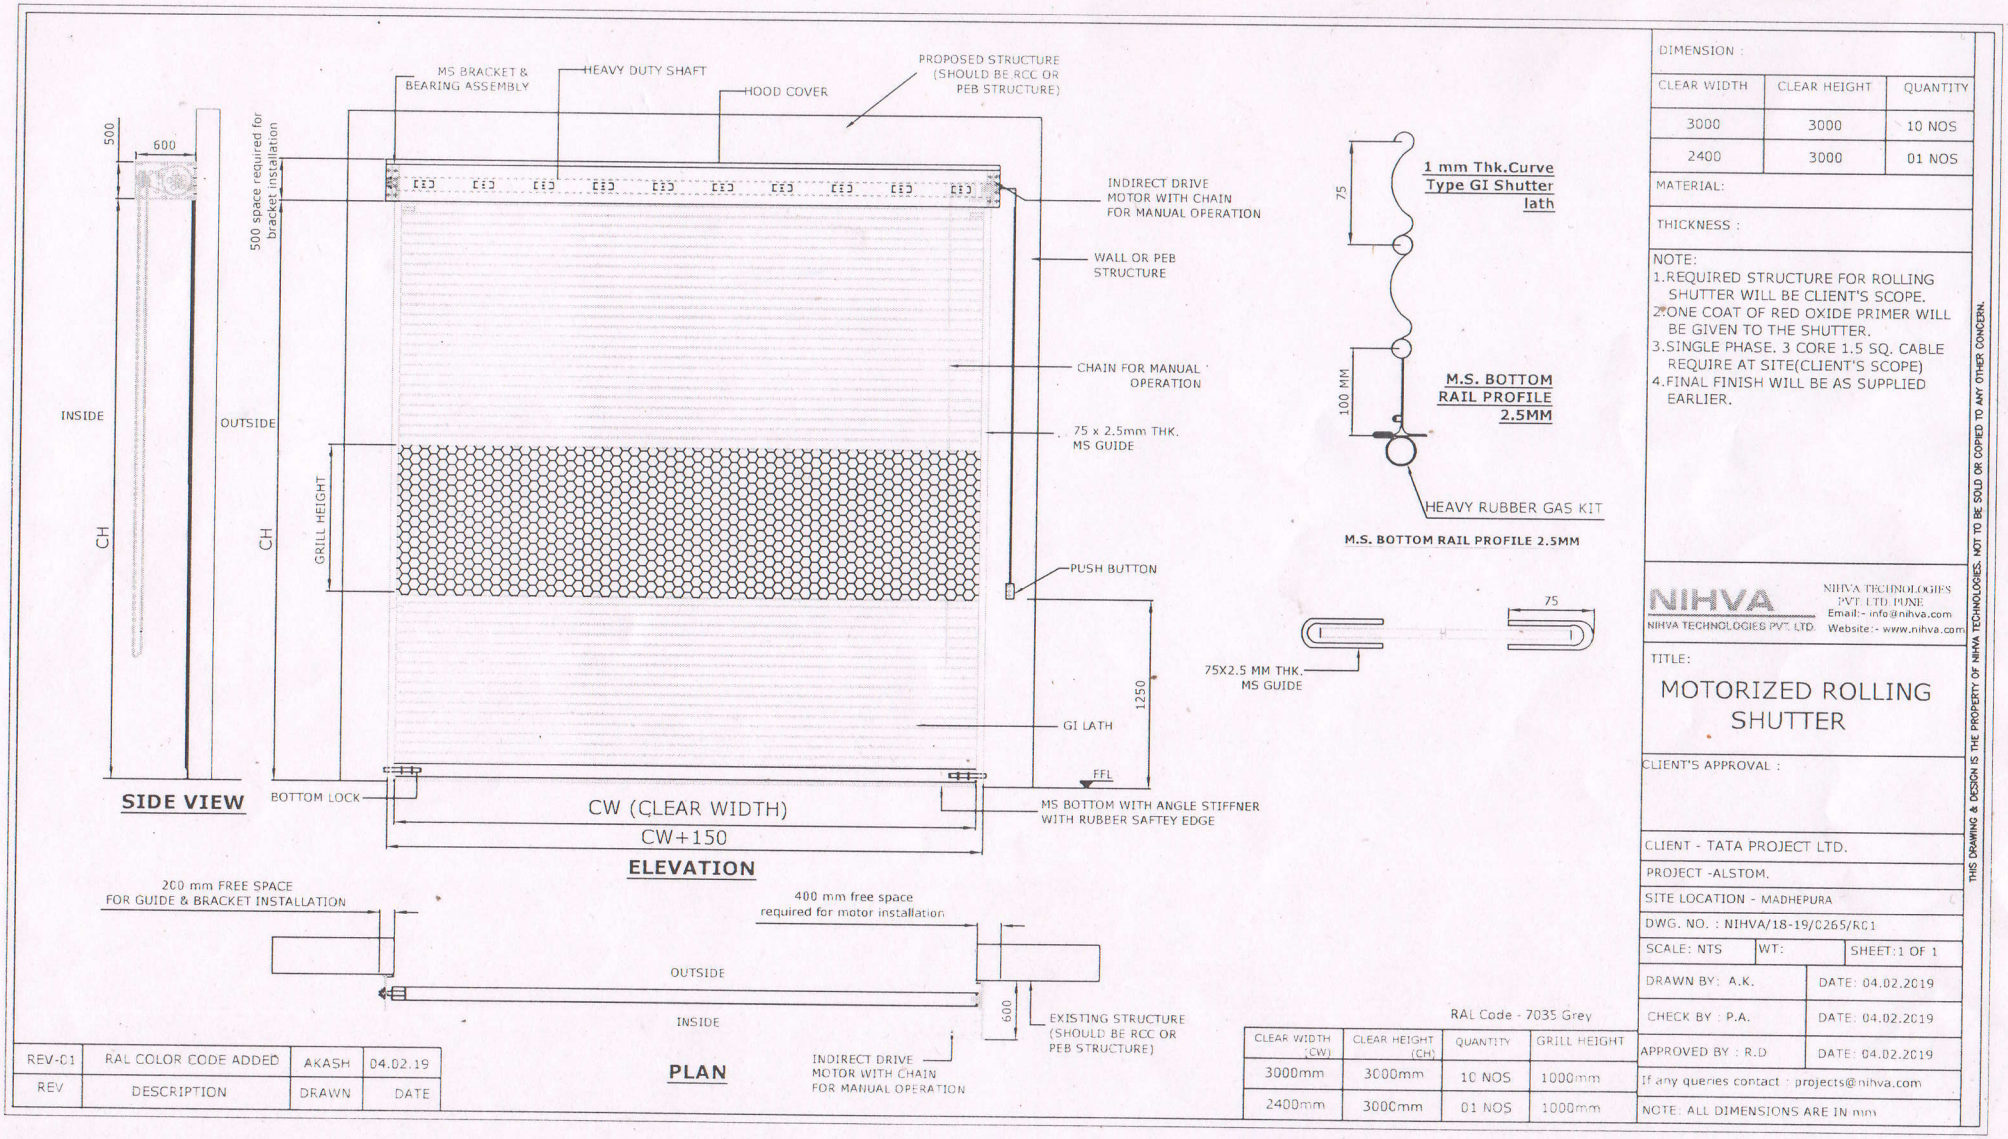


REV	DESCRIPTION	DRAWN	DATE
REV-01	RAL COLOR CODE ADDED	AKASH	04.02.19

RAL Code - 7035 Grey

CLEAR WIDTH (CW)	CLEAR HEIGHT (CH)	QUANTITY	GRILL HEIGHT
3000mm	3000mm	10 NOS	1000mm
2400mm	3000mm	01 NOS	1000mm

DIMENSION :

CLEAR WIDTH	CLEAR HEIGHT	QUANTITY
3000	3000	10 NOS
2400	3000	01 NOS

MATERIAL:

THICKNESS :

NOTE:
1. REQUIRED STRUCTURE FOR ROLLING SHUTTER WILL BE CLIENT'S SCOPE.
2. ONE COAT OF RED OXIDE PRIMER WILL BE GIVEN TO THE SHUTTER.
3. SINGLE PHASE. 3 CORE 1.5 SQ. CABLE REQUIRE AT SITE(CLIENT'S SCOPE)
4. FINAL FINISH WILL BE AS SUPPLIED EARLIER.

NIHVA TECHNOLOGIES PVT. LTD.
NIHVA TECHNOLOGIES PVT. LTD. PUNE
Email:- info@nihva.com
Website:- www.nihva.com

TITLE:
MOTORIZED ROLLING SHUTTER

CLIENT'S APPROVAL :

CLIENT - TATA PROJECT LTD.

PROJECT -ALSTOM.

SITE LOCATION - MADHEPURA

DWG. NO. : NIHVA/18-19/C265/RC1

SCALE: NTS	WT:	SHEET:1 OF 1
DRAWN BY: A.K.		DATE: 04.02.2019
CHECK BY : P.A.		DATE: 04.02.2019
APPROVED BY : R.D		DATE: 04.02.2019

If any queries contact : projects@nihva.com

NOTE: ALL DIMENSIONS ARE IN mm

THIS DRAWING & DESIGN IS THE PROPERTY OF NIHVA TECHNOLOGIES. NOT TO BE SOLD OR COPIED TO ANY OTHER CONCERN.

Note:- Rolling Shutter will be Fix in Shop. So grill Not Required for Rolling Shutter
So Flate plates only fix in Entire Length.

TATA PROJECTS LTD. GFC