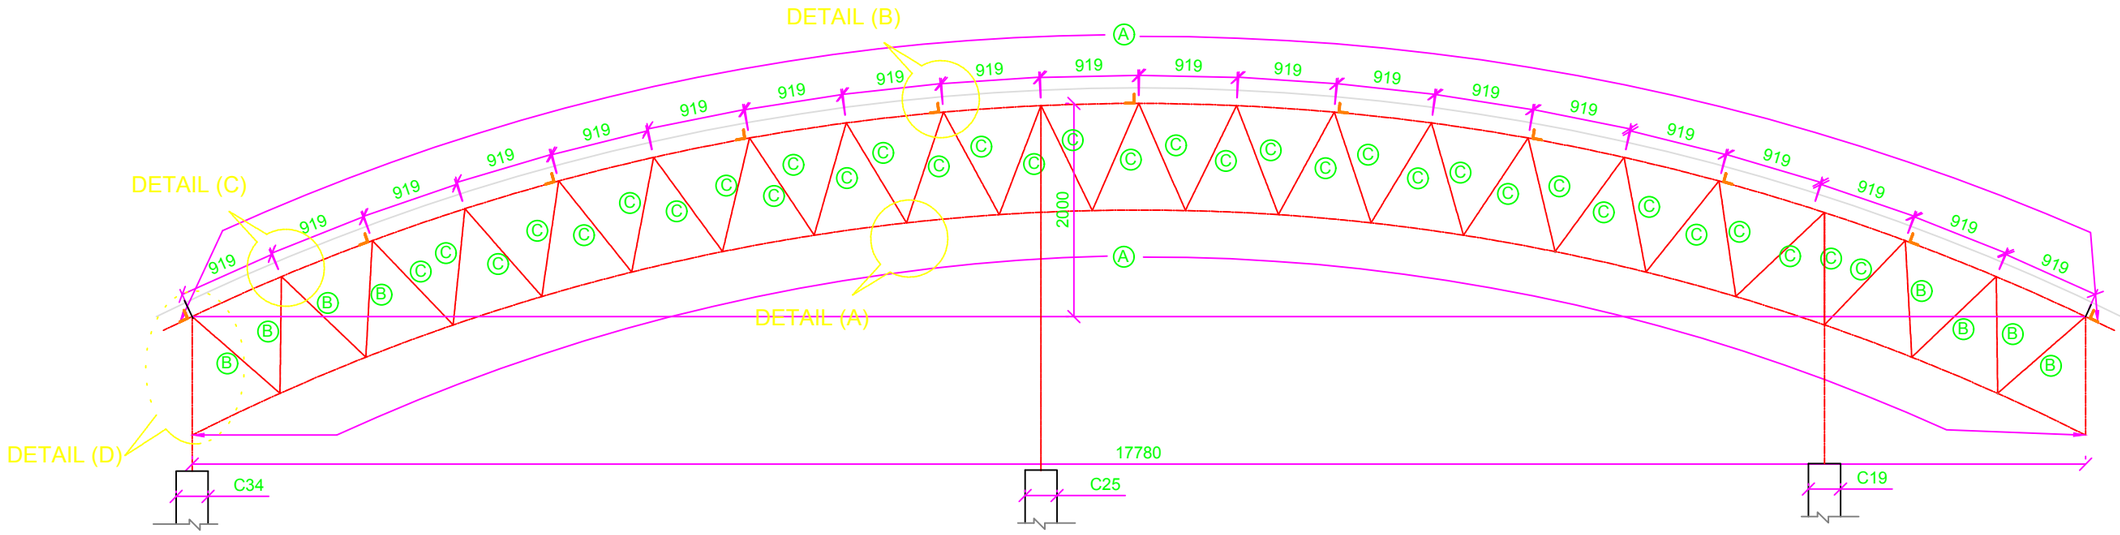


TRUSS-T2 ELEVATION

R5	DESIGN		DATE		
R4	DESIGN		DATE		
R3	DESIGN		DATE		
R2	DESIGN		DATE		
R1	DESIGN		DATE		
R0	DESIGN	ORIGINAL ISSUE	DATE	00/00/2023	
	___		DRAWN BY	___	
REV NO		REVISION DETAILS			

DRAWING	TRUSS ELEVATION		
PROJECT	PROP. CONSTRUCTION OF SCHOOL BLDG AT VIMANNAGAR PUNE FOR SYMBIOSIS.		
ARCHITECT	PANASE ASSOCIATE		
CLIENT	SYMBIOSIS.		

SATISH MARATHE
CONSULTING ENGINEERS
GHAGARE RESIDENCY, 105A/30, INCOME TAX LANE, PUNE - 411 004.
WEB: satishmarathe.com EMAIL : smce.civil@gmail.com
Ph. (020) - 25441396, 25445477, 29910754.

DESIGNED BY	ANGADI	DATE	AUG-2023
DRAWN BY	SAWANT	SHEET NO	**S1-B**
CHECKED BY	____	JOB NO	4573
SCALE	NTS		

NOT FOR CONSTRUCTION