



DETAIL A

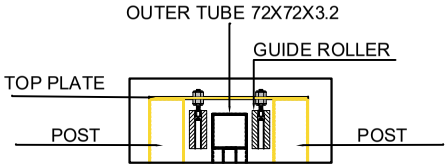

DETAIL B

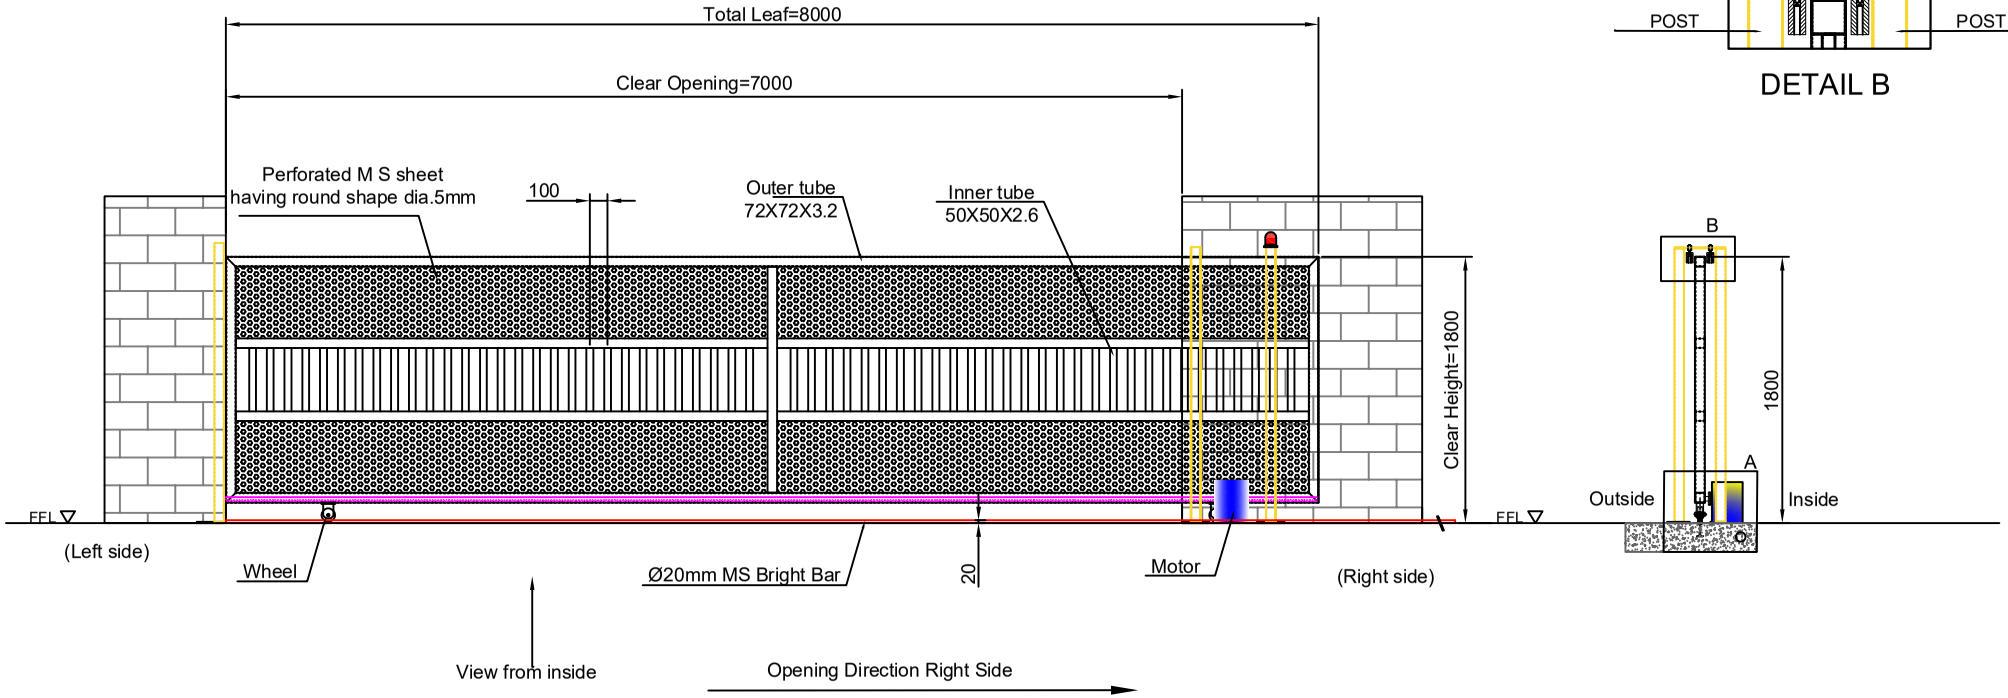

Note:--

1. Given above Sliding Gate drawing(GA) only for the client understanding purpose.
2. Required all Civil work will be in client scope
3. All Dimensions are in mm
4. Required Parking Space will be 8100mm
5. Power supply required near by Motor and Under ground 3"PVC pipe required from motor to start opening point for photocell cabling

Rev No.	Revision	Date	Revised By

This drawing & design is the property of NIHVA TECHNOLOGIES. Not to be sold or copied to any other concern.

TITLE:- MS Motorised Single Leaf Sliding Gate

NIHVA TECHNOLOGIES PVT. LTD.

NIHVA TECHNOLOGIES PVT. LTD. PUNE
Tel : 020 66304033
Email:- info@nihva.com
Website:- www.nihva.com

	NAME	DATE	SIGN
DRAWN	SUJATA	24/02/2022	
CHECK	G.PATIL	24/02/2022	
APPRD.	P.J	24/02/2022	

If any queries contact : design@nihva.com

ALL DIMENSION ARE IN mm

CLIENT - INDUS ENGINEES

LOCATION - TALOJA

PRODUCT - SLIDING GATE QTY:-

DWG NO:-NIHVA/21-22/CLT/0324 REV-3

SCALE: NTS SCALE:-- 1:1 SHEET: 01 OF 01