

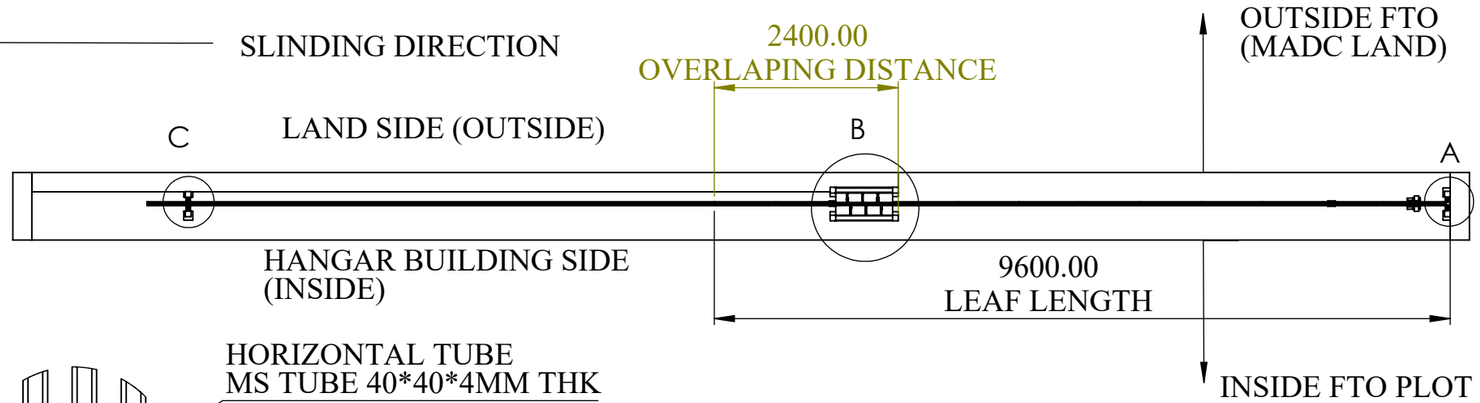


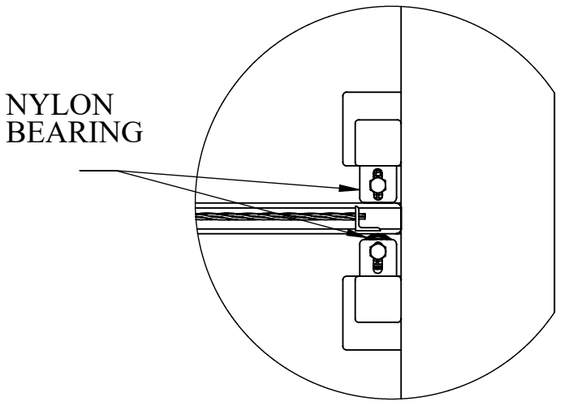



POST 1 AND NYLON
BEARING ASM

DETAIL A
SCALE 1 : 10

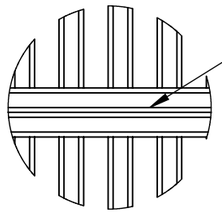


DETAIL E
SCALE 1 : 10

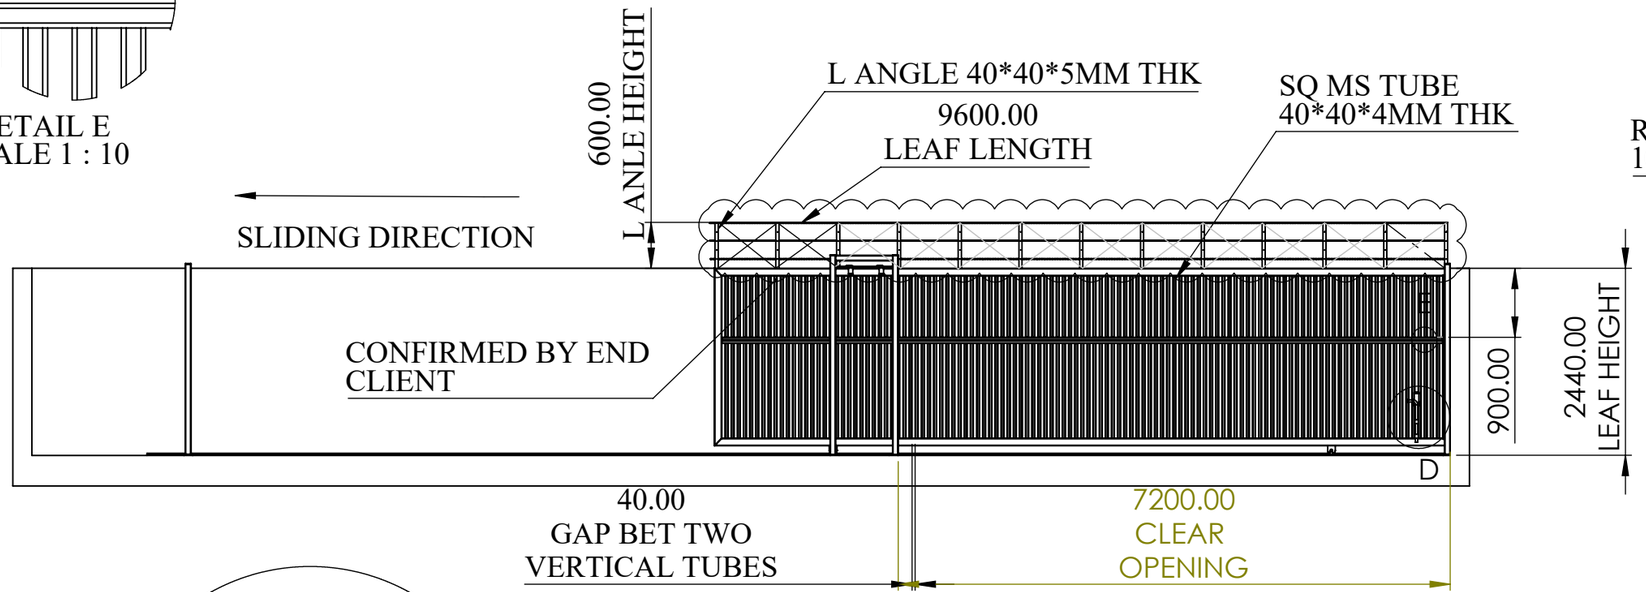

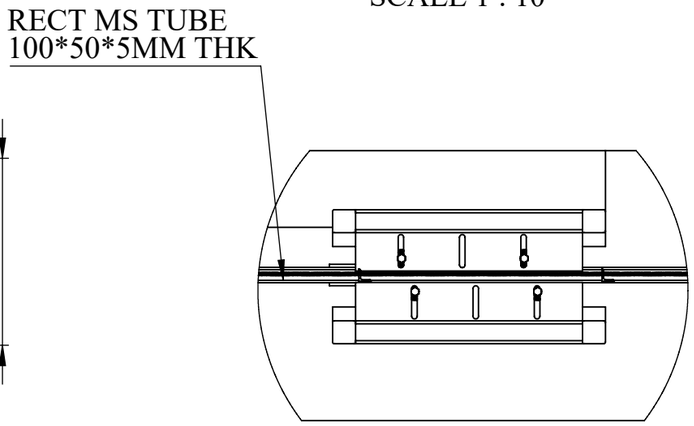


POST 2 AND NYLON
BEARING ASM

DETAIL B
SCALE 1 : 20

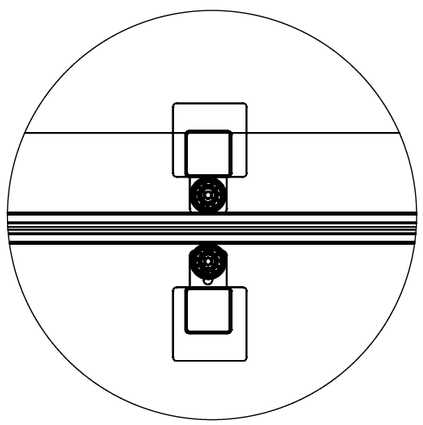

POST NO 3 &
NYLON ROLLER BERAING
ASM

DETAIL C
SCALE 1 : 10

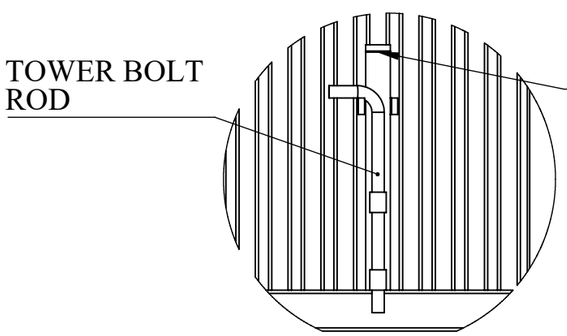

TOWER BOLT LOCKING
ARRANGEMENT.

DETAIL D
SCALE 1 : 15

NOTE :

1)GA DRAWING TYPE NO 01

2)03 column posts when the gates is in the closed position.

3)03 column posts when the gates is in the fully open position.

4) barbed wire design is zigzag pattern.

TITLE - GATE AUTOMATIOM				NIHVA TECHNOLOGIES PVT.LTD.PUNE
DWG NO - NTPL-000-PM-001-00-00-00				Website - www.nihva.com
	NAME	SIGNATURE	DATE	PROJECT NO - NTPL-000-PM
DRAWN	V.W		21-05-2025	PRODUCT - SINGLE SLIDING GATE
CHK'D	S.W.		21-05-2025	SITE LOCATION -
APPV'D	V.T.		21-05-2025	
if any queries contact - supportautomation@nihva.com				REVISION - 01 / QTY - 1
ALL DIMENSION ARE IN mm		A3		SCALE / SHEET 1 OF 1