


Abbrevation's:
WOW-Wall Opening Width
WOH-Wall Opening Height
CH- Clear Height
UC-Under Cut
FFL-Finished Floor Level

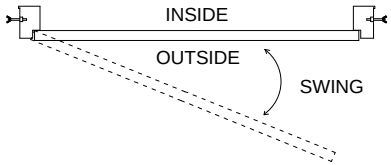


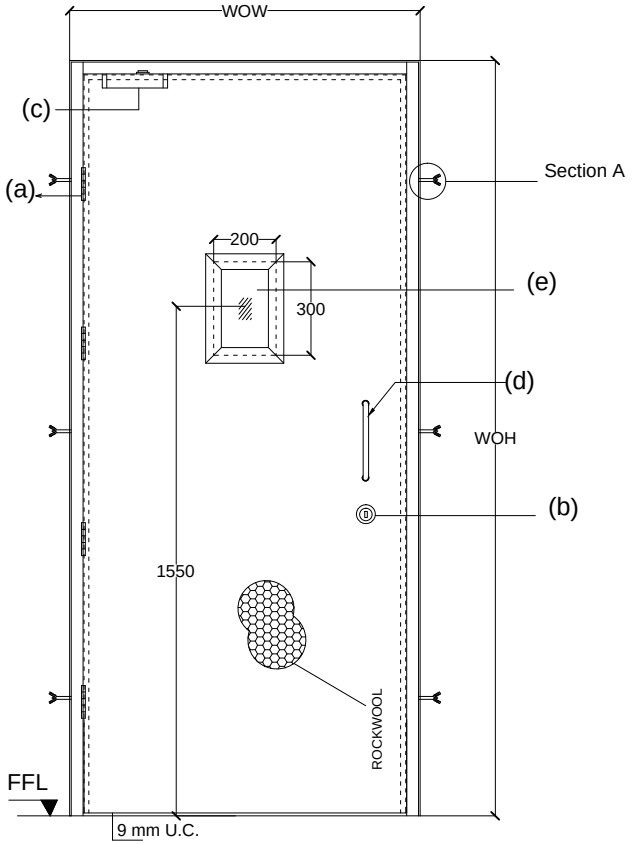

OUTSIDE ELEVATION

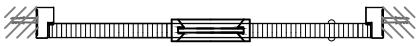

TOP VIEW

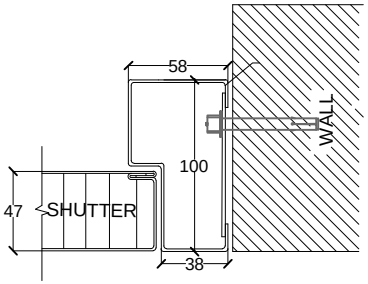

Detail view of Section A

ASSESORIES DETALES

(a) HINGES: SS hinges 100x75x3mm

(b) LOCK : Mortise dead Lock with cylinder(One side key & thumb turn on other side)with escutcheon.

(c) DOOR CLOSER : B4W

(d) HANDLE : D Handle (300x22) pair.

(e) VISION PANEL - 5mm THK. GLASS OF SIZE-200X300mm

Shutter thickness : 47 mm
Frame Sheet thick : 1.20mm
Shutter sheet thick : 0.80mm
Fixing : On Soliid Brick plasterd wall with Anchors

NOTE:- *All Dimensions are in mm.
*Tolerance:-All Linear Dimensions ±3mm,Others ±0.5mm.
*The Drawing Is For Location of Hardware only. Drawing Does Not Represent The Hardware For More Clarity, Please Go Through Hardware Broucher.

COLORS
TRAFFIC WHITE:- RAL9016

NOTE:-
1.Client has to select door handling type from attached door handling sheet.
2.Client should also select color for door from given options.

Door Type

WOW	WOH	TYPE 1	TYPE 2	TYPE 3	TYPE 4	QUANTITY
1200	2100			02		02
1000	2100			04	02	06

This drawing & designing is the property of NIHVA TECHNOLOGIES. Not to be sold or copied to any other concern.

TITLE
STEEL DOOR

NIHVA TECHNOLOGIES PVT. LTD.
NIHVA TECHNOLOGIES PVT. LTD. PUNE
Tel : 020 66304033
Email:- info@nihva.com
Website:- www.nihva.com

	NAME	DATE	SIGN
DRAWN	SURAJ	07/09/17	
CHECK	SHEKHAR	07/09/17	
APPRD.	SHEKHAR	07/09/17	
REV.	01		
MFG			

CLIENT - PHENIX CONSTRUCTION TECHNOLOGIES
PROJECT - SANAND GIDC
SITE LOCATION -GUJARAT
DWG. NO. : NIHVA/17-18/0160/R01 REV- 1
SCALE: NTS WT: SHEET: 01 OF 01
ALL DIMENSION ARE IN mm
If any queries contact : projects@nihva.com