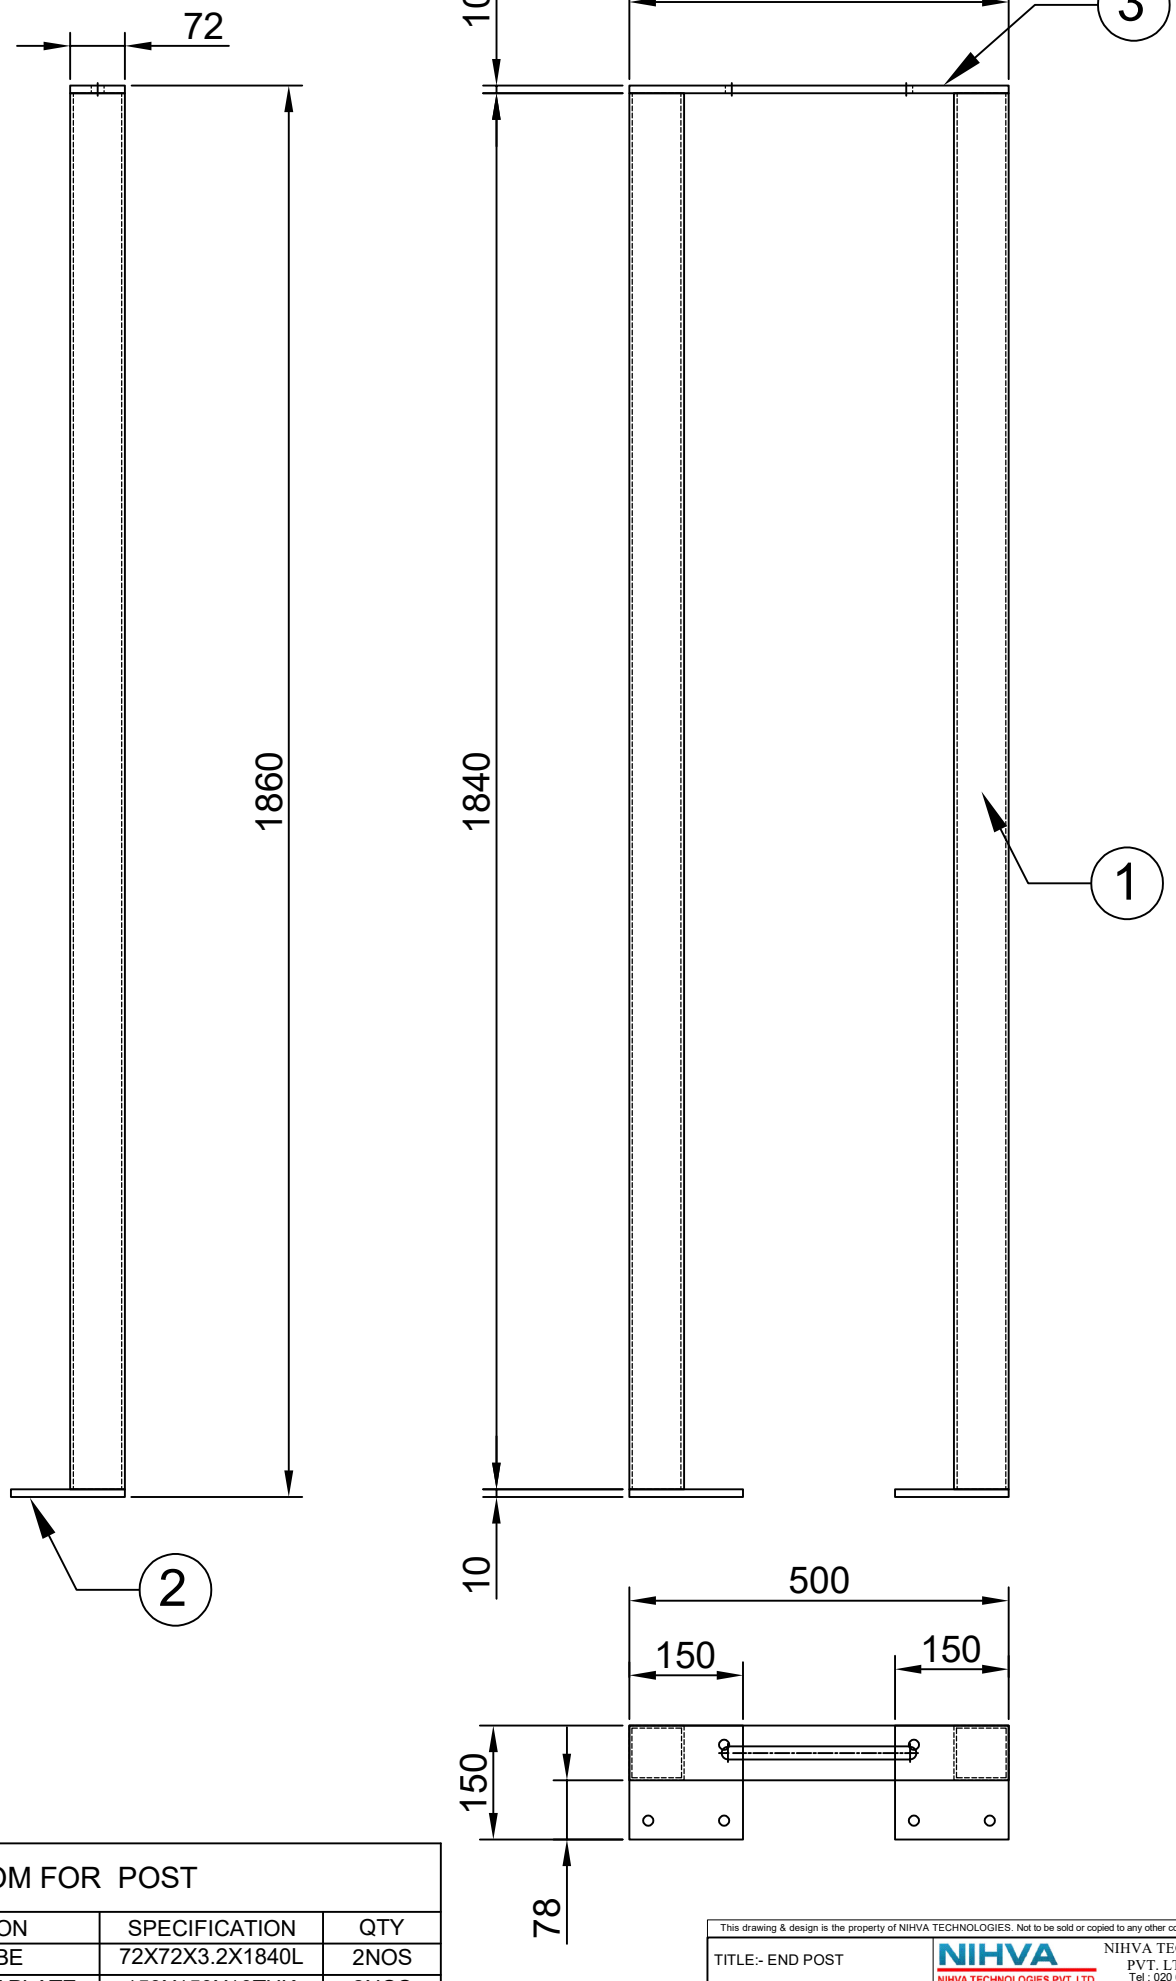


BOM FOR POST

SL NO.	DESCRIPTION	SPECIFICATION	QTY
1	MS SQ. TUBE	72X72X3.2X1840L	2NOS
2	POST SUPPORT PLATE	150X150X10THK	2NOS
3	ROLLER SUPPORT PLATE	500X90X10THK	1NO

Rev No.	Revision	Date	Revised By

This drawing & design is the property of NIHVA TECHNOLOGIES. Not to be sold or copied to any other concern.

TITLE:- END POST

NIHVA TECHNOLOGIES PVT. LTD.

NIHVA TECHNOLOGIES PVT. LTD. PUNE
Tel : 020 66304033
Email:- info@nihva.com
Website:- www.nihva.com

	NAME	DATE	SIGN
DRAWN	NIRMALA K	24/01/2023	
CHECK			
APPRD.	A.K	24/01/2023	

If any queries contact : design@nihva.com

ALL DIMENSION ARE IN mm

CLIENT - POONAM ROLLER FLOUR MILL PVT LTD

LOCATION -

PRODUCT - POST | QTY:-1 NOS

DWG NO:-NIHVA/22-23/MFG/0107 | REV- 0

SCALE: NTS | SCALE:– 1:1 | SHEET: 01 OF 01