




SIDE VIEW

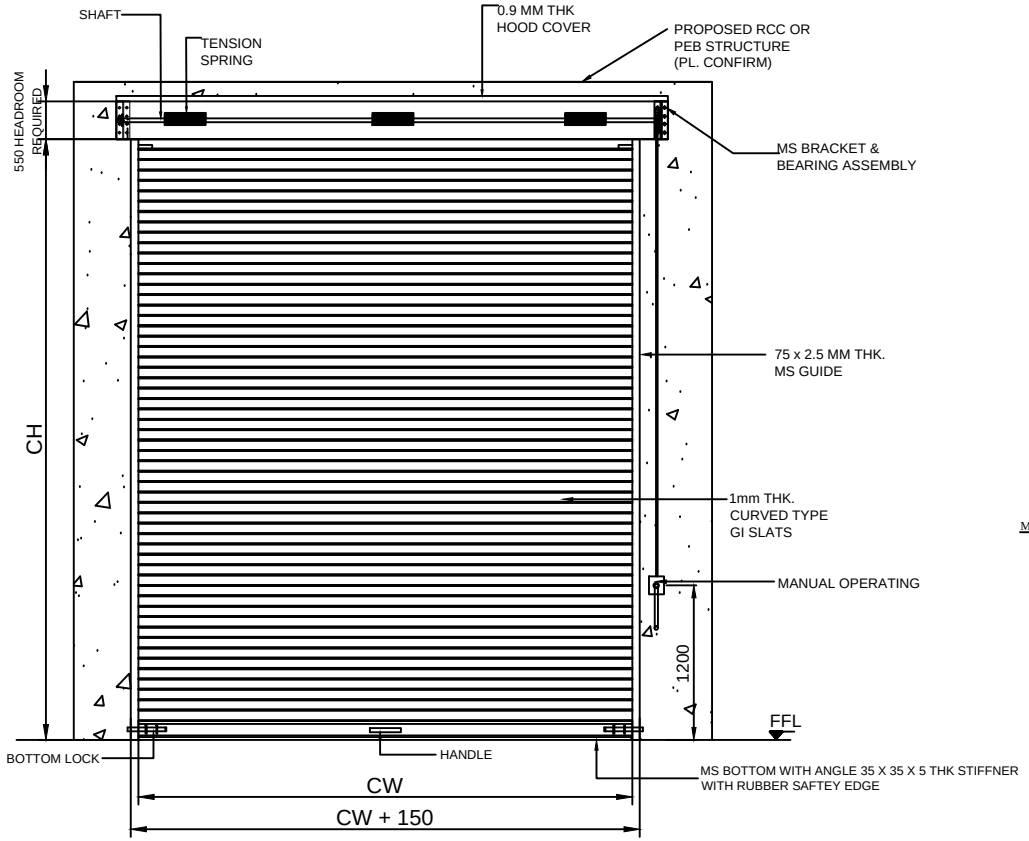


INSIDE ELEVATION

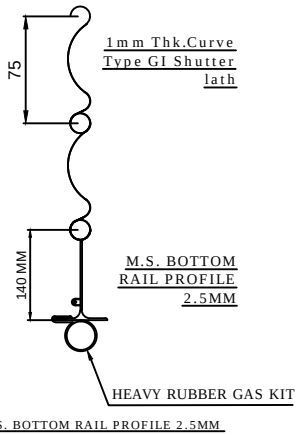

M.S. BOTTOM RAIL PROFILE 2.5MM

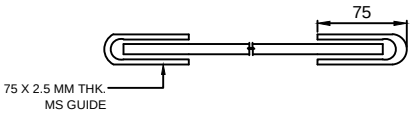

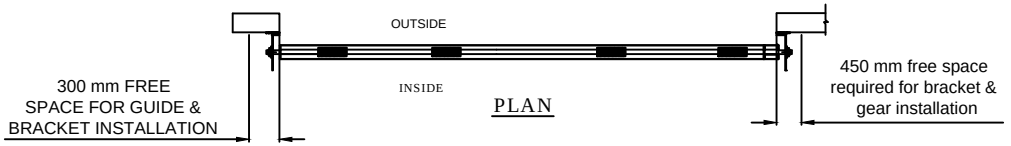

PLAN

TOLERANCE - ±5mm

NOTE-
1. ALL CIVIL WORK WILL BE CLIENT'S SCOPE.
2.STRUCTURE REQUIRED FOR SHUTTER IS IN CLIENT'S SCOPE.
3.FINAL FINISH OF SHUTTER WILL BE IN POWDER COATING OF APPROVED COLOR

S.N.	CLEAR WIDTH (CW)	CLEAR HEIGHT (CH)	QTY
1	3000	3300	02
2	4000	4500	01

This drawing & design is the property of NIHVA TECHNOLOGIES. Not to be sold or copied to any other concern.

TITLE	GEAR OPERATED ROLLING SHUTTER With Right side gearbox		
	NAME	SIGN	DATE
DRAWN	P.A		07.12.2019
CHECK	G.J		07.12.2019
APPRD.			

NIHVA TECHNOLOGIES PVT. LTD.
NIHVA TECHNOLOGIES PVT. LTD. PUNE
Tel : 020 66304033
Email:- info@nihva.com
Website:- www.nihva.com

CLIENT - PROGRESSIVE INFRA PROJECT PVT LTD.
PROJECT - VOSS
SITE LOCATION -
If any queries contact : design@nihva.com
DWG. NO. : NIHVA/19-20/0169 | REV- 0
ALL DIMENSION ARE IN mm | SCALE: NTS | WT: | SHEET: 01 OF 01