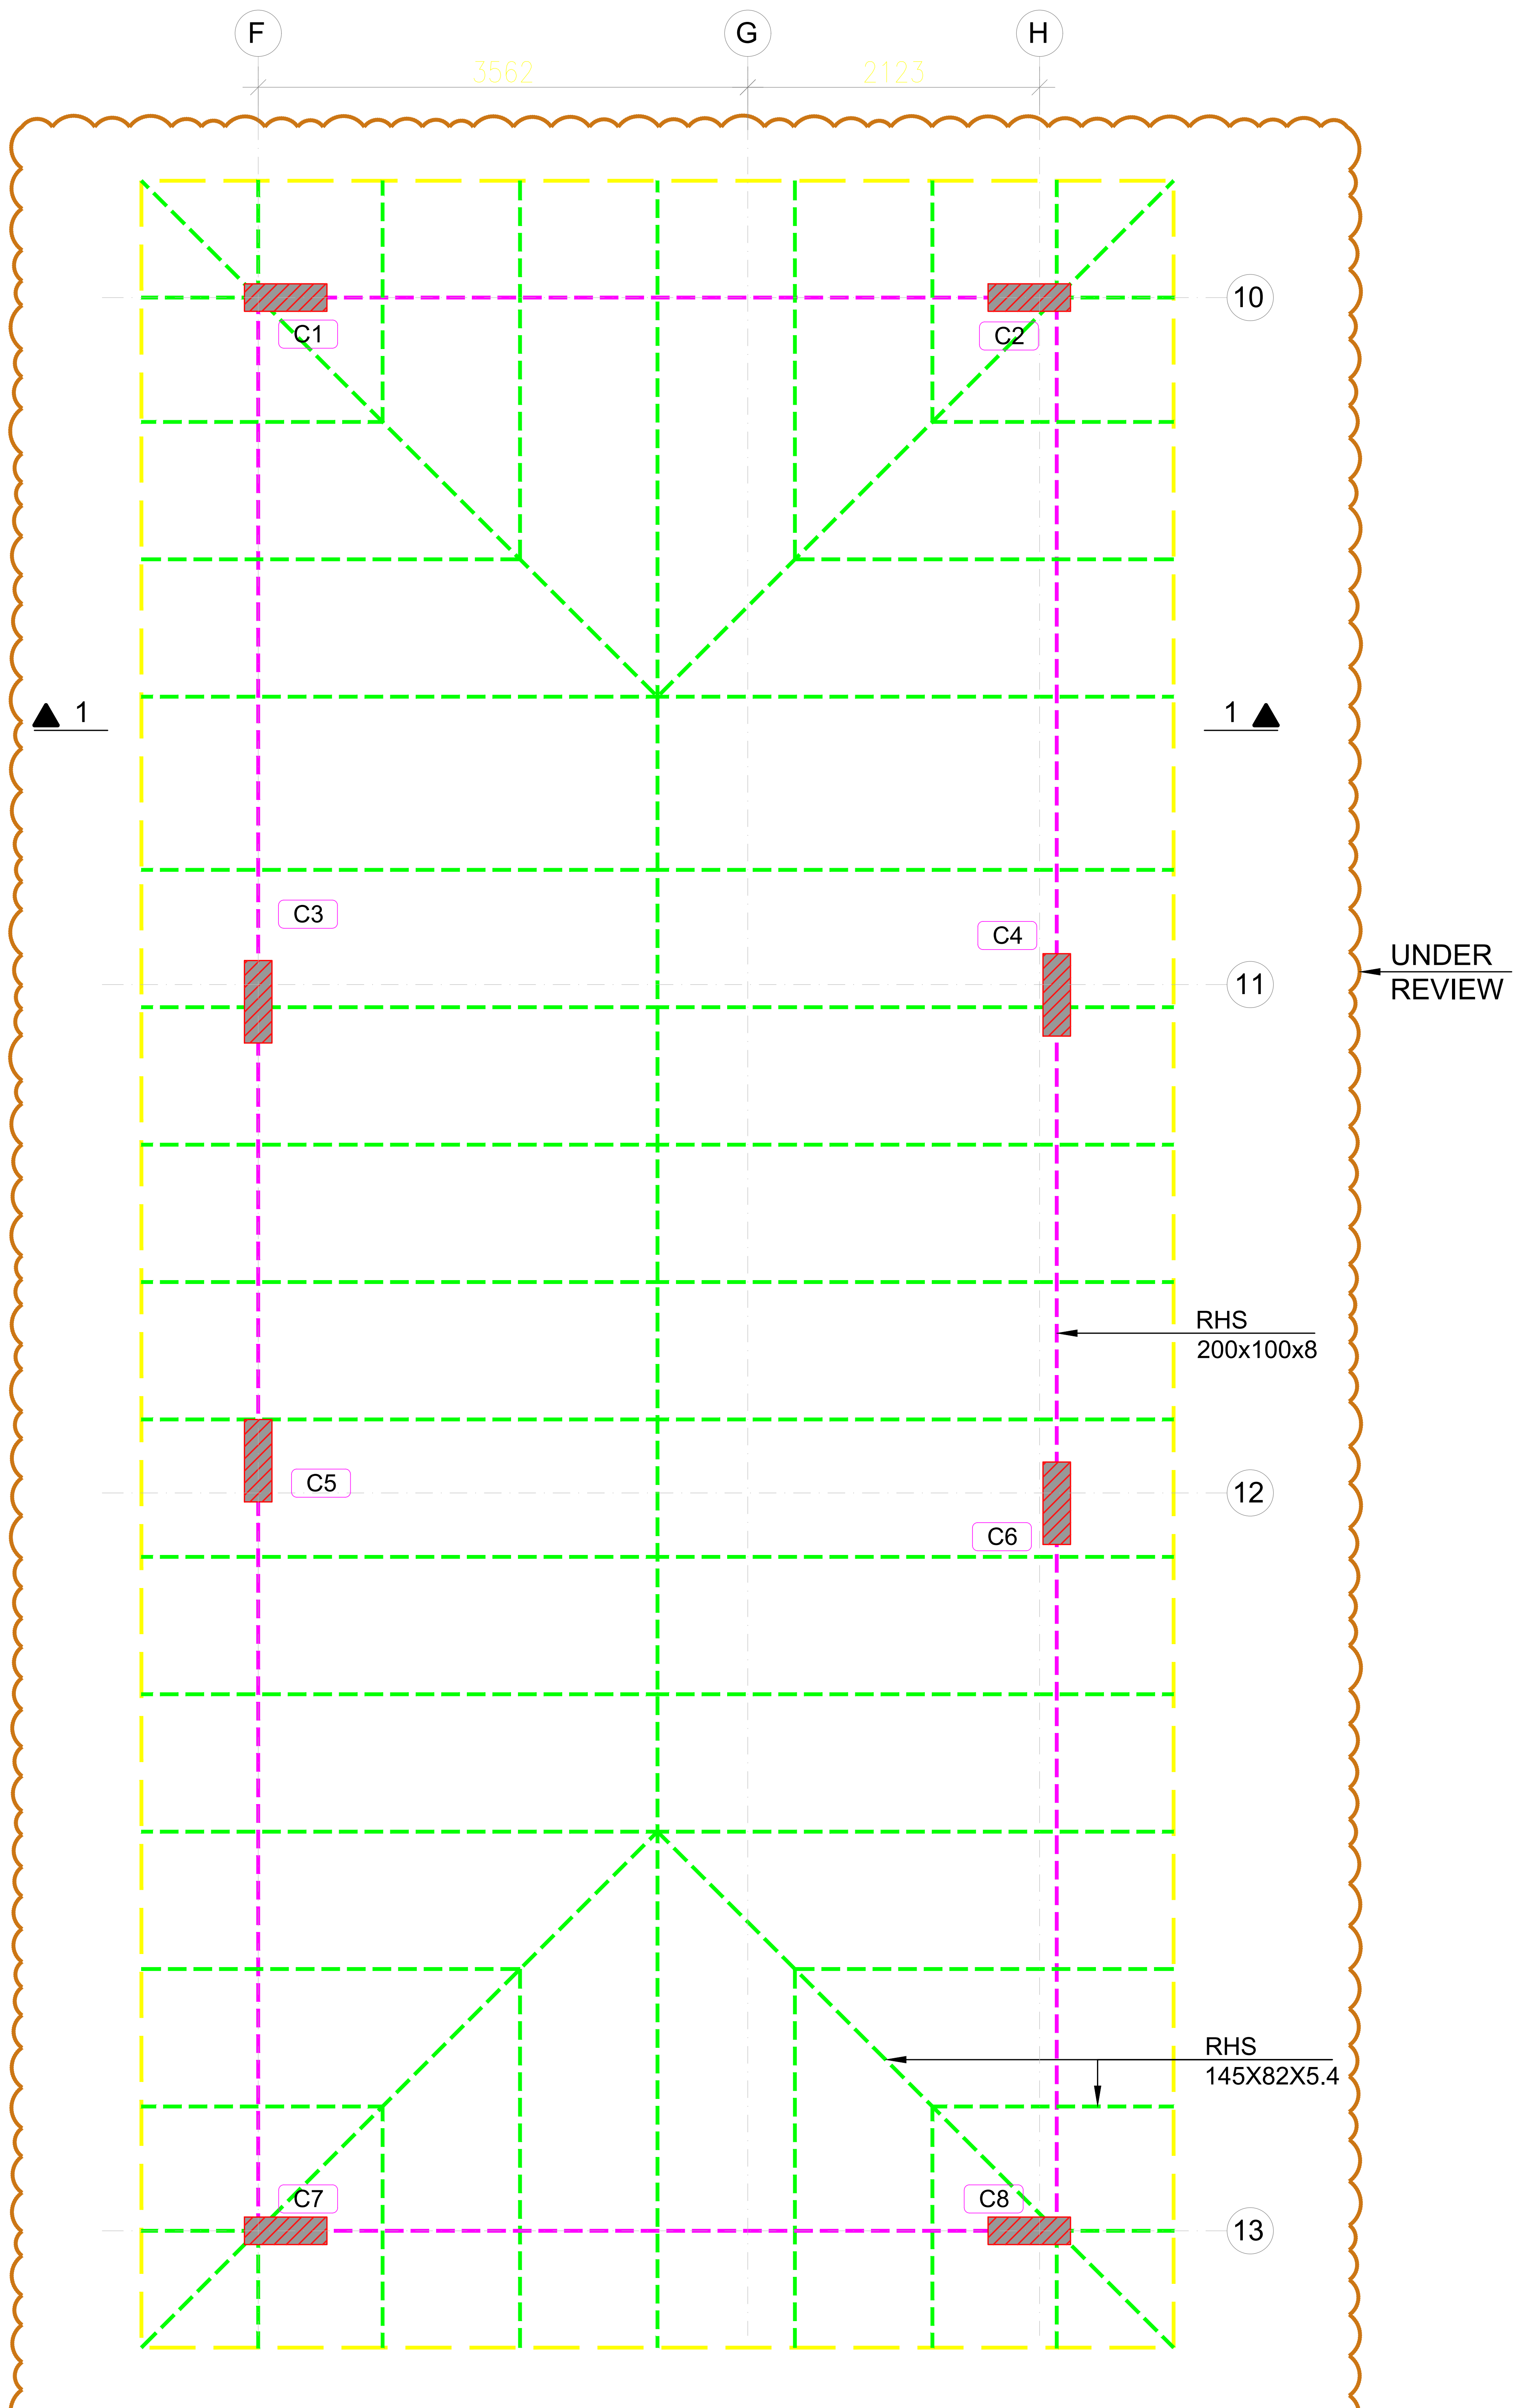
F
G
H
3562
2123
10
11
12
13
C1
C2
C3
C4
C5
C6
C7
C8
1
1
UNDER REVIEW
RHS 200x100x8
RHS 145X82X5.4

COLUMN TOP FRAMING PLAN (+587.915 M)

NOTE:

ALL COLUMNS TERMINATED AT +587.915 LVL.

ALL STRUCTURAL STEEL MEMBERS DESIGN & DETAILS AS PER VENDOR.

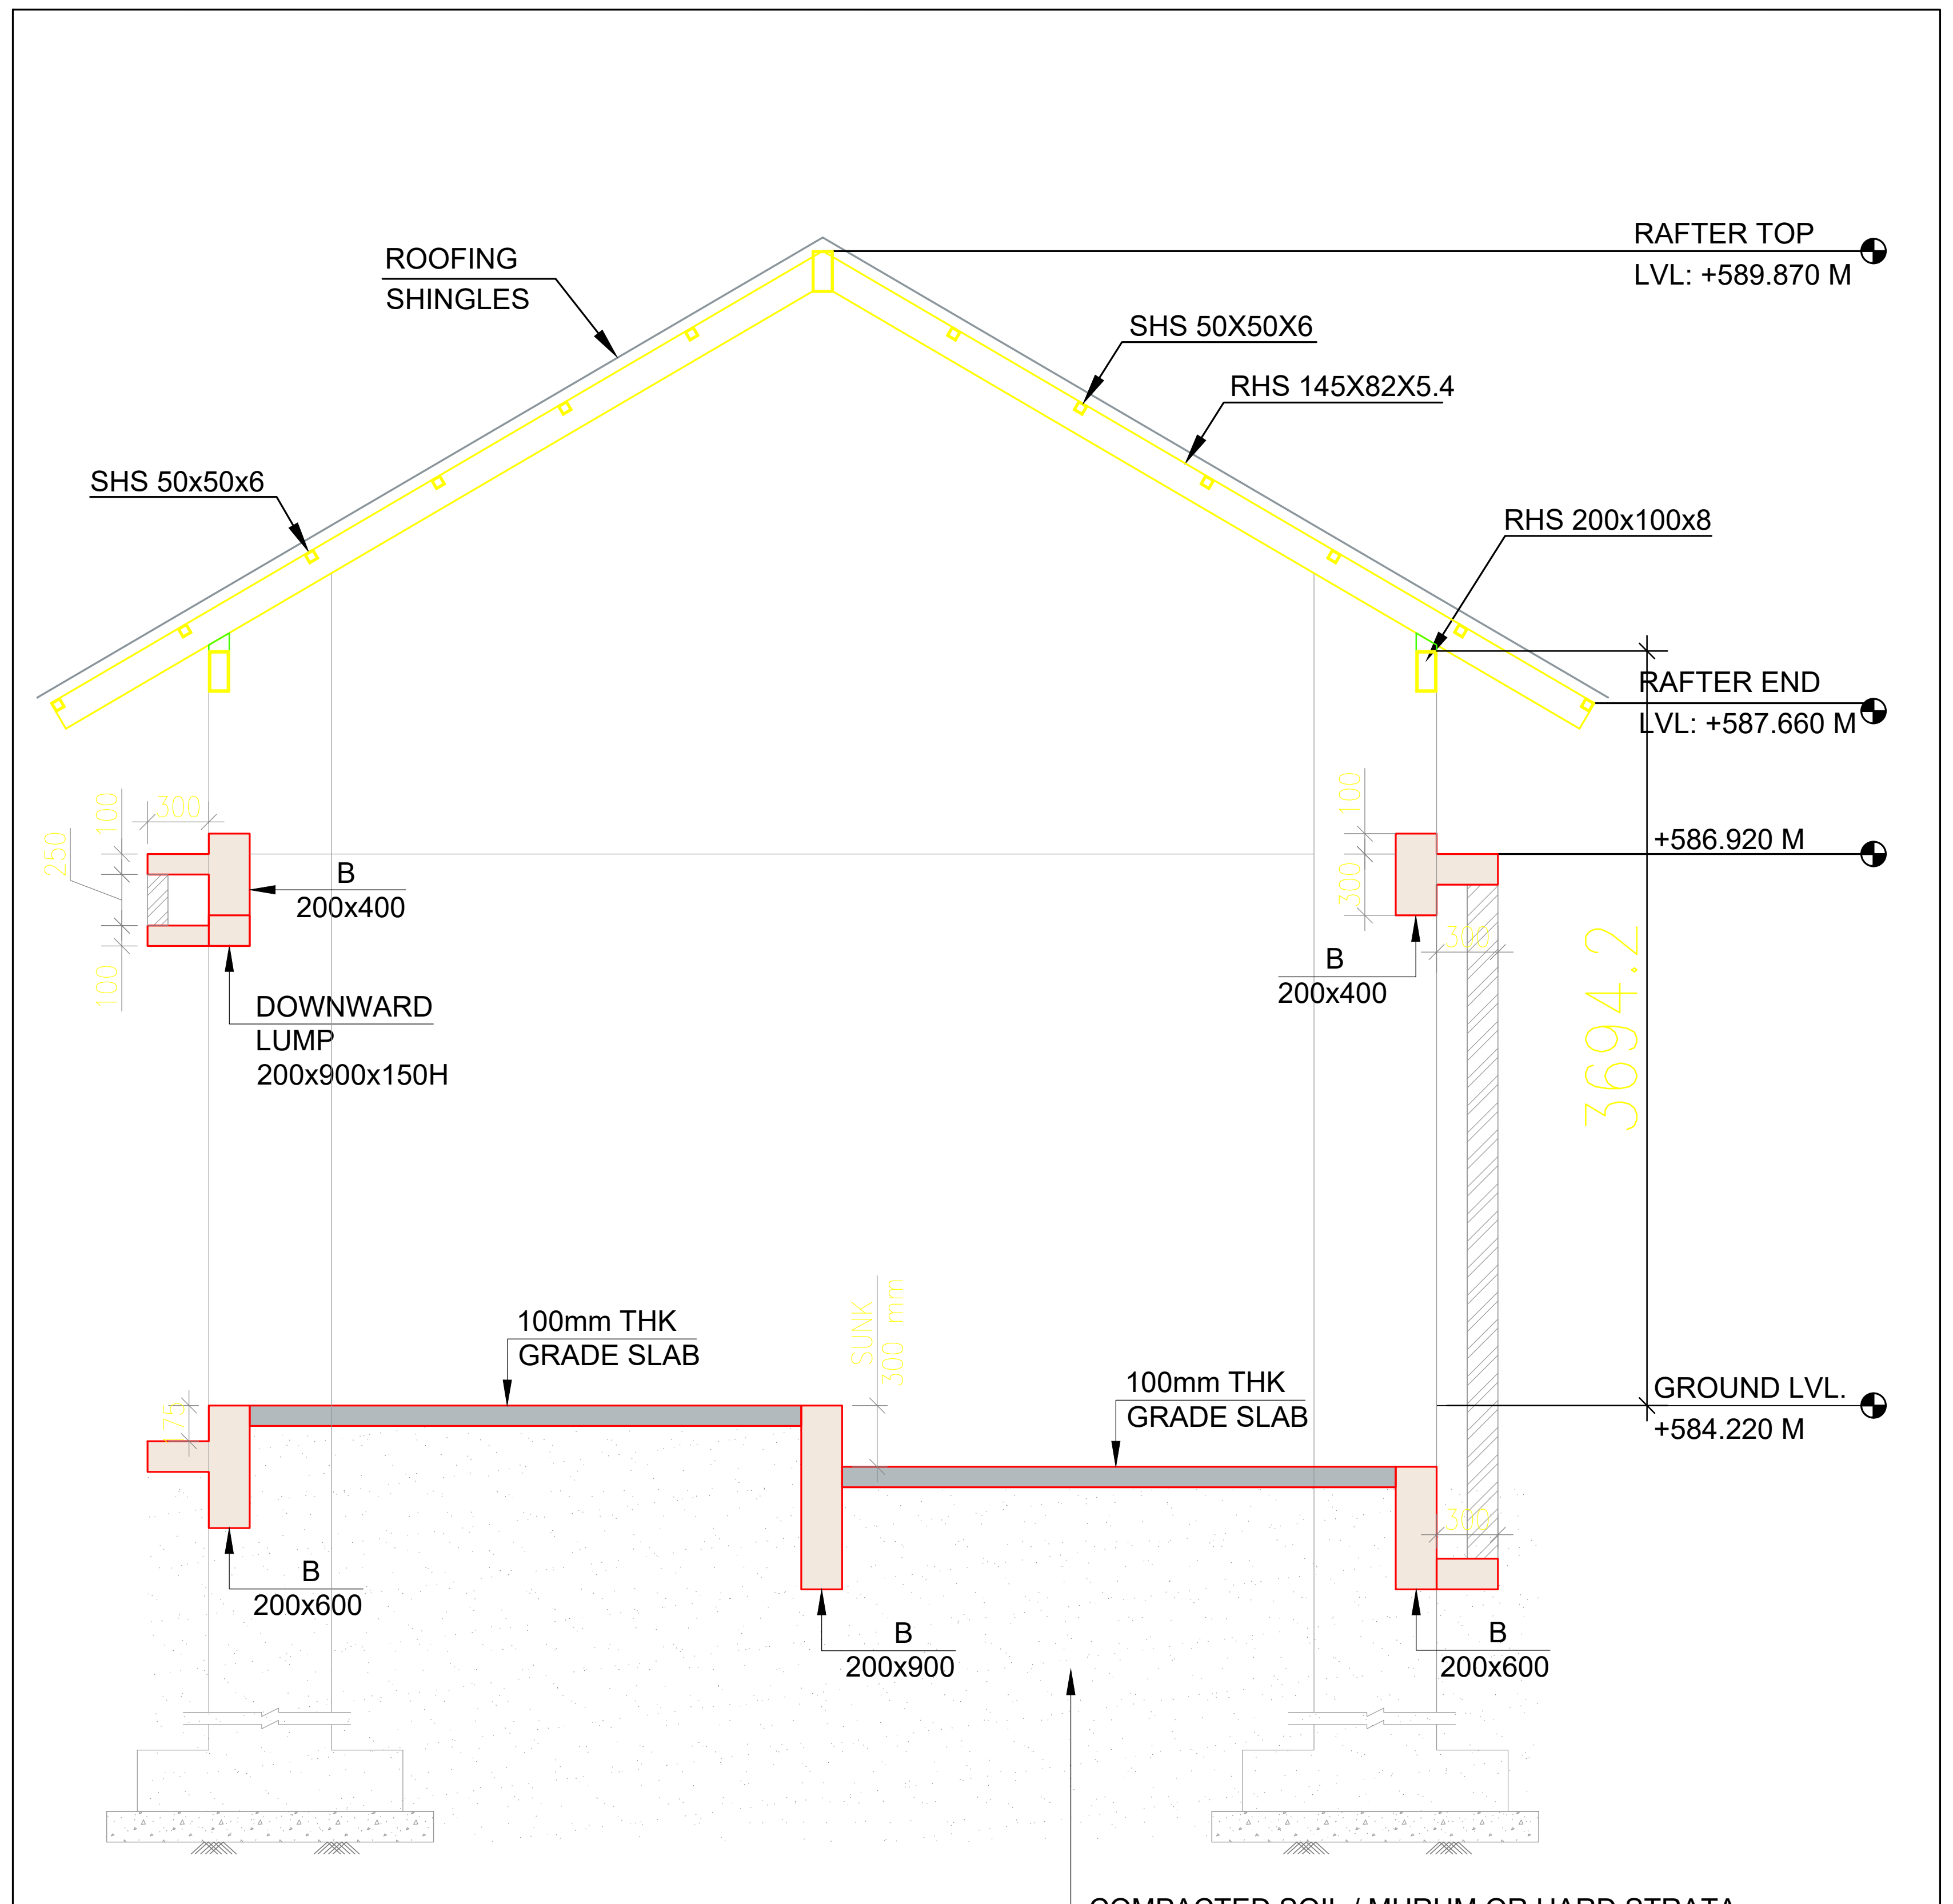
ROOFING SHINGLES
RAFTER TOP LVL: +589.870 M
SHS 50X50X6
RHS 145X82X5.4
SHS 50x50x6
RHS 200x100x8
RAFTER END LVL: +587.660 M
+586.920 M
B 200x400
DOWNWARD LUMP 200x900x150H
B 200x400
3694.2
100
300
250
100
100
300
300
100mm THK GRADE SLAB
SUNK 300 mm
100mm THK GRADE SLAB
GROUND LVL. +584.220 M
175
B 200x600
B 200x900
B 200x600
300

SECTION 1-1

COMPACTED SOIL / MURUM OR HARD STRATA.
REMOVE ALL LOOSE SOIL BEFORE
COMPACTION / RUBBLE SOILING.