

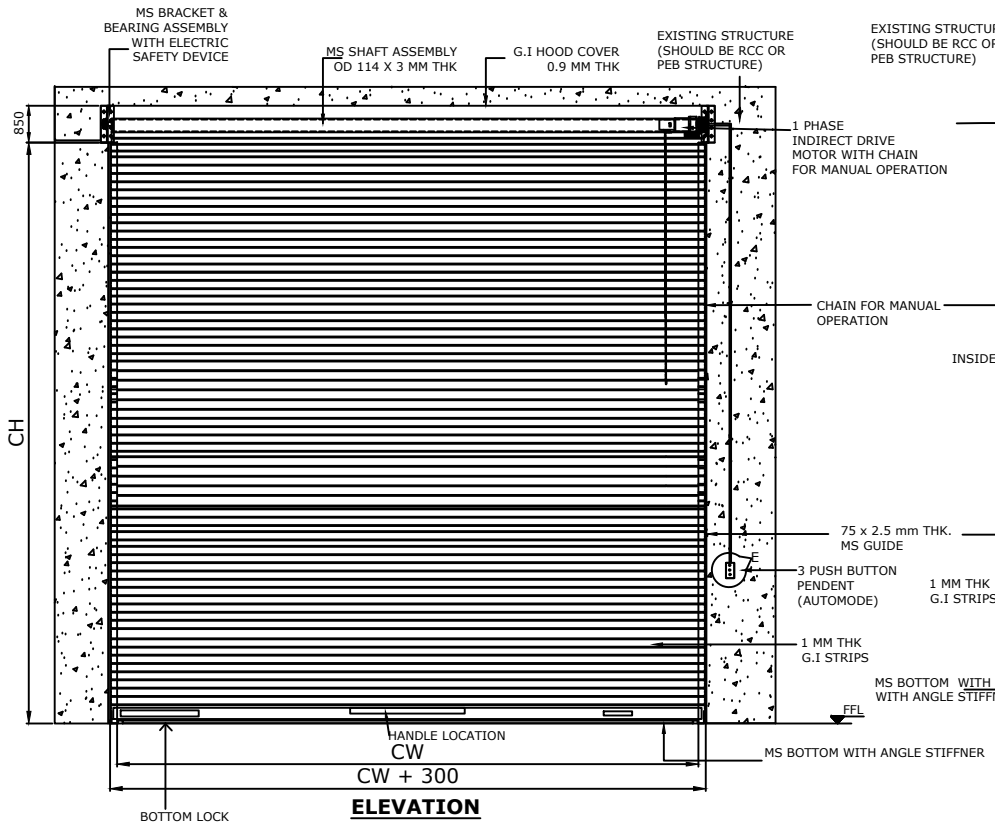



ELEVATION

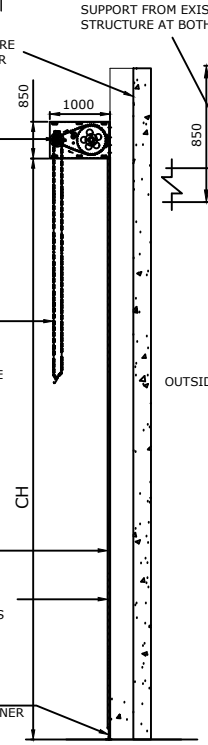


SIDE VIEW

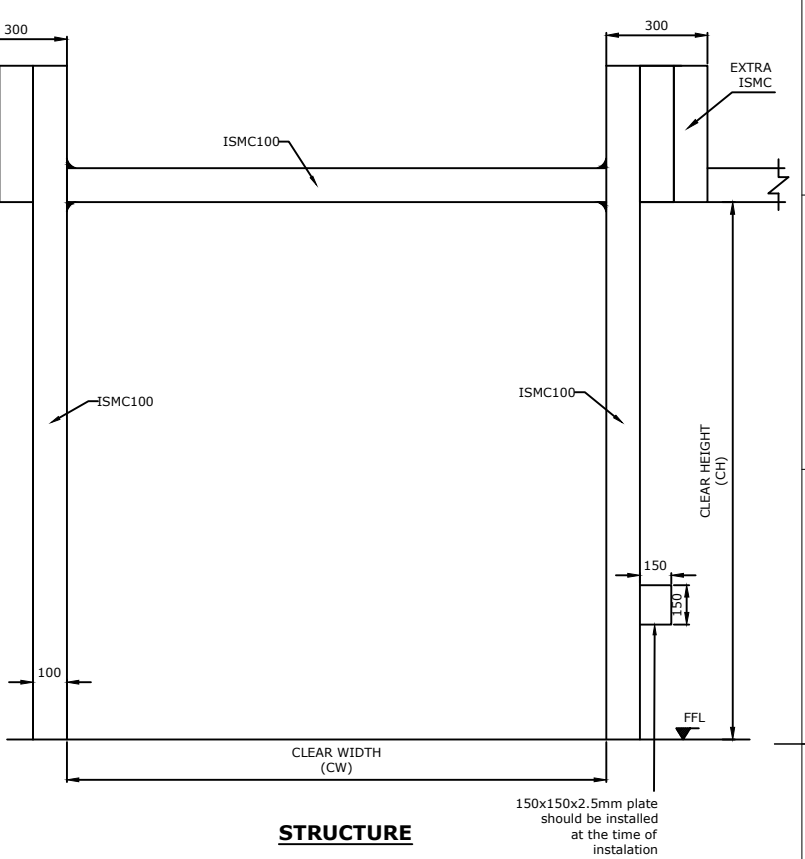


STRUCTURE

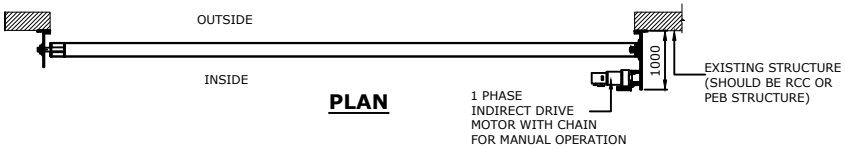

PLAN

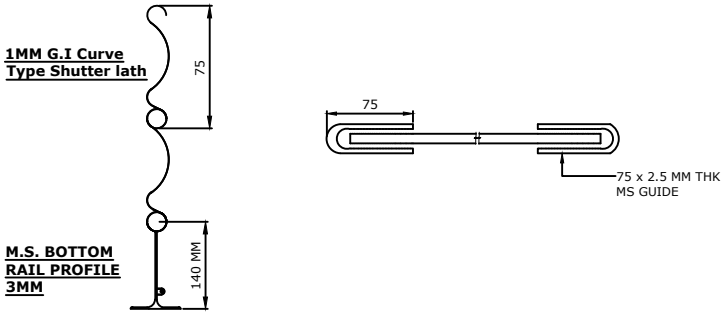

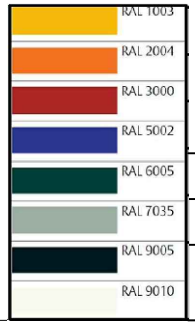

CLEAR WIDTH (CW)	CLEAR HEIGHT (CH)	QUANTITY
2450	2450	7
2450	3000	6

NOTE:
1. REQUIRED STRUCTURE FOR SHUTTER SHOULD BE IN CLIENT SCOPE.
2. REQUIRED POWER SUPPLY UP TO ROLLING SHUTTER IN CLIENT SCOPE.

This drawing & design is the property of NIHVA TECHNOLOGIES. Not to be sold or copied to any other concern.

TITLE: MOTORIZED ROLLING SHUTTER

NIHVA TECHNOLOGIES PVT. LTD.

NIHVA TECHNOLOGIES PVT. LTD. PUNE
Tel : 020 66304033
Email:- info@nihva.com
Website:- www.nihva.com

	NAME	SIGN	DATE
DRAWN	P.A		22.05.2020
CHECK	G.J		22.05.2020
APPRD.			

CLIENT - HIRANANDANI
PROJECT -
SITE LOCATION - CHENNAI
If any queries contact : design@nihva.com
DWG. NO. : NIHVA/20-21/0010
REV- 0
ALL DIMENSION ARE IN mm
SCALE: NTS
WT:
SHEET: