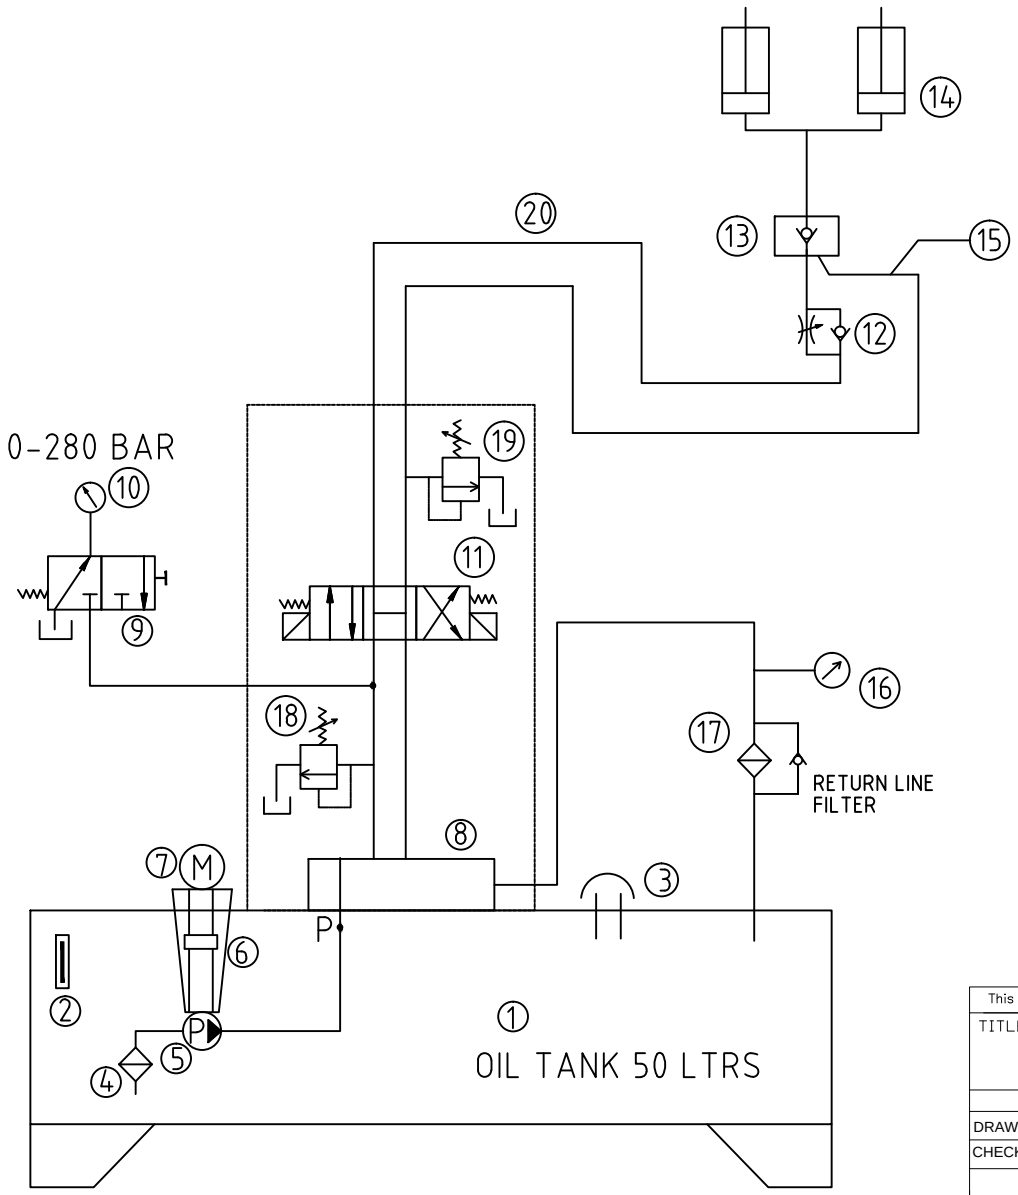


NO.	DESCRIPTION	MAKE	QTY.
20	FLEXIBLE HOSE 3/8" R1	PARKER	1
19	PRESSURE RELIEF VALVE MBA 01 C	YUKEN	1
18	PRESSURE RELIEF VALVE	REXROTH	1
17	RETURN LINE FILTER	HYDROLINE	1
16	RETURN LINE FILTER CLOGGING INDICATOR	HYDROLINE	1
15	FLEXIBLE HOSE 1/4", R1	PARKER	1
14	HYDRAULIC CYLINDER	NIHVA	2
13	PILOT OPERATED CHECK VALVE	REXROTH	1
12	FLOW CONTROL VALVE TCV12	TUCSON	1
11	DIRECTION CONTROL NG6 SIZE	REXROTH	1
10	PRESSURE GAUGE 63MM DIAL 0-280 BAR	WIKA	1
9	PRESSURE GAUGE ISOLATOR	FENNER	1
8	MANIFOLD BLOCK	NIHVA	1
7	ELECTRIC MOTOR 3HP/1440/FLANGE	SIEMENS	1
6	BELL HOUSING AND COUPLING	POLYHYDRN	1
5	GEAR PUMP 6 LPM	REXROTH	1
4	SUCTION STRAINER SC3007	HYDROLINE	1
3	FILLER BREATHER FSB25	HYDROLINE	1
2	OIL LEVEL GAUGE LG3	HYDROLINE	2
1	OIL RESRVIOR 50 LITERS	NIHVA	1

BILL OF MATERIAL

This drawing & design is the property of NIHVA TECHNOLOGIES. Not to be sold or copied to any other concern.

TITLE:- HYDRAULIC CIRCUIT SCISSOR LIFT

	NAME	SIGN	DATE
DRAWN	P.V.A		29.07.2019
CHECK	V.M.T		29.07.2019

If any queries contact : design@nihva.com

ALL DIMENSION ARE IN mm

NIHVA TECHNOLOGIES PVT. LTD.
NIHVA TECHNOLOGIES PVT. LTD. PUNE
Tel : 020 66304033
Email:- info@nihva.com
Website:- www.nihva.com

CLIENT - METROLAB ENGINEERING PVT .LTD

PROJECT -

SITE LOCATION - CHINCHWAD

DWG. NO. : NIHVA/19-20/0066 | REV- 0

SCALE: NTS | WT: | SHEET: 02 OF 02