


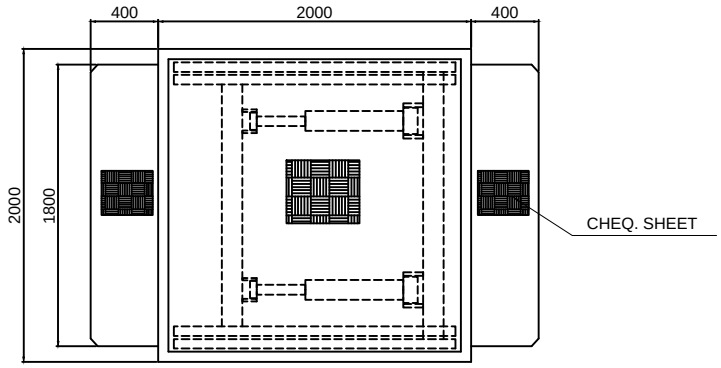


CAPACITY	2 TON
PLATFORM SIZE	2000(L) X 2000(W)
POWER PACK	3 HP, 3 PH
SHUT HEIGHT	500 MM
LIFT HEIGHT	1500 MM
OPEN HEIGHT	2000 MM

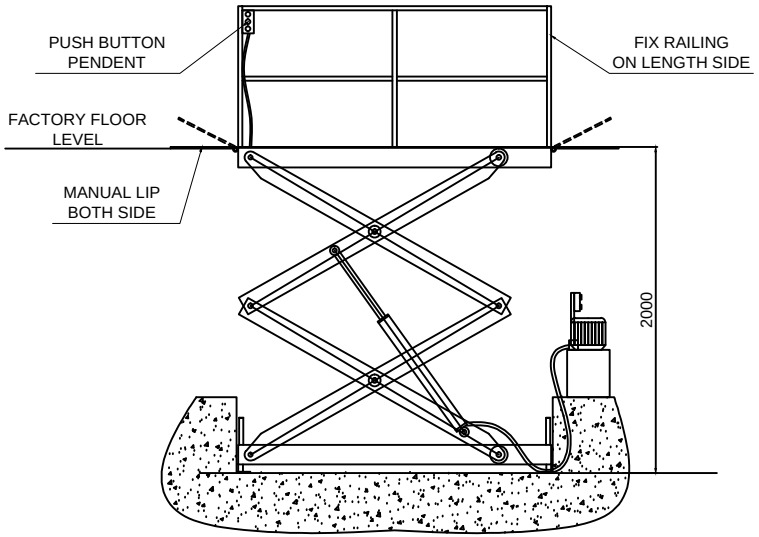

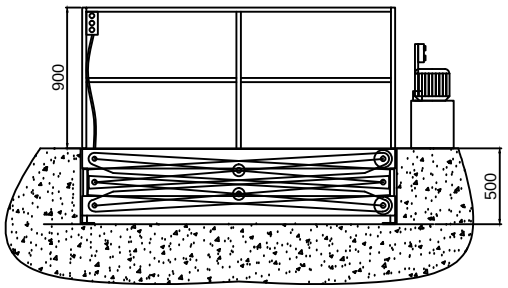

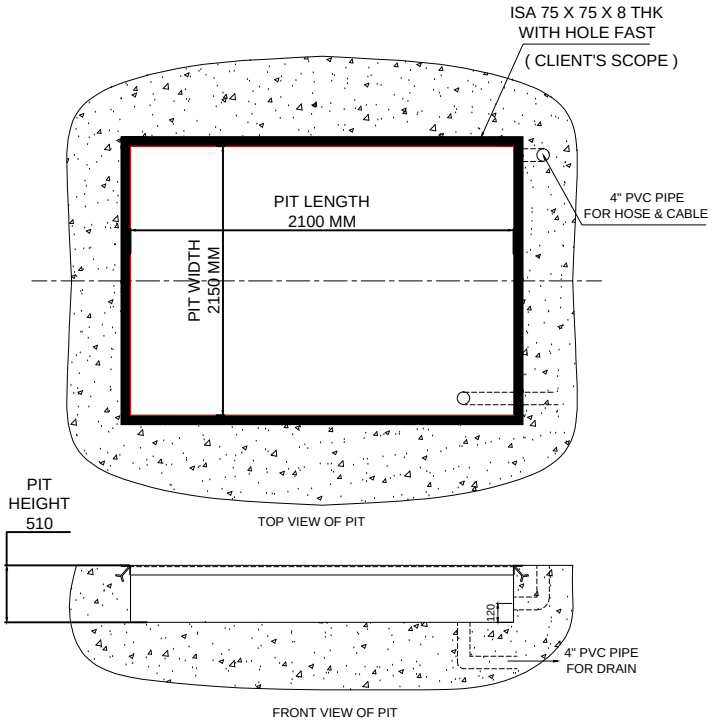

TOLERANCE - ±10mm

NOTE :-
1. PIT LEVEL SHOULD PARALLEL.
2. PROVISION OF 75 MM SPACE IN PIT ON BOTH LENGTH SIDE IS FOR INSTALLATION PURPOSE.
3. FLEXIBLE HOSE LENGTH - 7 MTR FROM CYLINDER.
4. MAIN SUPPLY CABLE WILL BE IN CLIENT SCOPE.

COLOR : RAL 1004 (GOLDEN YELLOW)

This drawing & design is the property of NIHVA TECHNOLOGIES. Not to be sold or copied to any other concern.

TITLE: SCISSOR LIFT GA DRAWING

	NAME	SIGN	DATE
DRAWN	P.V.A		17.06.2019
CHECK	V.M.T		17.06.2019
APPRD.			

NIHVA TECHNOLOGIES PVT. LTD.
NIHVA TECHNOLOGIES PVT. LTD. PUNE
Tel : 020 66304033
Email:- info@nihva.com
Website:- www.nihva.com

CLIENT - RMK INFRA STRUCTURE PVT LTD

PROJECT -

SITE LOCATION - TALEGAON

If any queries contact : design@nihva.com

DWG. NO. : NIHVA/19-20/0031 | REV- 0

ALL DIMENSION ARE IN mm | SCALE: NTS | WT: | SHEET: 01 OF 01