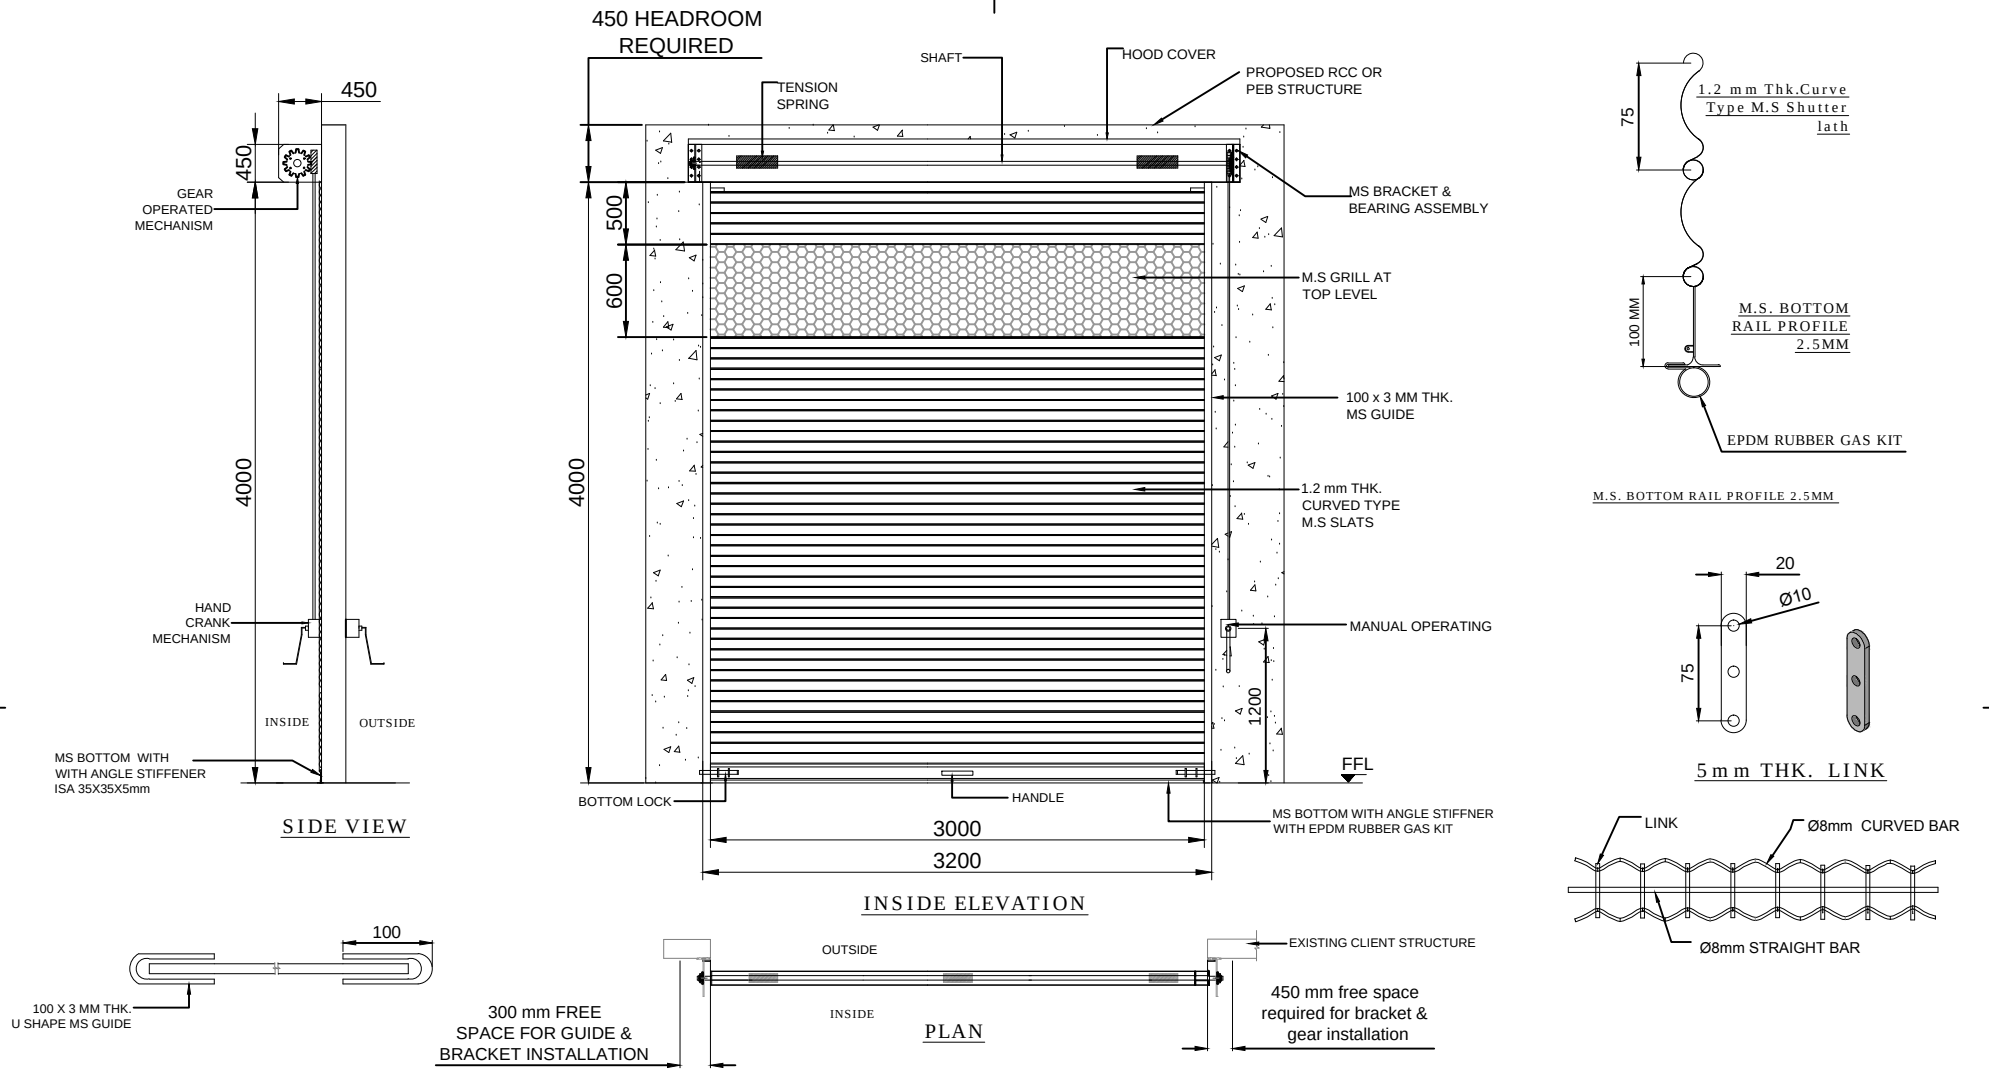


TOLERANCE - ±10mm

NOTE-
1. ALL CIVIL WORK WILL BE CLIENT'S SCOPE.
2.STRUCTURE REQUIRED FOR SHUTTER IS IN CLIENT'S SCOPE.
3.FINAL FINISH OF SHUTTER WILL BE IN POWDER COATING OF APPROVED COLOR .

REV NO	REV DATE	DRAWN	REMARK
R04	11.11.2019	P.A	1. DETAILS ADD.
R03	06.11.2019	P.A	1. GRILL POSITION CHANGE 2. CLEAR HEIGHT CHANGE
R02	05.11.2019	P.A	1. GRILL POSITION CHANGE 2. SLAT THICKNESS CHANGE
R01	19.10.2019	P.A	1. GRILL ADDED

This drawing & design is the property of NIHVA TECHNOLOGIES. Not to be sold or copied to any other concern.

TITLE: GEAR OPERATED ROLLING SHUTTER 3m X 4 m
Right side gear box.

	NAME	SIGN	DATE
DRAWN	P.A		16.10.2019
CHECK	G.J		16.10.2019
APPRD.			

If any queries contact : design@nihva.com

ALL DIMENSION ARE IN mm

NIHVA TECHNOLOGIES PVT. LTD.
NIHVA TECHNOLOGIES PVT. LTD. PUNE
Tel : 020 66304033
Email:- info@nihva.com
Website:- www.nihva.com

CLIENT - PROGRESSIVE INFRA PROJECT PVT. LTD.

PROJECT -

SITE LOCATION - PUNE

DWG. NO. : NIHVA/19-20/0136/R04 | REV- R04

SCALE: NTS | WT: | SHEET: 01 OF 01