
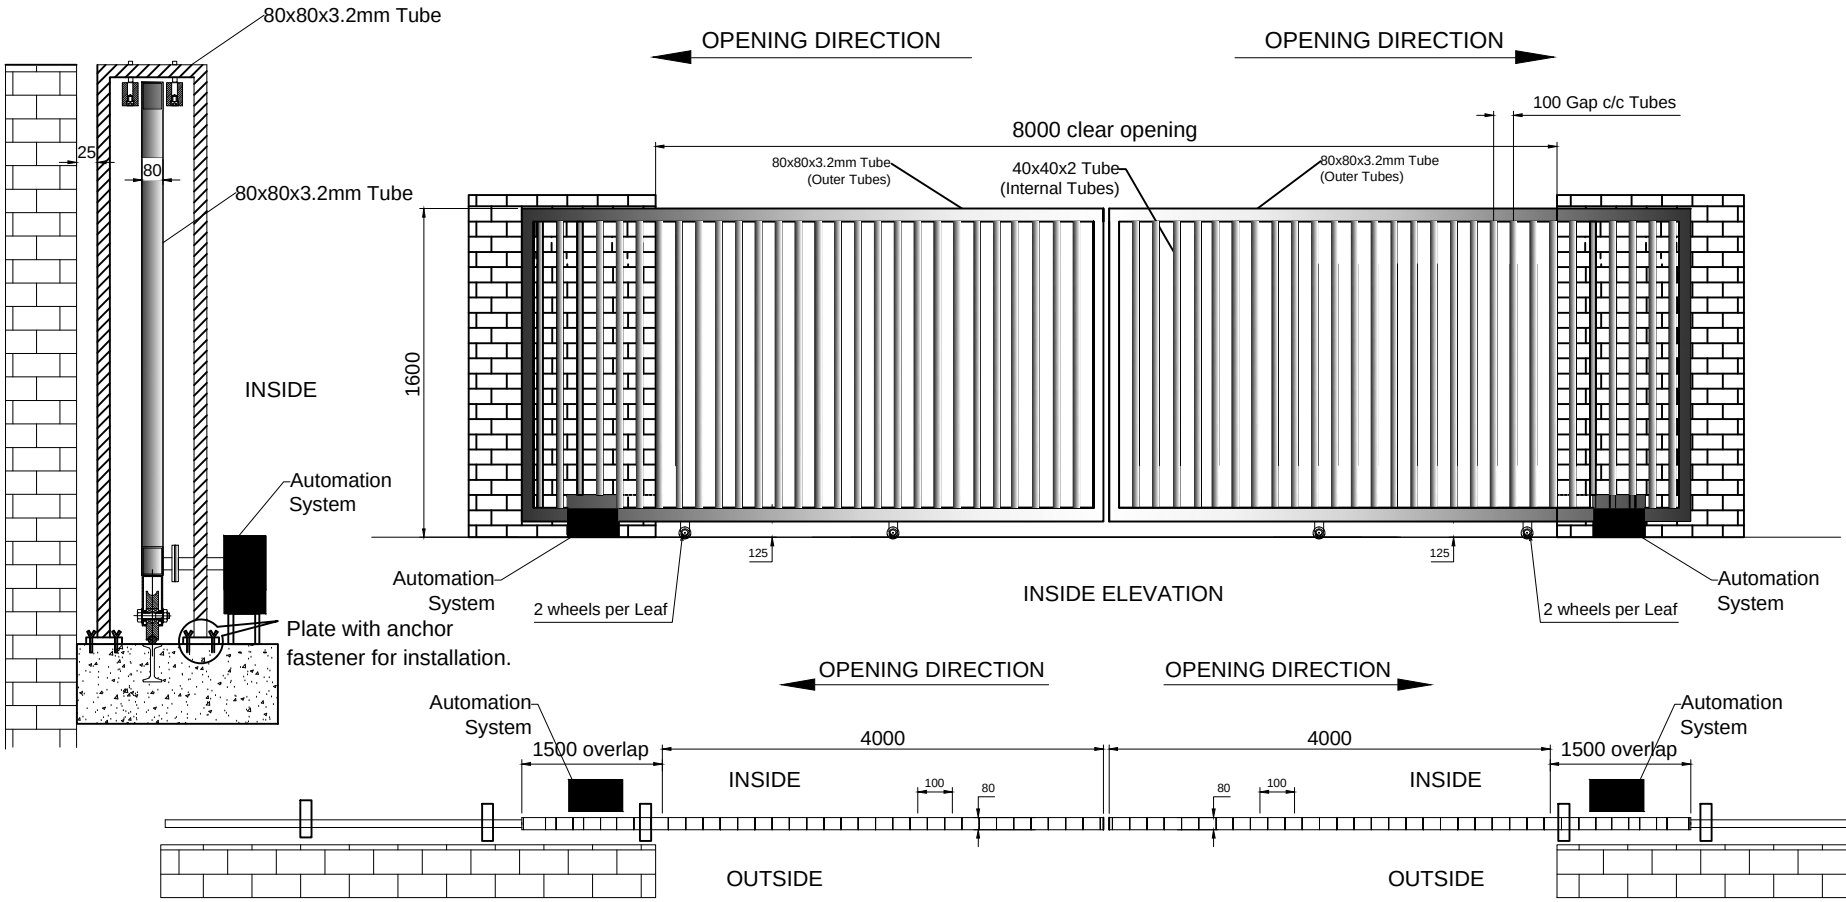


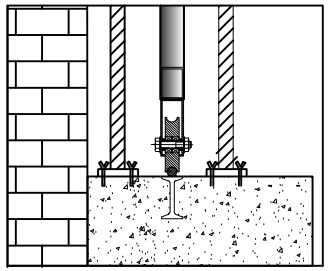

Clear Opening size -8000mm x 1600mm
Total No. of Leaf - 2 Leaf
NOTE :- *ALL REQ. CIVIL WORK WILL BE IN CLIENT SCOPE.

DOUBLE LEAF SLIDING GATE

This drawing & designing is the property of NIHVA TECHNOLOGIES. Not be sold or copy to any other concern.

TITLE	DOUBLE LEAF MOTORISED SLIDING GATE	
	SIGN	DATE
DRAWN	OMKAR	27/02/16
CHECK	ANIL	27/02/16
REV.	01	
APPROVAL		

NIHVA TECHNOLOGY PVT. LTD. PUNE
Tel : 020 66304033
Email:- info@nihva.com
Website:- www.nihva.com

CLIENT - HYOSUNG T&D	
PROJECT -	
SITE -	
DWG. NO. : NIHVA/15-16/232	
SCALE: 01	WT: SHEET: 01 OF 01

If any queries contact : projects@nihva.com
ALL DIMENSION ARE IN mm