
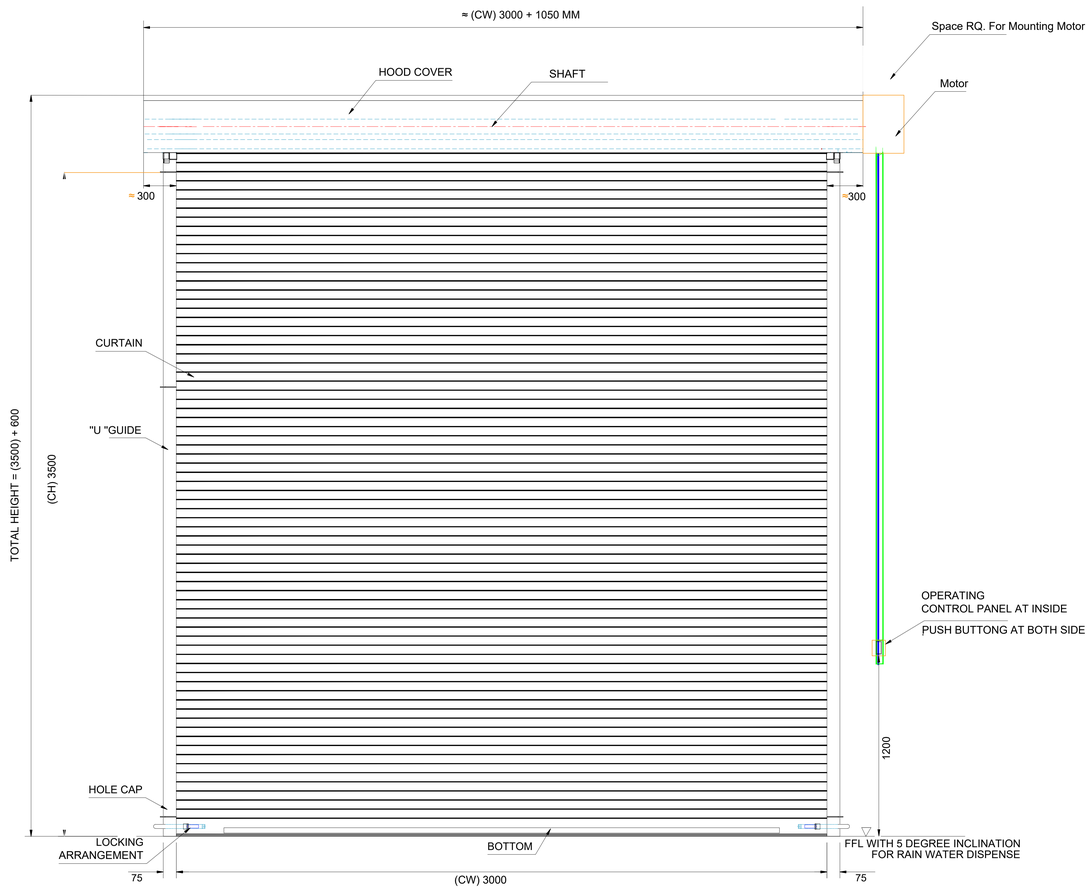


INSIDE ELEVATION

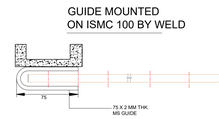

" U " TYPE GUIDE

☐	CAT - I	APPROVED - *No Further Comments*
☑	CAT - II	APPROVED - *Subjected to Incorporation of Comments as Marked.*
☐	CAT - III	NOT APPROVED *Resubmit with Incorporation of Comments as Marked / Discussed.*
☐	CAT - IV	INVALID SUBMISSION *Due to Non-Conformity of Tender specifications / drawings*

(Sign & Date)	(Name & Designation)	(Remarks)

COMMON COMMENTS :-
1. CONTRACTOR NEEDS TO VERIFY THE DIMENSION OF THE OPENING ON SITE BEFORE PROCEEDING FOR EXECUTION.
2. OPENING CONDITION OF THE ROLLING SHUTTER SHOULD BE AS PER THE PLAN
3. NO DEVIATION FROM TENDER SPECIFICATION WILL BE ALLOWED.
4. COLOR OF CURTAIN, BRACKET, SHAFT,SIDE GUIDES, BOTTOM PATTI, HOOD COVER PU SPRAY PAINTED SIMILAR TO RAL 9006 OVER 1COAT OF EPOXY PRIMER

TECHNICAL SPECIFICATION:-

SR.	SPECIFICATION	DETAILS
1.	Description	Double Wall PUF Insulated Motorised Rolling Shutter
2.	Drive & Motor	Jielong Make GKJS-400/11 3 Phase With Inbuilt Limit Switches.Manual Chain Option In Supply Failure. Torque: 65 Nm , Power :1.1kW
3.	Control Switch	IP 54 Rated Control Card With 3 stage Operating Push Button
4.	Slat	Galvanised Steel - 95 x 19 mm With PUF Filled Inside (THK-0.5 mm TCT)
5.	Density	48 kg /m3 (For Wind Speed 50 m/Sec)
6.	Bottom Profile	MS Plate 100 x 2 mm Thk. with Angle Stiffner WITH RUBBER SEAL
7.	Guide Profile	M.S." U " Shape profile 75 x 2 mm Thk.
8.	Hood Cover & Motor Cover	Made of GI Sheet Thickness 0.9 mm
9.	Accessories	Control Panel,Push Button On Both Side,In-Built Limit Switches
10.	Surface Finish	Powder Coating RAL-9006

SHUTTER SIZES :-

SR.	CLEAR WIDTH	CLEAR HEIGHT	QTY.
01	3000	3500	01

(1) All Cables & Ele.Conduits to be provided by RINAC
(2) All Civil Work in Client Scope


This drawing & designing is the property of NIHVA TECHNOLOGIES. Not to be sold or copied to any other concern.


TITLE :-
DOUBLE WALL PUF INSULATED
MOTORISED ROLLING SHUTTER

NIHVA TECHNOLOGIES PVT. LTD.
NIHVA TECHNOLOGIES
PVT. LTD. PUNE
Tel : 020 66304033
Email:- info@nihva.com
Website:- www.nihva.com

	NAME	DATE
DRAWN	J.S.	19/01/2024
CHECK	A.K.	19/01/2024
APPROVAL	V.T.	19/01/2024

CLIENT - RINAC
PROJECT -ROLLING SHUTTER
FORMAT NO - NIHVA-DD-F-03
DWG. NO. : NIHVA/23-24/104 REV-01
SCALE: NTS WT: SHEET: 01 OF 01
ALL DIMENSION ARE IN mm
If any queries contact : design@nihva.com

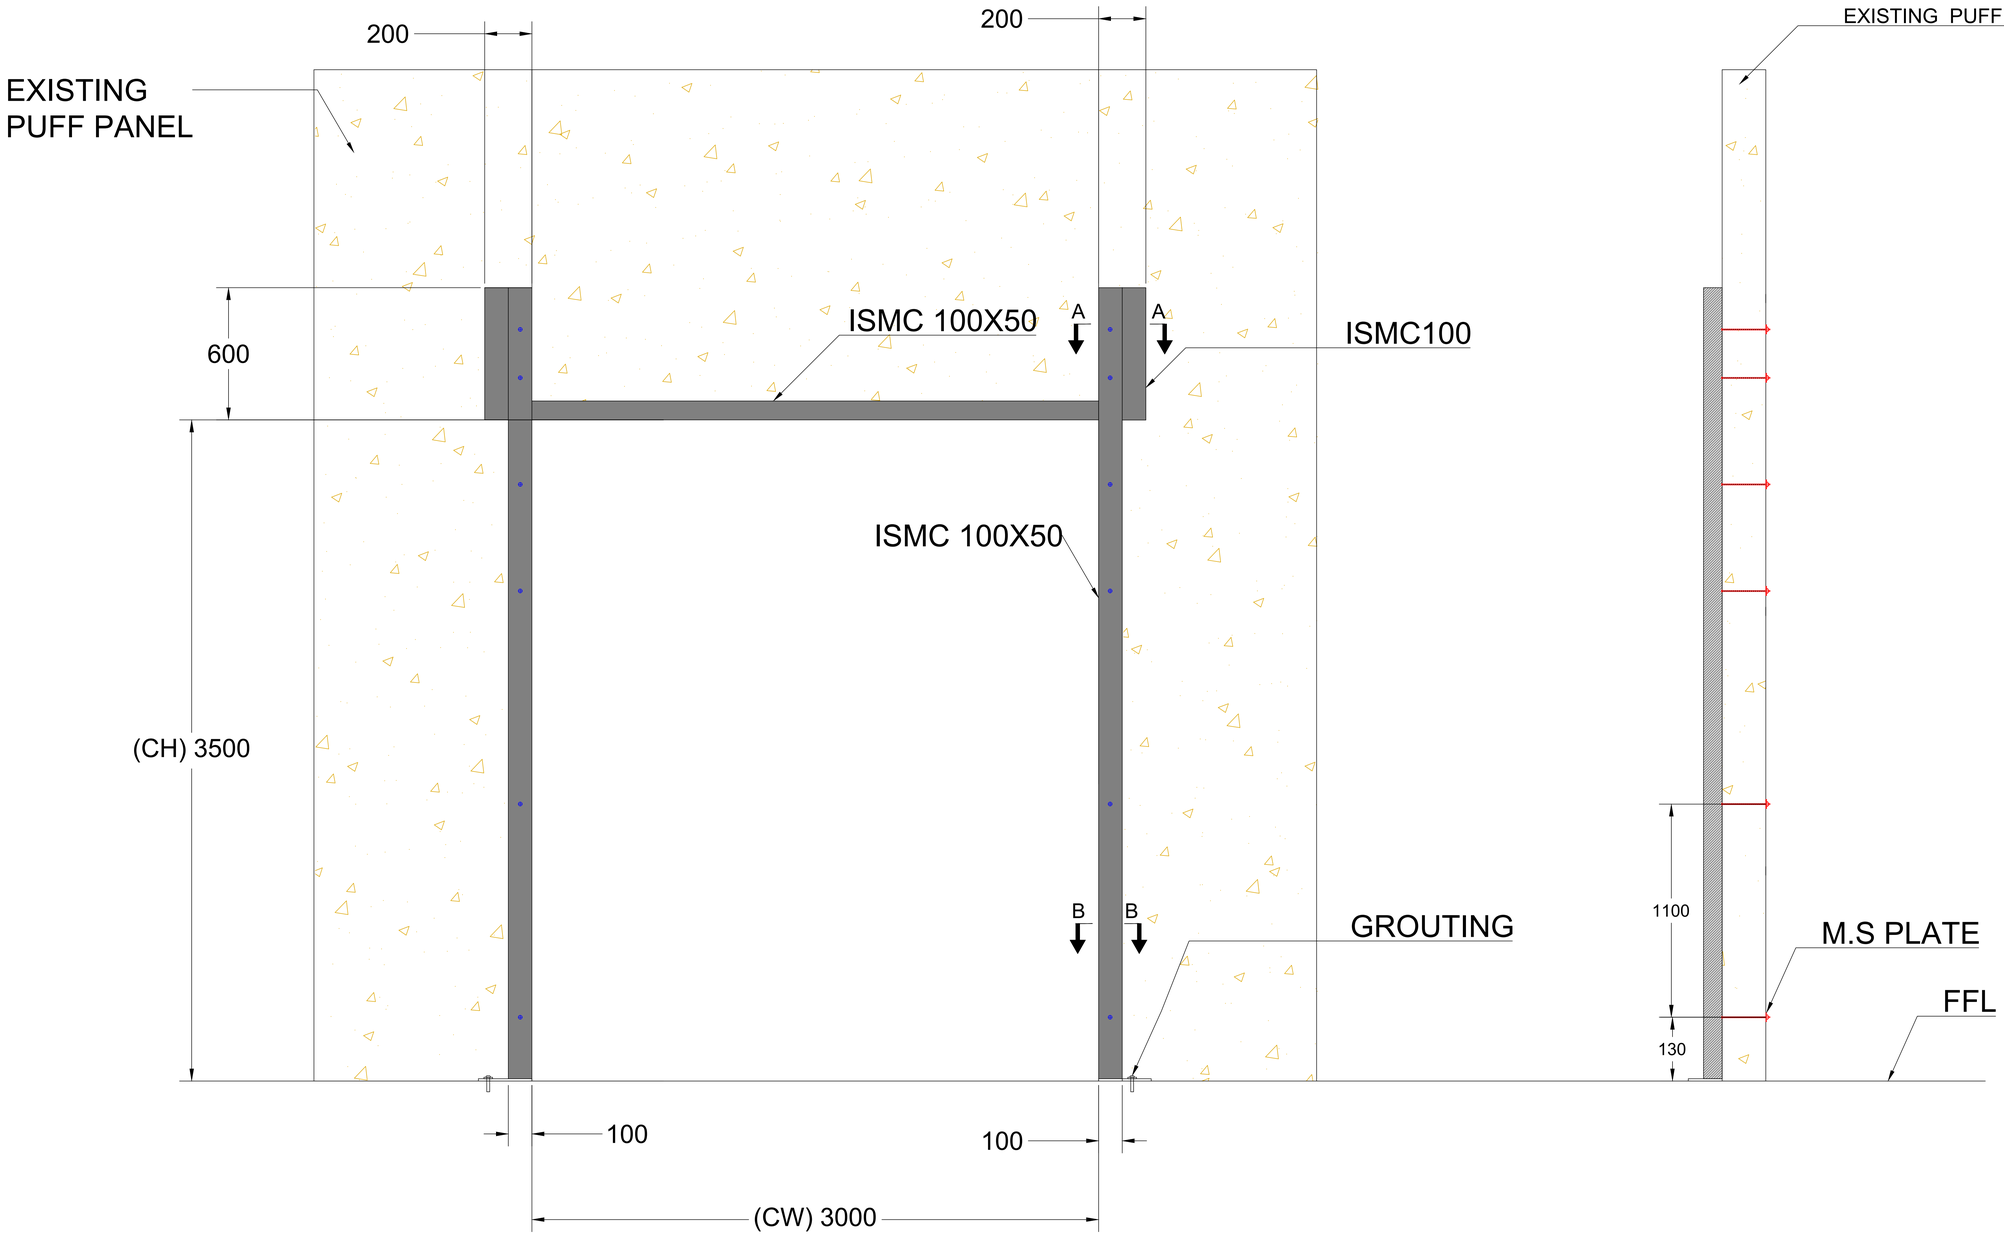

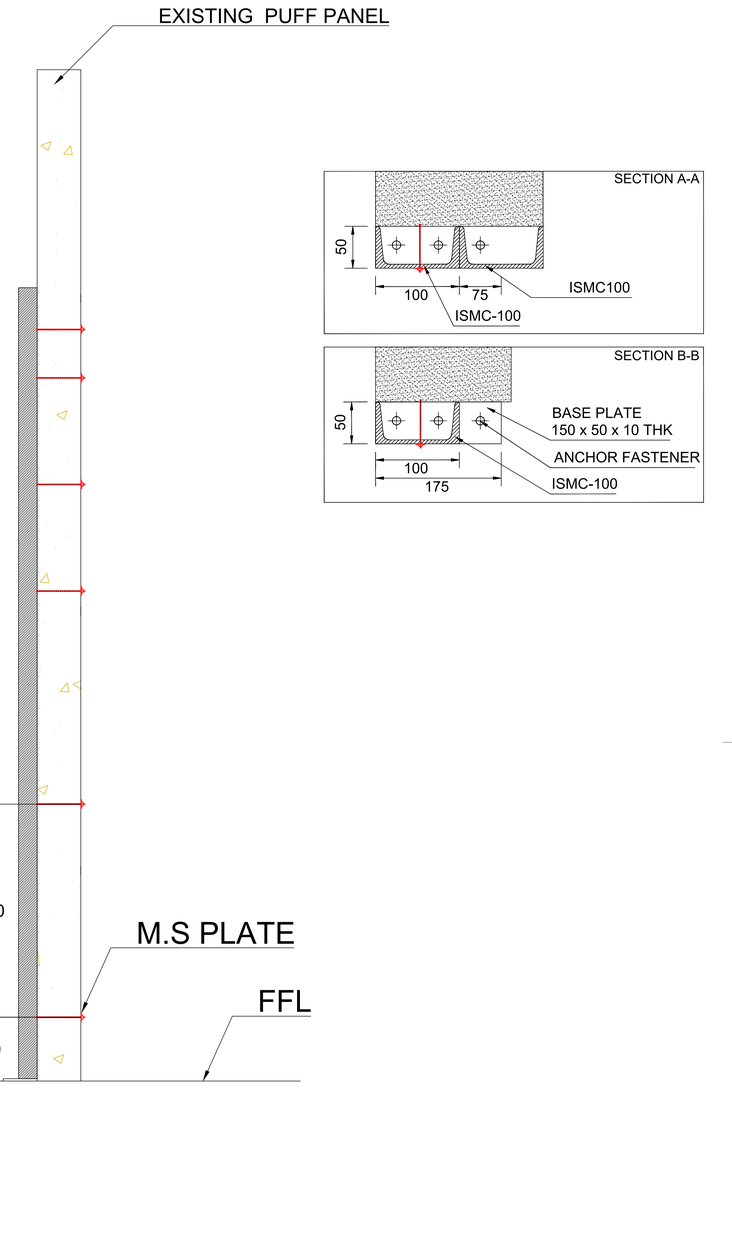

M.S. STRUCTURE DETAILS

SR.	CLEAR WIDTH	CLEAR HEIGHT	QTY.
01	3000	3500	01

This drawing & design is the property of NIHVA TECHNOLOGIES. Not to be sold or copied to any other concern.

TITLE SHUTTER ST.

NIHVA TECHNOLOGIES PVT. LTD.
NIHVA TECHNOLOGIES PVT. LTD. PUNE
Tel : 020 66304033
Email:- info@nihva.com
Website:- www.nihva.com

	NAME	SIGN	DATE
DRAWN	J.S		19.01.2024
CHECK	A.K		19.01.2024
APPRD.	V.T		19.01.2024

CLIENT - RINAC

PROJECT - ROLLING SHUTTER ST.


FORMAT NO - NIHVA-DD-F-03


If any queries contact : projectsupport@nihva.com

DWG. NO. : NIHVA/23-24/104 REV- R00


ALL DIMENSION ARE IN mm


SCALE: NTS WT: SHEET:

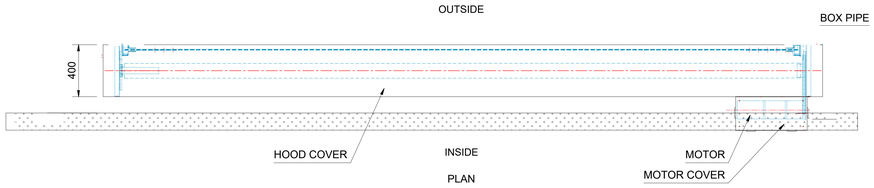

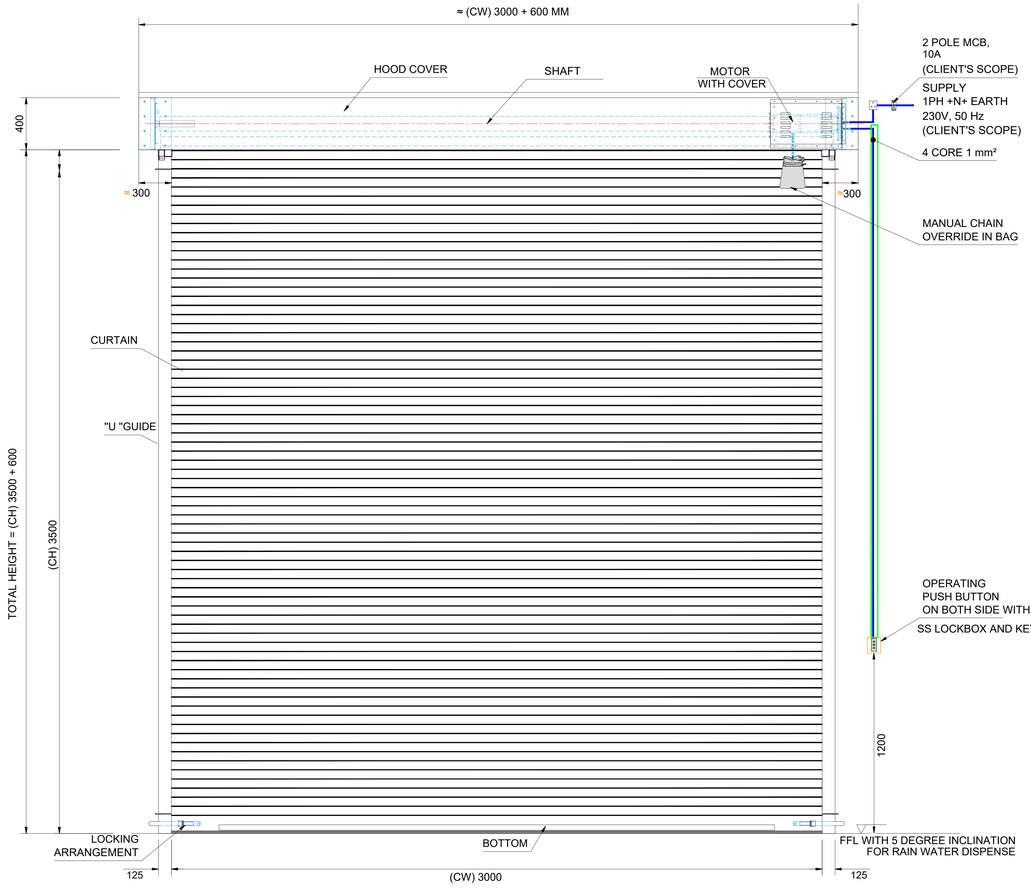

INSIDE ELEVATION

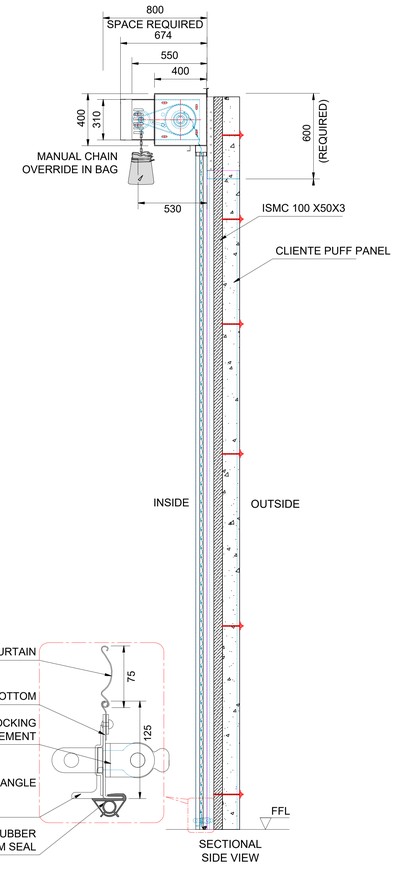

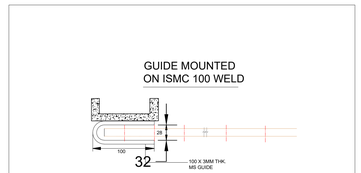

" U " TYPE GUIDE

☐	CAT - I	APPROVED - *No Further Comments*
☑	CAT - II	APPROVED - *Subjected to Incorporation of Comments as Marked.*
☐	CAT - III	NOT APPROVED *Resubmit with Incorporation of Comments as Marked / Discussed.*
☐	CAT - IV	INVALID SUBMISSION *Due to Non-Conformity of Tender specifications / drawings*

(Sign & Date)	(Name & Designation)	(Remarks)

COMMON COMMENTS :
1. CONTRACTOR NEEDS TO VERIFY THE DIMENSION OF THE OPENING ON SITE BEFORE PROCEEDING FOR EXECUTION
2. OPENING CONDITION OF THE ROLLING SHUTTER SHOULD BE AS PER THE PLAN
3. NO DEVIATION FROM TENDER SPECIFICATION WILL BE ALLOWED.
4. COLOR OF CURTAIN, BRACKET, SHAFT,SIDE GUIDES, BOTTOM PATTI, HOOD COVER PU SPRAY PAINTED SIMILAR TO RAL 9006 OVER 1COAT OF EPOXY PRIMER

TECHNICAL SPECIFICATION:-

SR.	SPECIFICATION	DETAILS
1.	Description & Drive	Motorised Rolling Shutter (Indirect Drive) with Manual Chain Arrangment
2.	Location Area	Inside / Outside
3.	Mounting Surface	Side Brackets: Optional / Structure
4.	Slat	Curved 75 mm PPGI Sheet - 1.0 mm Thk.
5.	Bottom Profile	MS Plate 125 x 2.5 mm thick with Angle Stiffner WITH RUBBER SEAL
6.	Guide Profile	M.S." U " Shape profile 100 x 2 mm Thk.
7.	Hood Cover & Motor Cover	Made of GI Sheet Thickness 0.9 mm
8.	Accessories	Push Button On Both Side

(1) All Cables & Ele.Conduits to be provided by RINAC
(2) All Civil Work in Client Scope

SHUTTER SIZES :-

SR.	CLEAR WIDTH	CLEAR HEIGHT	QTY.
01	3000	3500	06


This drawing & designing is the property of NIHVA TECHNOLOGIES. Not to be sold or copied to any other concern.


TITLE :-
MOTORISED ROLLING SHUTTER

NIHVA TECHNOLOGIES PVT. LTD. PUNE
Tel : 020 66304033
Email:- info@nihva.com
Website:- www.nihva.com

	NAME	DATE
DRAWN	J.S.	19/01/2024
CHECK	A.K.	19/01/2024
APPROVAL	V.T.	19/01/2024

CLIENT - RINAC
PROJECT -ROLLING SHUTTER
FORMAT NO - NIHVA-DD-F-03
DWG. NO. : NIHVA/23-24/107 REV-01
SCALE: NTS WT: SHEET: 01 OF 01
ALL DIMENSION ARE IN mm
If any queries contact : design@nihva.com

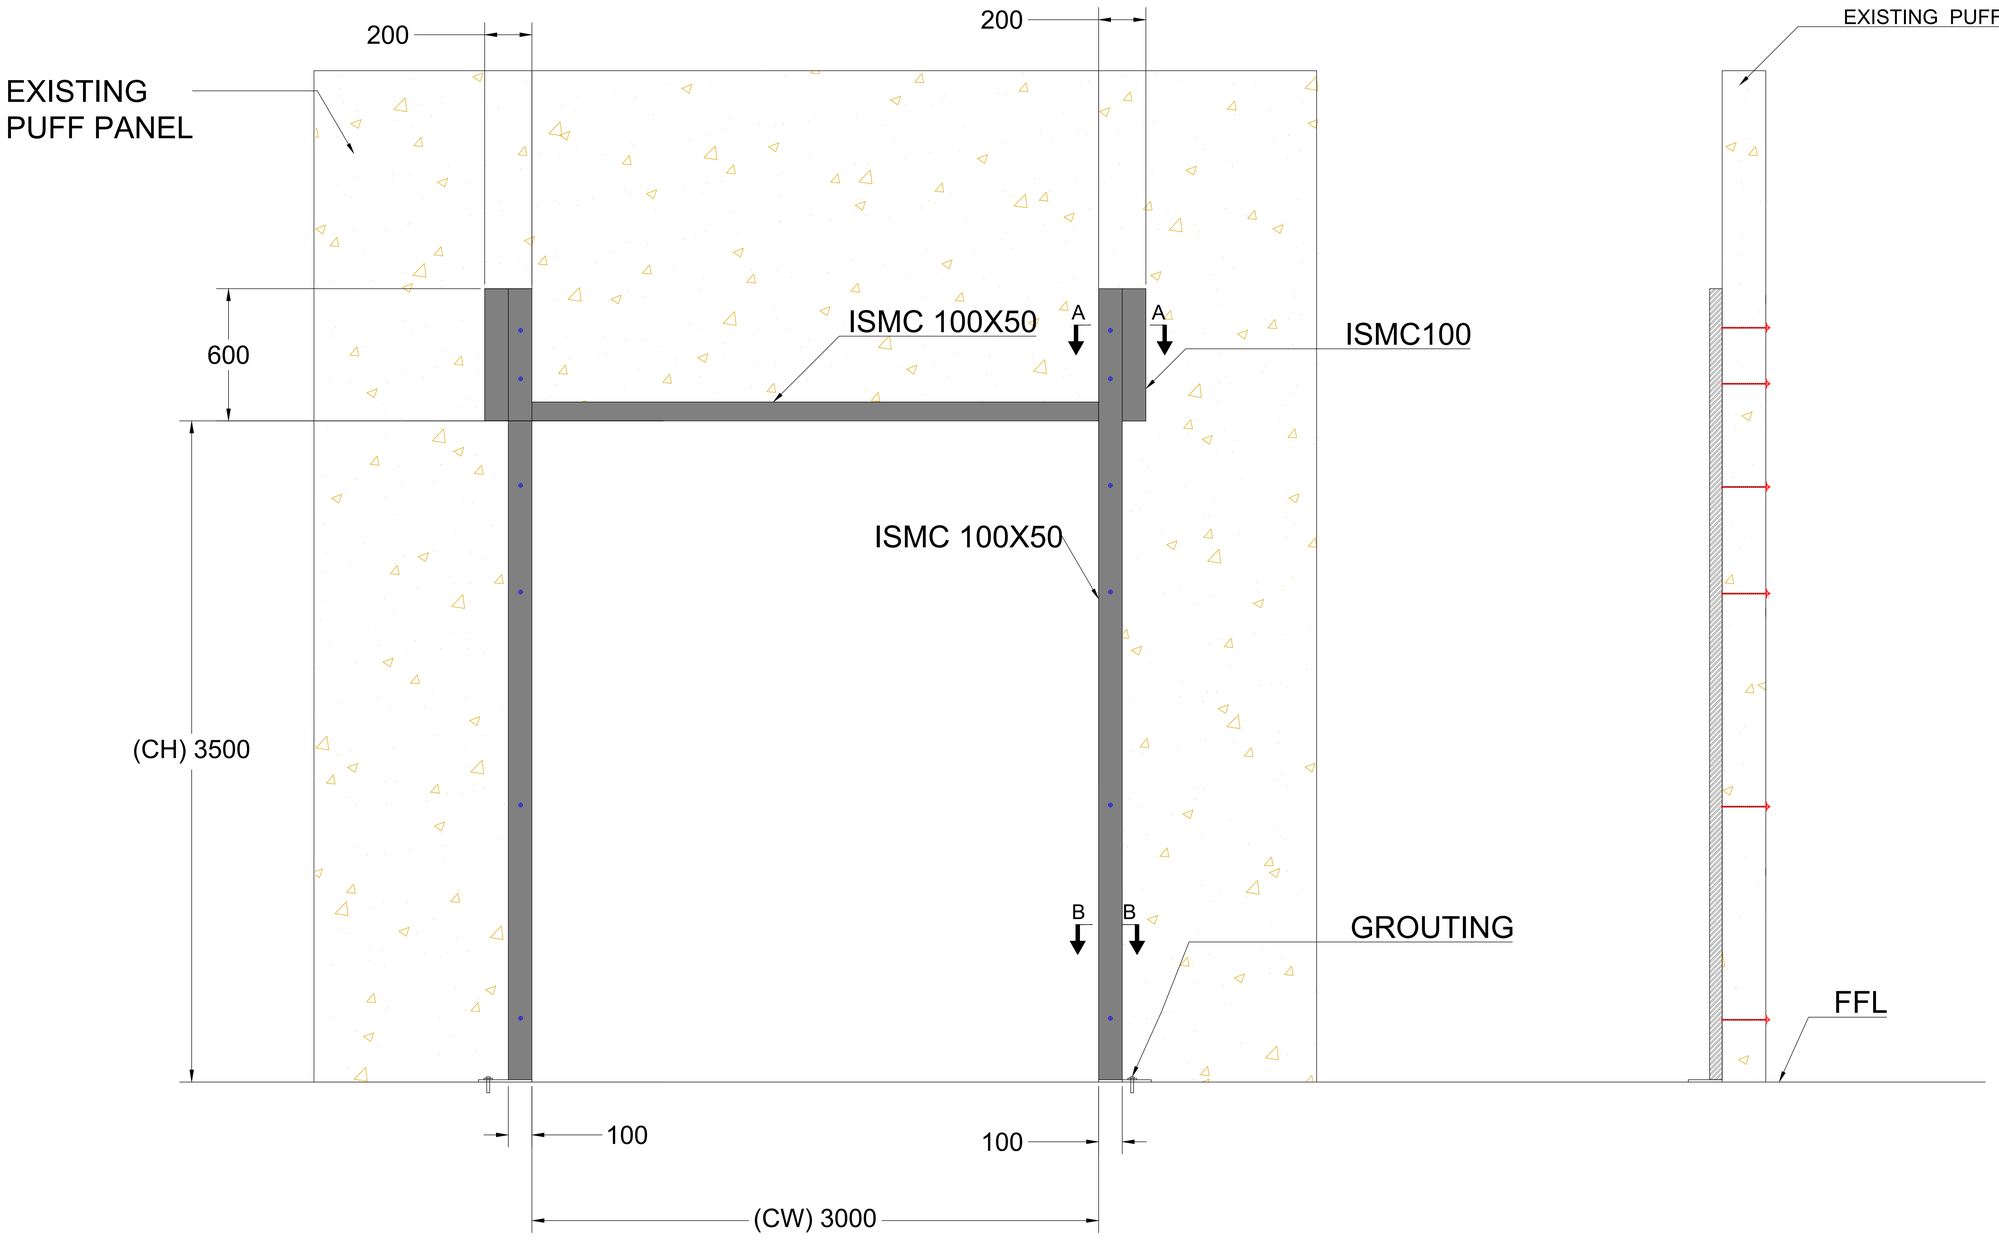

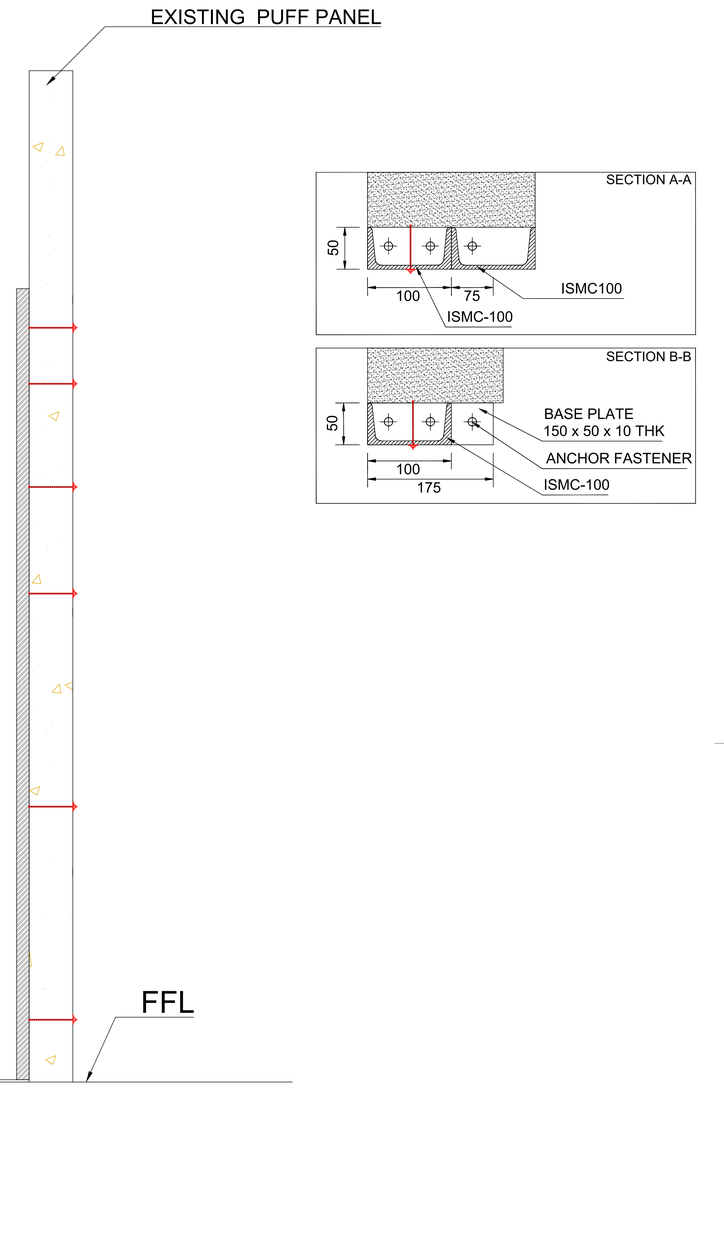



M.S. STRUCTURE DETAILS

SR.	CLEAR WIDTH	CLEAR HEIGHT	QTY.
01	3000	3500	06


This drawing & design is the property of NIHVA TECHNOLOGIES. Not to be sold or copied to any other concern.


TITLE	ROLLING SHUTTER ST.			NIHVA TECHNOLOGIES PVT. LTD. PUNE Tel : 020 66304033 Email:- info@nihva.com Website:- www.nihva.com	
	NAME	SIGN	DATE		
DRAWN	J.S		19.01.2024	CLIENT - RINAC	
CHECK	A.K		19.01.2024	PROJECT - ROLLING SHUTTER ST.	
APPRD.	V.T		19.01.2024	FORMAT NO - NIHVA-DD-F-03	
If any queries contact : projectsupport@nihva.com				DWG. NO. : NIHVA/23-24/108	REV- R00
ALL DIMENSION ARE IN mm				SCALE: NTS	WT: SHEET:

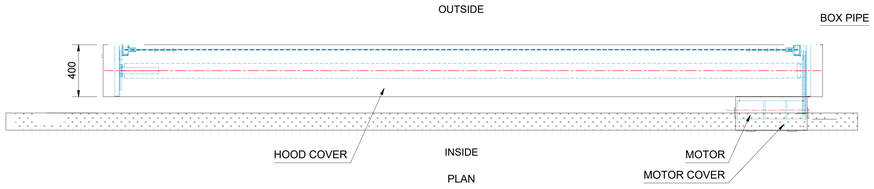


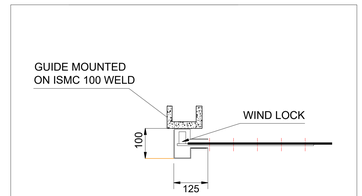

" T " TYPE GUIDE

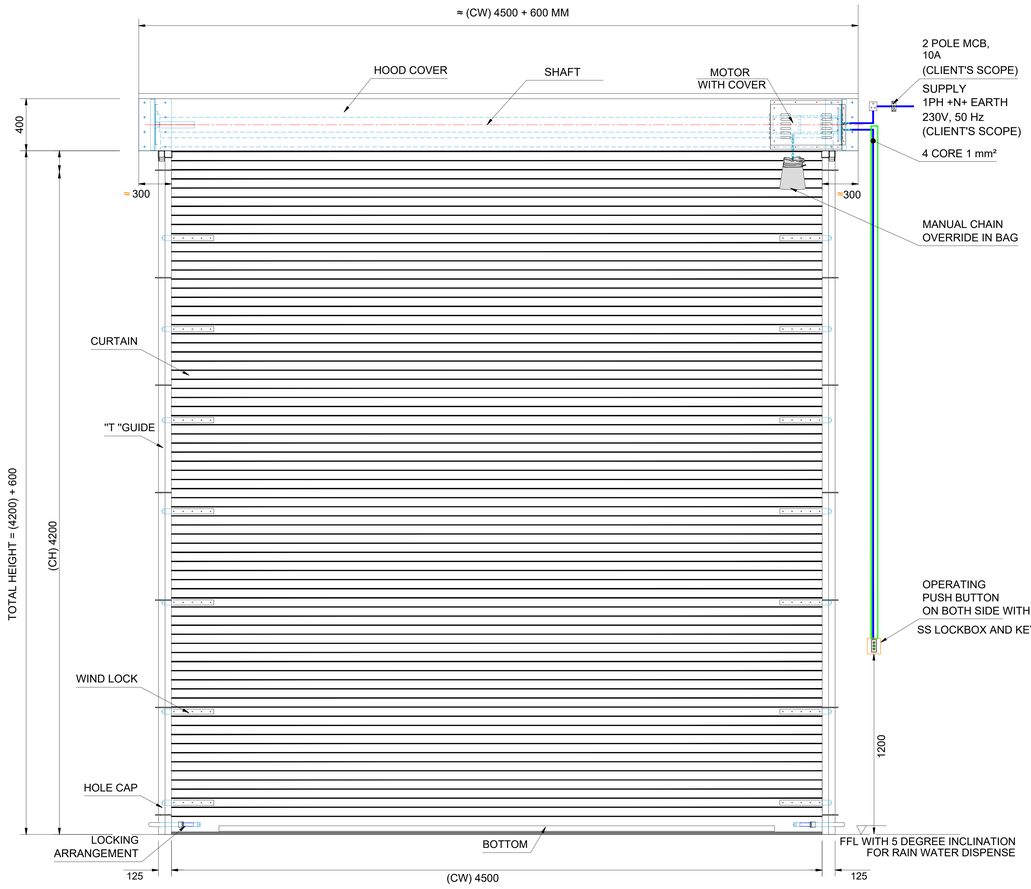

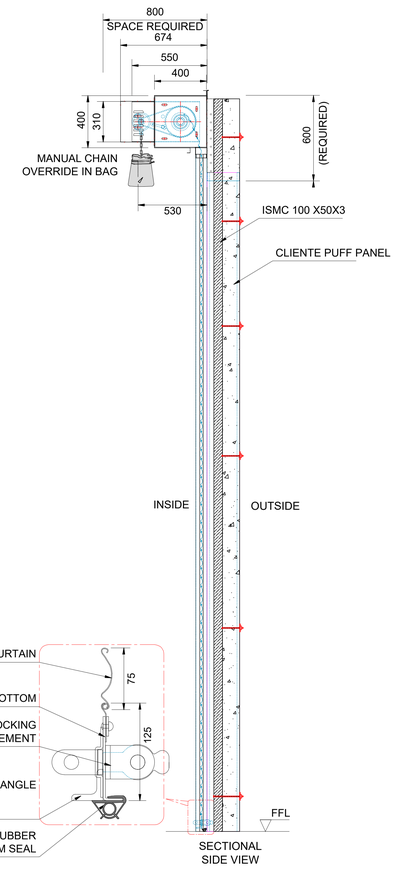

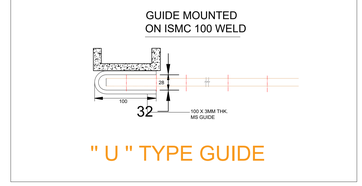

" U " TYPE GUIDE

CAT - I	APPROVED - *No Further Comments*
CAT - II	APPROVED - *Subjected to Incorporation of Comments as Marked.*
CAT - III	NOT APPROVED *Resubmit with Incorporation of Comments as Marked / Discussed.*
CAT - IV	INVALID SUBMISSION *Due to Non-Conformity of Tender specifications / drawings*

(Sign & Date)	(Name & Designation)	(Remarks)

COMMON COMMENTS :
1. CONTRACTOR NEEDS TO VERIFY THE DIMENSION OF THE OPENING ON SITE BEFORE PROCEEDING FOR EXECUTION
2. OPENING CONDITION OF THE ROLLING SHUTTER SHOULD BE AS PER THE PLAN
3. NO DEVIATION FROM TENDER SPECIFICATION WILL BE ALLOWED.
4. COLOR OF CURTAIN, BRACKET, SHAFT,SIDE GUIDES, BOTTOM PATTI, HOOD COVER PU SPRAY PAINTED SIMILAR TO RAL 9006 OVER 1COAT OF EPOXY PRIMER

INSIDE ELEVATION

TECHNICAL SPECIFICATION:-

SR.	SPECIFICATION	DETAILS
1.	Description & Drive	Motorised Rolling Shutter (Indirect Drive) with Manual Chain Arrangment
2.	Location Area	Inside / Outside
3.	Mounting Surface	Side Brackets: Optional / Structure
4.	Slat	Curved 75 mm PPGI Sheet - 1.0 mm Thk. & Windlock Considered
5.	Bottom Profile	MS Plate 125 x 2.5 mm thick with Angle Stiffner WITH RUBBER SEAL
6.	Guide Profile	M.S." T " Shape profile 125 x 3.15 mm Thk.
7.	Hood Cover & Motor Cover	Made of GI Sheet Thickness 0.9 mm
8.	Accessories	Push Button On Both Side

SHUTTER SIZES :-

SR.	CLEAR WIDTH	CLEAR HEIGHT	QTY.
01	4500	4200	01

(1) All Cables & Ele.Conduits to be provided by RINAC
(2) All Civil Work in Client Scope


This drawing & designing is the property of NIHVA TECHNOLOGIES. Not to be sold or copied to any other concern.


TITLE :-
MOTORISED ROLLING SHUTTER

NIHVA TECHNOLOGIES PVT. LTD.
NIHVA TECHNOLOGIES PVT. LTD. PUNE
Tel : 020 66304033
Email:- info@nihva.com
Website:- www.nihva.com

	NAME	DATE
DRAWN	J.S.	19/01/2024
CHECK	A.K.	19/01/2024
APPROVAL	V.T.	19/01/2024

CLIENT - RINAC
PROJECT -ROLLING SHUTTER
FORMAT NO - NIHVA-DD-F-03
DWG. NO. : NIHVA/23-24/109 REV-01
SCALE: NTS WT: SHEET: 01 OF 01
ALL DIMENSION ARE IN mm
If any queries contact : design@nihva.com

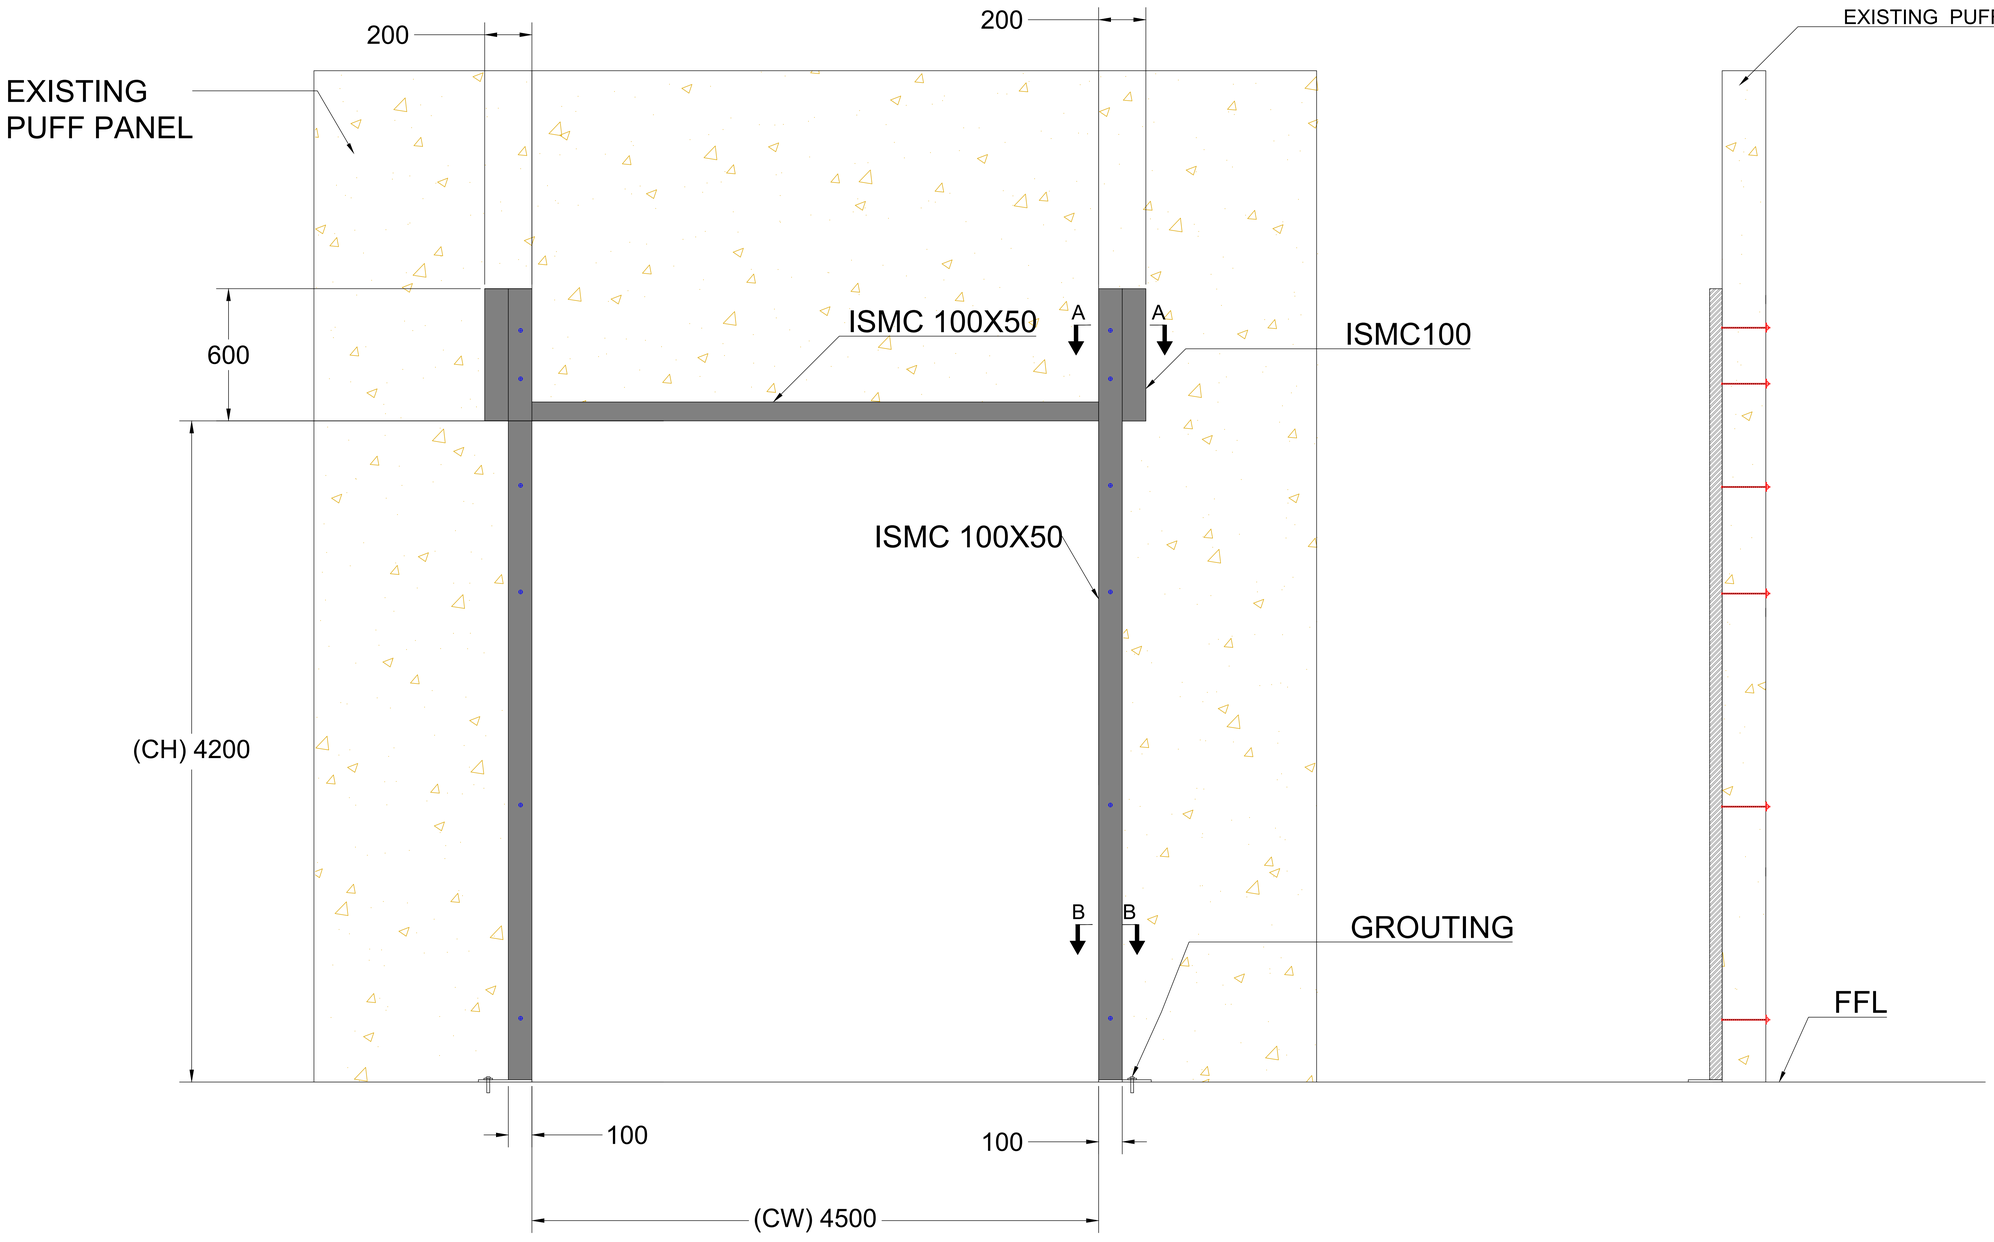

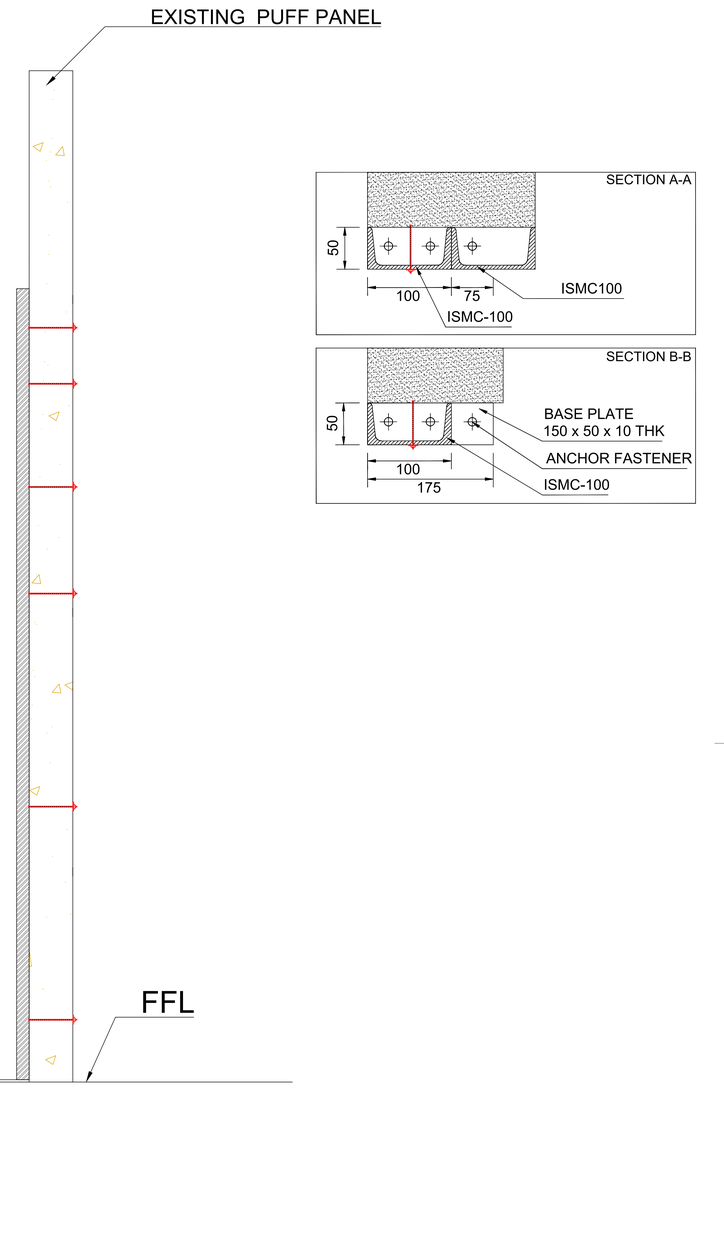


M.S. STRUCTURE DETAILS


SR.	CLEAR WIDTH	CLEAR HEIGHT	QTY.
01	4500	4200	01

This drawing & design is the property of NIHVA TECHNOLOGIES. Not to be sold or copied to any other concern.


TITLE	ROLLING SHUTTER ST.			NIHVA TECHNOLOGIES PVT. LTD. PUNE Tel : 020 66304033 Email:- info@nihva.com Website:- www.nihva.com	
	NAME	SIGN	DATE		
DRAWN	J.S		19.01.2024	CLIENT - RINAC	
CHECK	A.K		19.01.2024	PROJECT - ROLLING SHUTTER ST.	
APPRD.	V.T		19.01.2024	FORMAT NO - NIHVA-DD-F-03	
If any queries contact : projectsupport@nihva.com				DWG. NO. : NIHVA/23-24/110	REV- R00
ALL DIMENSION ARE IN mm				SCALE: NTS	WT: SHEET:

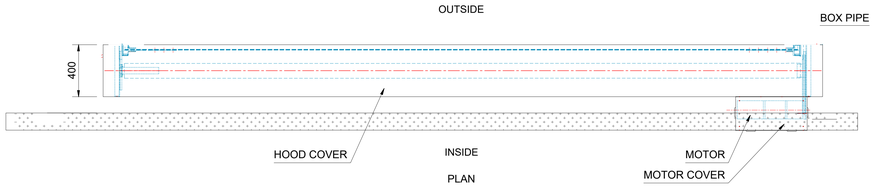


PLAN

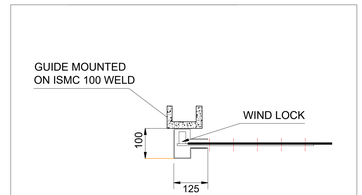

" T " TYPE GUIDE

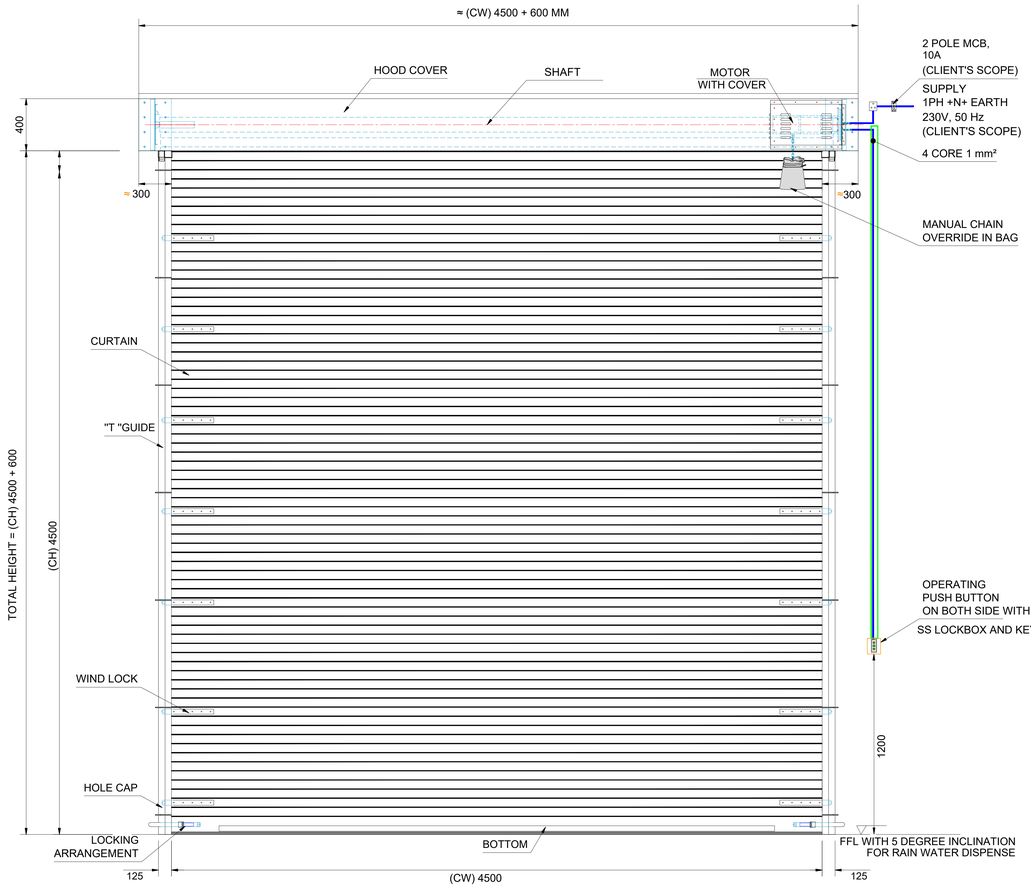

INSIDE ELEVATION

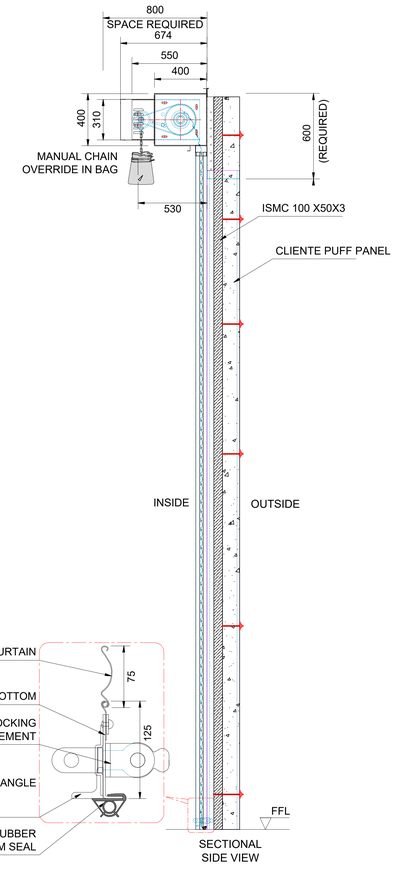

CAT - I	APPROVED - *No Further Comments*
CAT - II	APPROVED - *Subjected to Incorporation of Comments as Marked.*
CAT - III	NOT APPROVED *Resubmit with Incorporation of Comments as Marked / Discussed.*
CAT - IV	INVALID SUBMISSION *Due to Non-Conformity of Tender specifications / drawings*

(Sign & Date)	(Name & Designation)	(Remarks)

COMMON COMMENTS :
1. CONTRACTOR NEEDS TO VERIFY THE DIMENSION OF THE OPENING ON SITE BEFORE PROCEEDING FOR EXECUTION
2. OPENING CONDITION OF THE ROLLING SHUTTER SHOULD BE AS PER THE PLAN
3. NO DEVIATION FROM TENDER SPECIFICATION WILL BE ALLOWED.
4. COLOR OF CURTAIN, BRACKET, SHAFT,SIDE GUIDES, BOTTOM PATTI, HOOD COVER PU SPRAY PAINTED SIMILAR TO RAL 9006 OVER 1COAT OF EPOXY PRIMER

TECHNICAL SPECIFICATION:-

SR.	SPECIFICATION	DETAILS
1.	Description & Drive	Motorised Rolling Shutter (Indirect Drive) with Manual Chain Arrangment
2.	Location Area	Inside / Outside
3.	Mounting Surface	Side Brackets: Optional / Structure
4.	Slat	Curved 75 mm PPGI Sheet - 1.0 mm Thk. & Windlock Considered
5.	Bottom Profile	MS Plate 125 x 2.5 mm thick with Angle Stiffner WITH RUBBER SEAL
6.	Guide Profile	M.S." T " Shape profile 125 x 3.15 mm Thk.
7.	Hood Cover & Motor Cover	Made of GI Sheet Thickness 0.9 mm
8.	Accessories	Push Button On Both Side

(1) All Cables & Ele.Conduits to be provided by RINAC
(2) All Civil Work in Client Scope

SHUTTER SIZES :-

SR.	CLEAR WIDTH	CLEAR HEIGHT	QTY.
01	4500	4500	07


This drawing & designing is the property of NIHVA TECHNOLOGIES. Not to be sold or copied to any other concern.


TITLE :-
MOTORISED ROLLING SHUTTER

NIHVA TECHNOLOGIES PVT. LTD.
NIHVA TECHNOLOGIES PVT. LTD. PUNE
Tel : 020 66304033
Email:- info@nihva.com
Website:- www.nihva.com

	NAME	DATE
DRAWN	J.S.	19/01/2024
CHECK	A.K.	19/01/2024
APPROVAL	V.T.	19/01/2024

CLIENT - RINAC
PROJECT -ROLLING SHUTTER
FORMAT NO - NIHVA-DD-F-03
DWG. NO. : NIHVA/23-24/105 REV-01
SCALE: NTS WT: SHEET: 01 OF 01
ALL DIMENSION ARE IN mm
If any queries contact : design@nihva.com

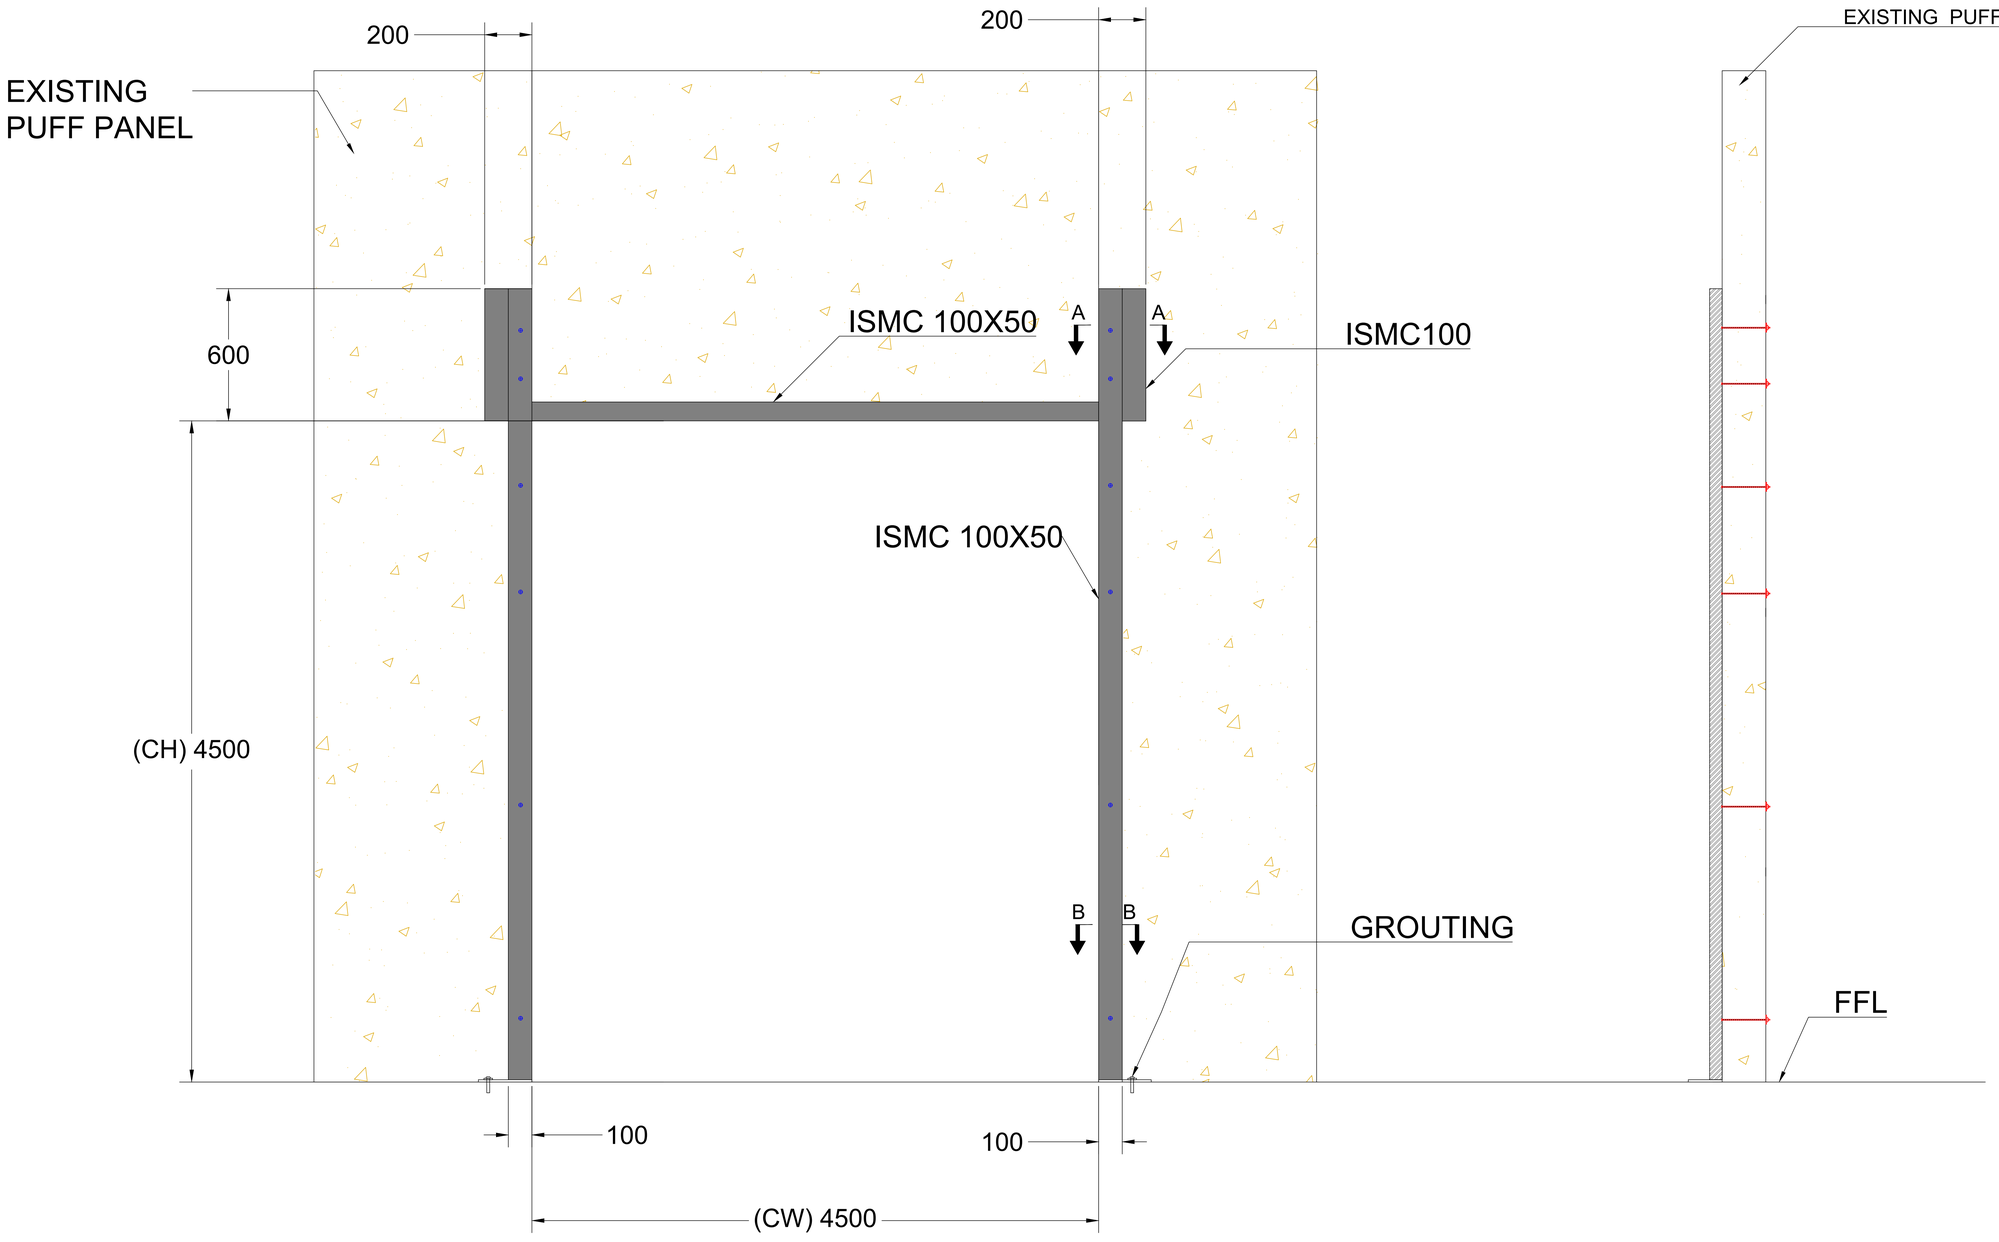

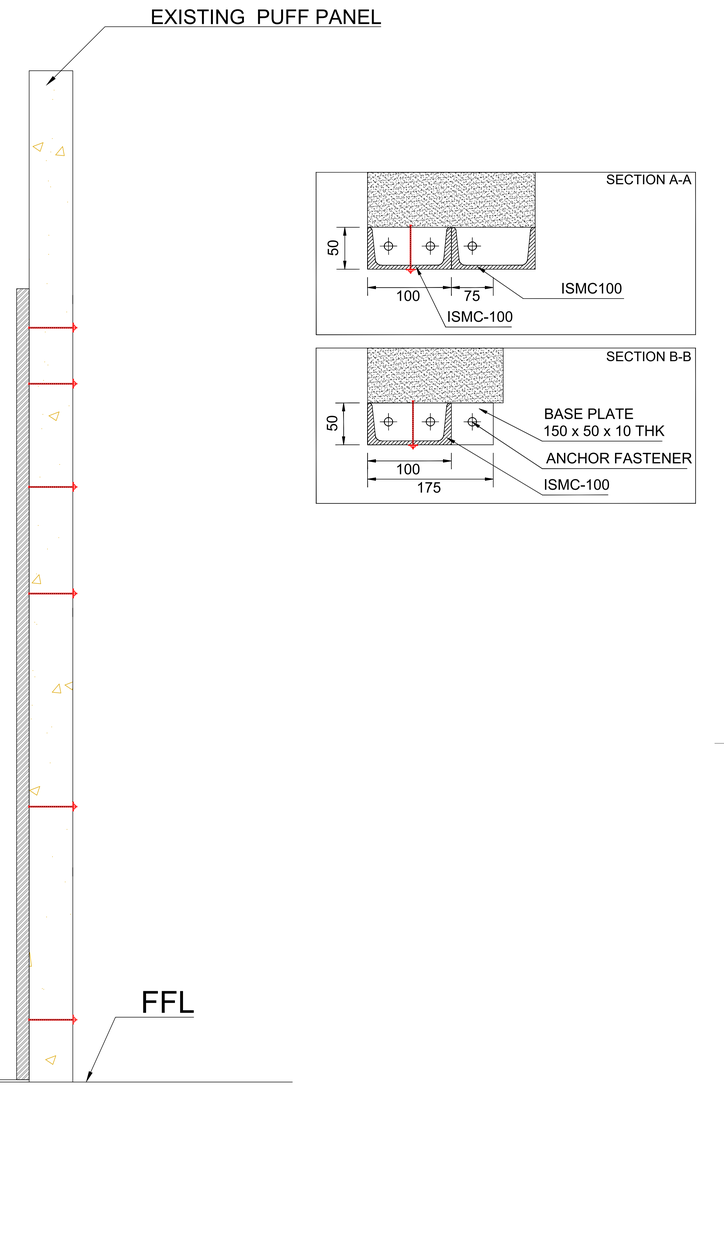


M.S. STRUCTURE DETAILS


SR.	CLEAR WIDTH	CLEAR HEIGHT	QTY.
01	4500	4500	07

This drawing & design is the property of NIHVA TECHNOLOGIES. Not to be sold or copied to any other concern.


TITLE	ROLLING SHUTTER ST.			NIHVA TECHNOLOGIES PVT. LTD. PUNE Tel : 020 66304033 Email:- info@nihva.com Website:- www.nihva.com	
	NAME	SIGN	DATE		
DRAWN	J.S		19.01.2024	CLIENT - RINAC	
CHECK	A.K		19.01.2024	PROJECT - ROLLING SHUTTER ST.	
APPRD.	V.T		19.01.2024	FORMAT NO - NIHVA-DD-F-03	
If any queries contact : projectsupport@nihva.com				DWG. NO. : NIHVA/23-24/106	REV- R00
ALL DIMENSION ARE IN mm				SCALE: NTS	WT: SHEET:

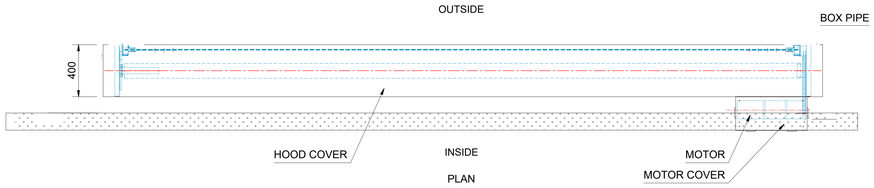


PLAN

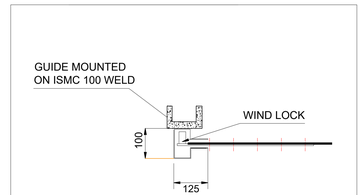

" T " TYPE GUIDE

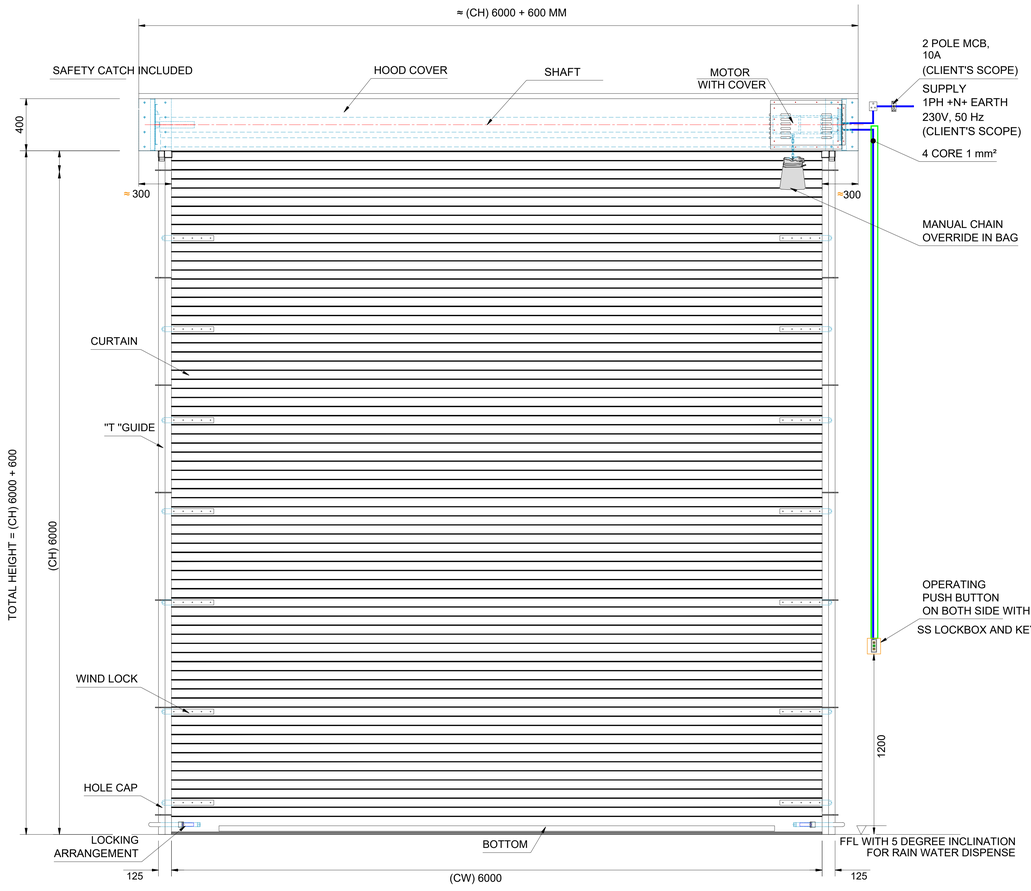

INSIDE ELEVATION

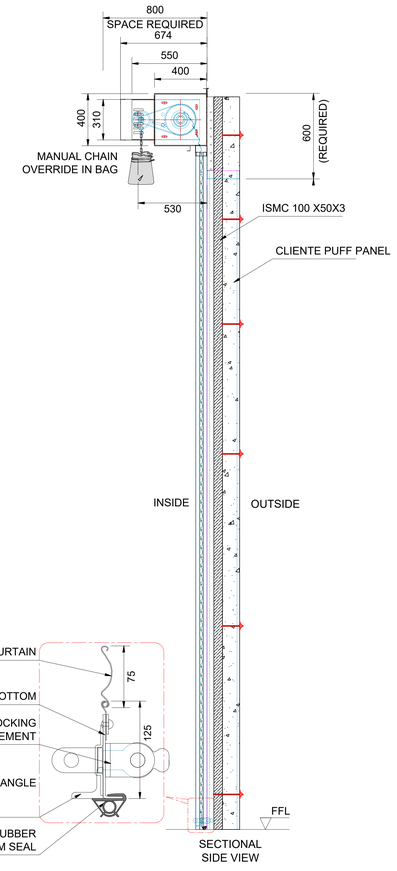

CAT - I	APPROVED - *No Further Comments*
CAT - II	APPROVED - *Subjected to Incorporation of Comments as Marked.*
CAT - III	NOT APPROVED *Resubmit with Incorporation of Comments as Marked / Discussed.*
CAT - IV	INVALID SUBMISSION *Due to Non-Conformity of Tender specifications / drawings*

(Sign & Date)	(Name & Designation)	(Remarks)

COMMON COMMENTS :
1. CONTRACTOR NEEDS TO VERIFY THE DIMENSION OF THE OPENING ON SITE BEFORE PROCEEDING FOR EXECUTION
2. OPENING CONDITION OF THE ROLLING SHUTTER SHOULD BE AS PER THE PLAN
3. NO DEVIATION FROM TENDER SPECIFICATION WILL BE ALLOWED.
4. COLOR OF CURTAIN, BRACKET, SHAFT,SIDE GUIDES, BOTTOM PATTI, HOOD COVER PU SPRAY PAINTED SIMILAR TO RAL 9006 OVER 1COAT OF EPOXY PRIMER

TECHNICAL SPECIFICATION:-

SR.	SPECIFICATION	DETAILS
1.	Description & Drive	Motorised Rolling Shutter (Indirect Drive) with Manual Chain Arrangment
2.	Location Area	Inside / Outside
3.	Mounting Surface	Side Brackets: Optional / Structure
4.	Slat	Curved 75 mm PPGI Sheet - 1.0 mm Thk. & Windlock Considered
5.	Bottom Profile	MS Plate 125 x 2.5 mm thick with Angle Stiffner With Rubber Seal
6.	Guide Profile	M.S." T " Shape profile 125 x 3.15 mm Thk.
7.	Hood Cover & Motor Cover	Made of GI Sheet Thickness 0.9 mm
8.	Accessories	Safety Catch,Push Button On Both SIde

SHUTTER SIZES :-

SR.	CLEAR WIDTH	CLEAR HEIGHT	QTY.
01	6000	6000	02

NOTE :-
(1) All Cables & Ele.Conduits to be provided by RINAC
(2) All Civil Work in Client Scope


This drawing & designing is the property of NIHVA TECHNOLOGIES. Not to be sold or copied to any other concern.


TITLE :-
MOTORISED ROLLING SHUTTER

NIHVA TECHNOLOGIES PVT. LTD.
NIHVA TECHNOLOGIES PVT. LTD. PUNE
Tel : 020 66304033
Email:- info@nihva.com
Website:- www.nihva.com

	NAME	DATE
DRAWN	J.S.	19/01/2024
CHECK	A.K.	19/01/2024
APPROVAL	V.T.	19/01/2024

CLIENT - RINAC
PROJECT -ROLLING SHUTTER
FORMAT NO - NIHVA-DD-F-03
DWG. NO. :NIHVA/23-24/103 REV-01
SCALE: NTS WT: SHEET: 01 OF 01
ALL DIMENSION ARE IN mm
If any queries contact : design@nihva.com

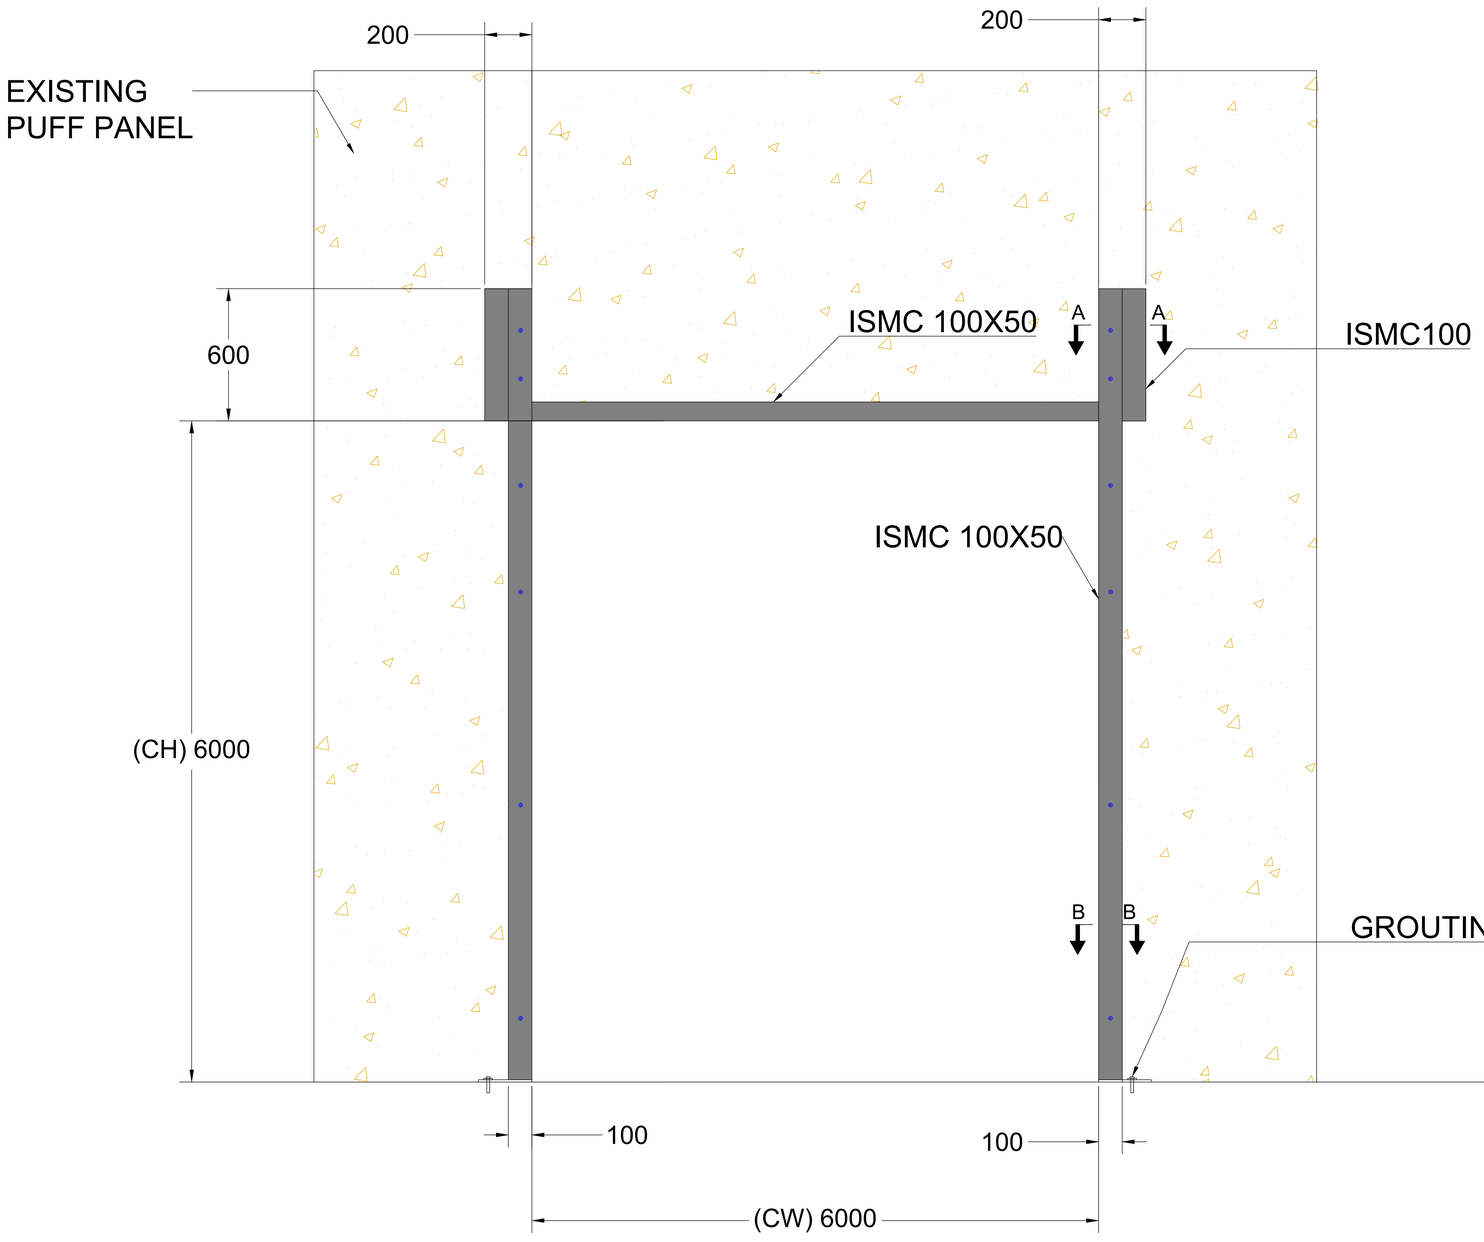

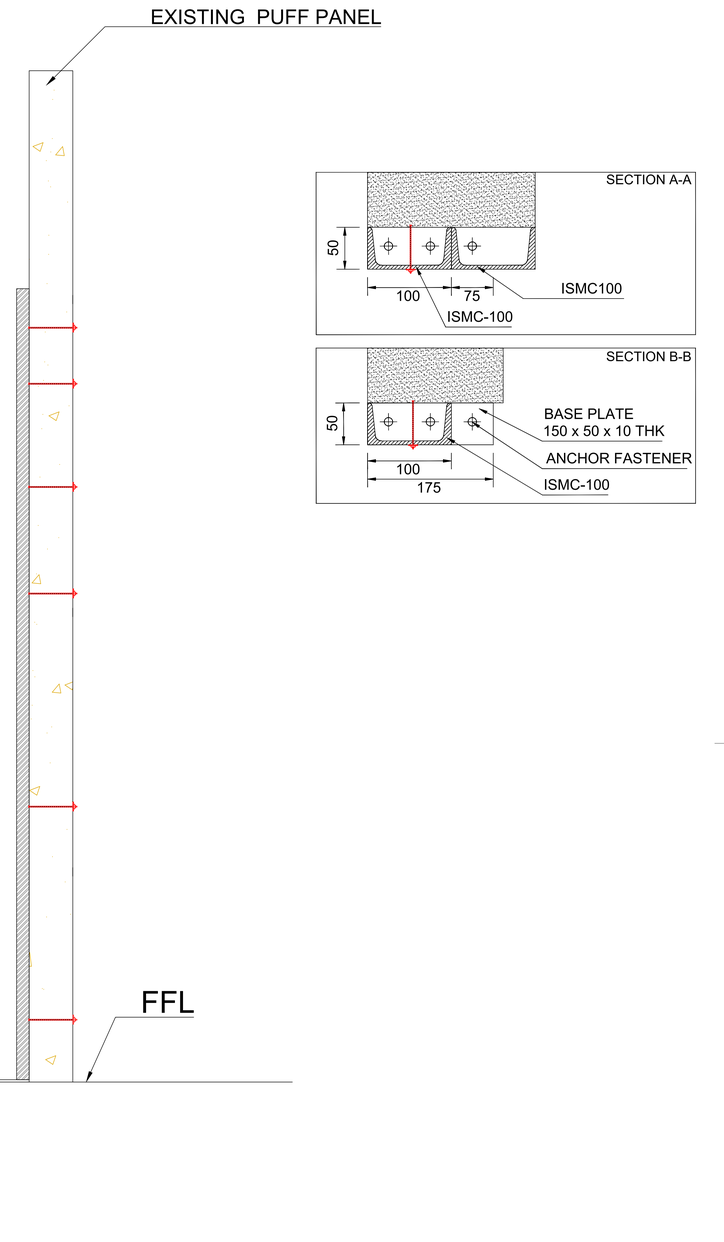


M.S. STRUCTURE DETAILS


SR.	CLEAR WIDTH	CLEAR HEIGHT	QTY.
01	6000	6000	02

This drawing & design is the property of NIHVA TECHNOLOGIES. Not to be sold or copied to any other concern.


TITLE	ROLLING SHUTTER ST.			NIHVA TECHNOLOGIES PVT. LTD. PUNE Tel : 020 66304033 Email:- info@nihva.com Website:- www.nihva.com	
	NAME	SIGN	DATE		
DRAWN	J.S		19.01.2024	CLIENT - RINAC	
CHECK	A.K		19.01.2024	PROJECT - ROLLING SHUTTER ST.	
APPRD.	V.T		19.01.2024	FORMAT NO - NIHVA-DD-F-03	
If any queries contact : projectsupport@nihva.com				DWG. NO. : NIHVA/23-24/104	REV- R00
ALL DIMENSION ARE IN mm				SCALE: NTS	WT: SHEET:

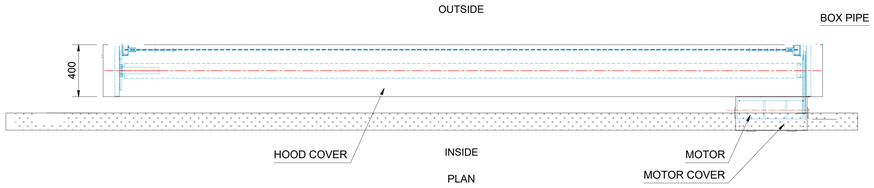


PLAN

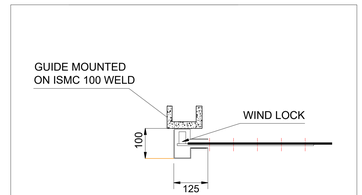

" T " TYPE GUIDE

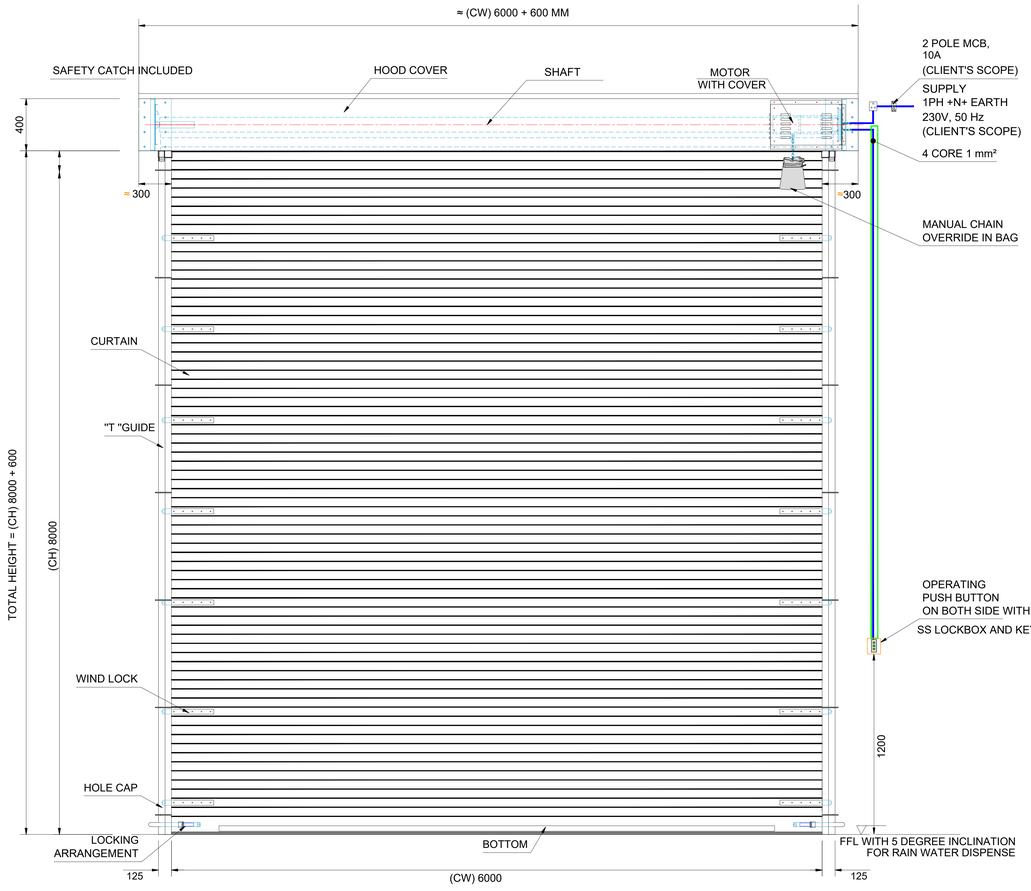

INSIDE ELEVATION

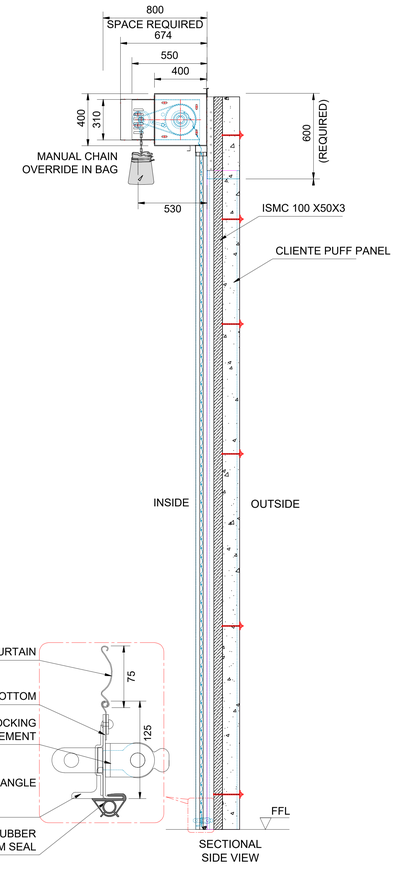

CAT - I	APPROVED - *No Further Comments*
CAT - II	APPROVED - *Subjected to Incorporation of Comments as Marked.*
CAT - III	NOT APPROVED *Resubmit with Incorporation of Comments as Marked / Discussed.*
CAT - IV	INVALID SUBMISSION *Due to Non-Conformity of Tender specifications / drawings*

(Sign & Date)	(Name & Designation)	(Remarks)

COMMON COMMENTS :
1. CONTRACTOR NEEDS TO VERIFY THE DIMENSION OF THE OPENING ON SITE BEFORE PROCEEDING FOR EXECUTION
2. OPENING CONDITION OF THE ROLLING SHUTTER SHOULD BE AS PER THE PLAN
3. NO DEVIATION FROM TENDER SPECIFICATION WILL BE ALLOWED.
4. COLOR OF CURTAIN, BRACKET, SHAFT,SIDE GUIDES, BOTTOM PATTI, HOOD COVER PU SPRAY PAINTED SIMILAR TO RAL 9006 OVER 1COAT OF EPOXY PRIMER

TECHNICAL SPECIFICATION:-

SR.	SPECIFICATION	DETAILS
1.	Description & Drive	Motorised Rolling Shutter (Indirect Drive) with Manual Chain Arrangment
2.	Location Area	Inside / Outside
3.	Mounting Surface	Side Brackets: Optional / Structure
4.	Slat	Curved 75 mm PPGI Sheet - 1.0 mm Thk. & Windlock Considered
5.	Bottom Profile	MS Plate 125 x 2.5 mm thick with Angle Stiffner WITH RUBBER SEAL
6.	Guide Profile	M.S." T " Shape profile 125 x 3.15 mm Thk.
7.	Hood Cover & Motor Cover	Made of GI Sheet Thickness 0.9 mm
8.	Accessories	Safety Catch,Push Button On Both SIde

(1) All Cables & Ele.Conduits to be provided by RINAC
(2) All Civil Work in Client Scope

SHUTTER SIZES :-

SR.	CLEAR WIDTH	CLEAR HEIGHT	QTY.
01	6000	8000	01


This drawing & designing is the property of NIHVA TECHNOLOGIES. Not to be sold or copied to any other concern.


TITLE :-
MOTORISED ROLLING SHUTTER

NIHVA TECHNOLOGIES PVT. LTD.
NIHVA TECHNOLOGIES PVT. LTD. PUNE
Tel : 020 66304033
Email:- info@nihva.com
Website:- www.nihva.com

	NAME	DATE
DRAWN	J.S.	19/01/2024
CHECK	A.K.	19/01/2024
APPROVAL	V.T.	19/01/2024

CLIENT - RINAC
PROJECT -ROLLING SHUTTER
FORMAT NO - NIHVA-DD-F-03
DWG. NO. : NIHVA/23-24/101 REV-01
SCALE: NTS WT: SHEET: 01 OF 01
ALL DIMENSION ARE IN mm
If any queries contact : design@nihva.com

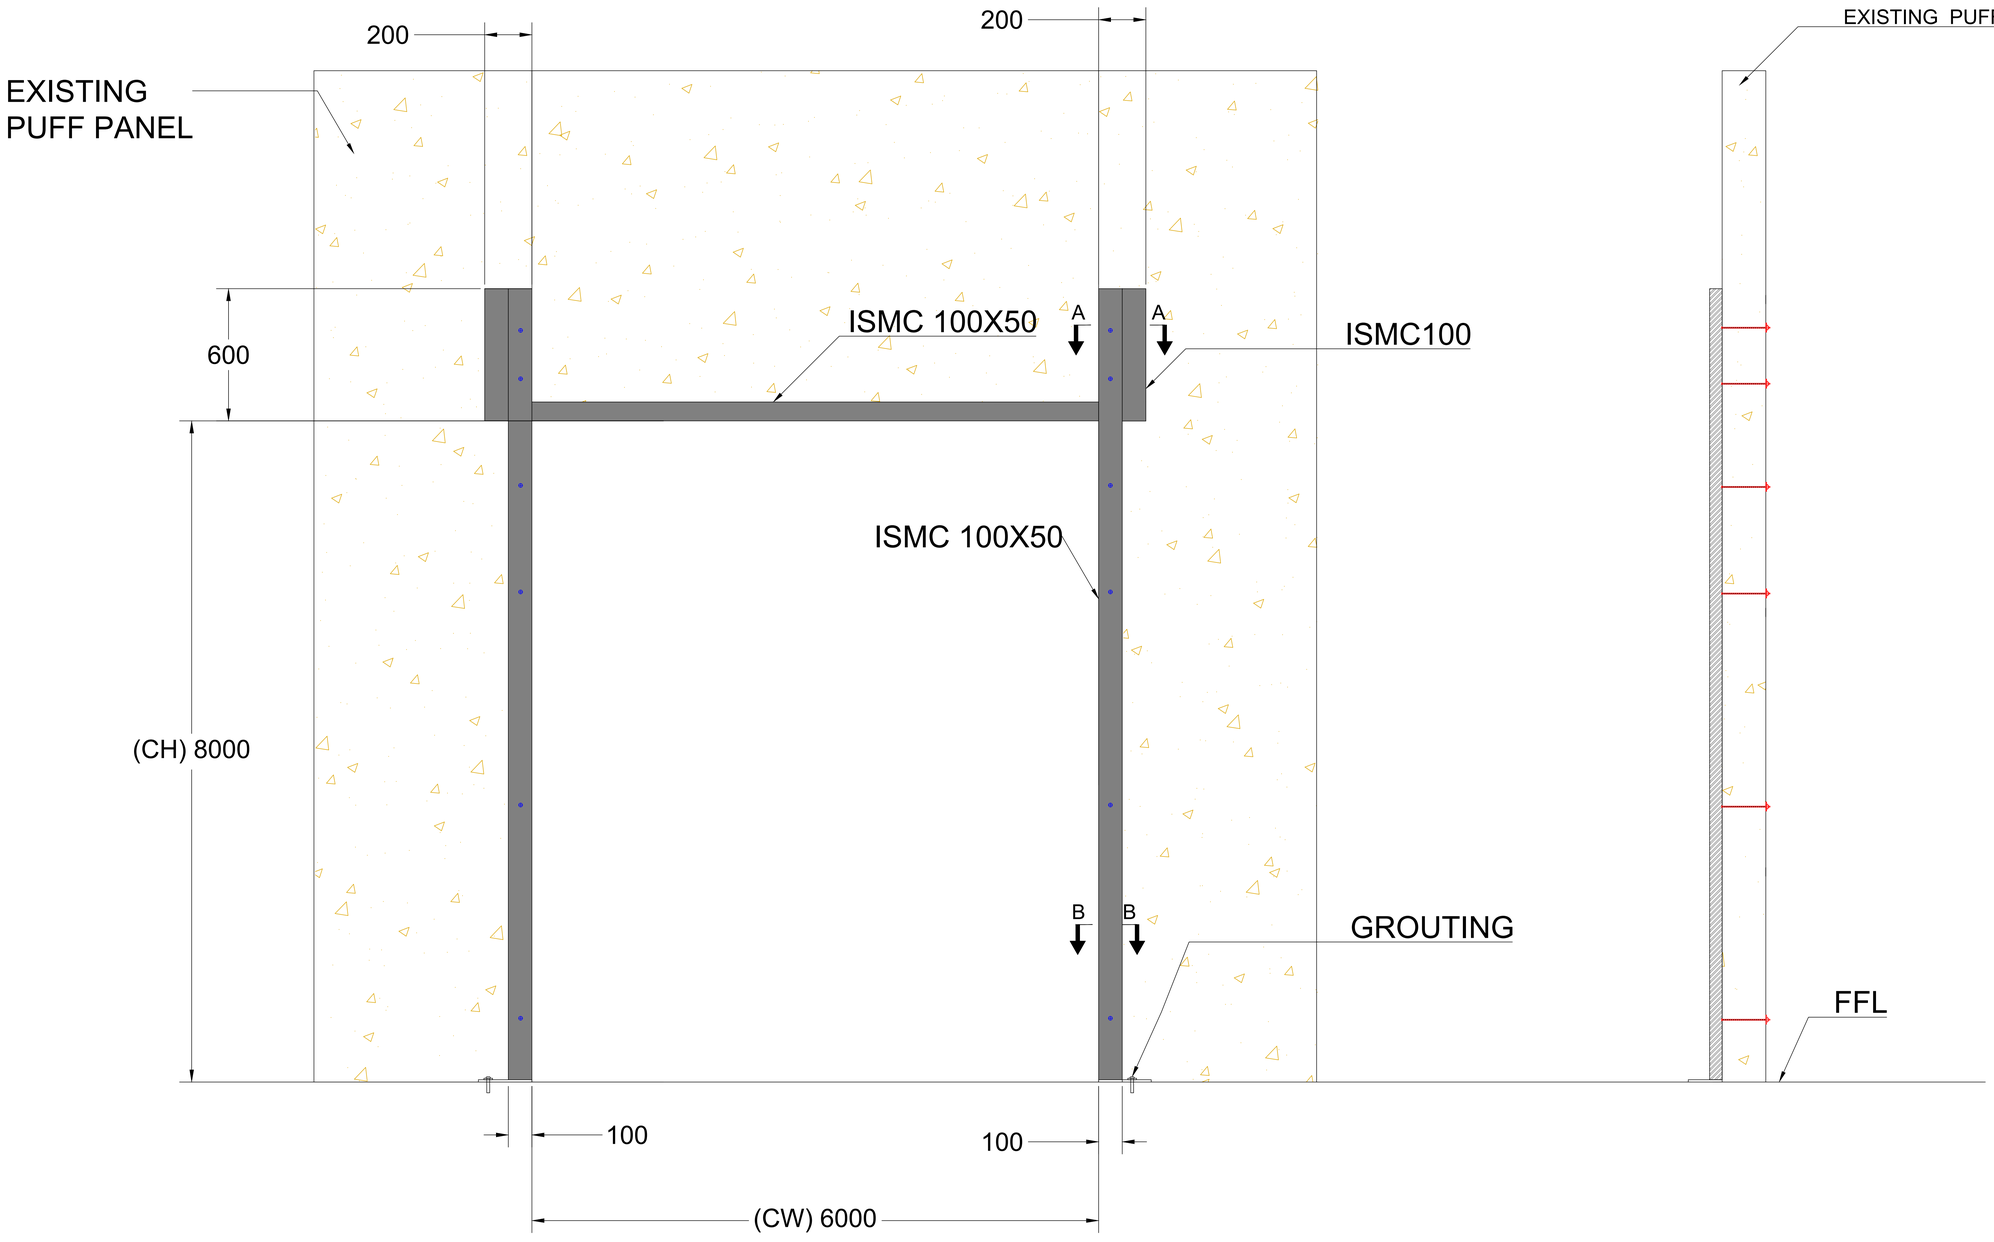

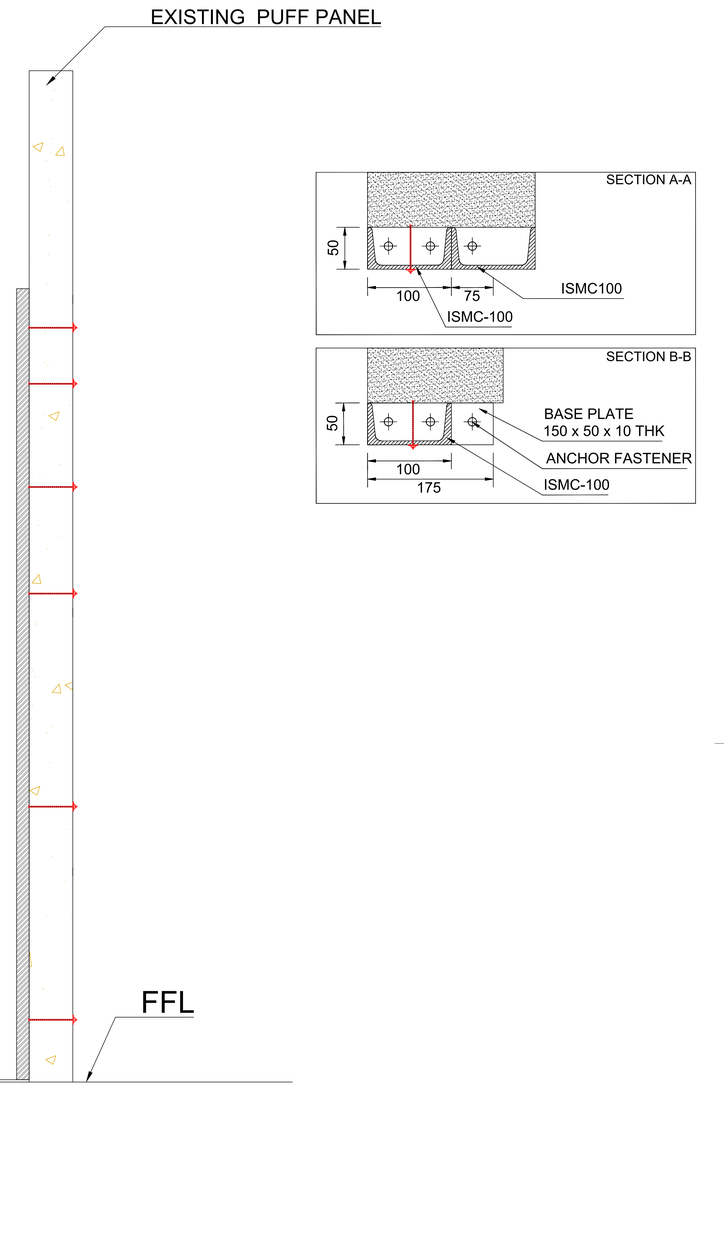

M.S. STRUCTURE DETAILS

SR.	CLEAR WIDTH	CLEAR HEIGHT	QTY.
01	6000	8000	01

This drawing & design is the property of NIHVA TECHNOLOGIES. Not to be sold or copied to any other concern.

TITLE	ROLLING SHUTTER ST.			NIHVA TECHNOLOGIES PVT. LTD. PUNE Tel : 020 66304033 Email:- info@nihva.com Website:- www.nihva.com	
	NAME	SIGN	DATE		
DRAWN	J.S		19.01.2024	CLIENT - RINAC	
CHECK	A.K		19.01.2024	PROJECT - ROLLING SHUTTER ST.	
APPRD.	V.T		19.01.2024	FORMAT NO - NIHVA-DD-F-03	
If any queries contact : projectsupport@nihva.com				DWG. NO. : NIHVA/23-24/102	REV- R00
ALL DIMENSION ARE IN mm				SCALE: NTS	WT: SHEET: