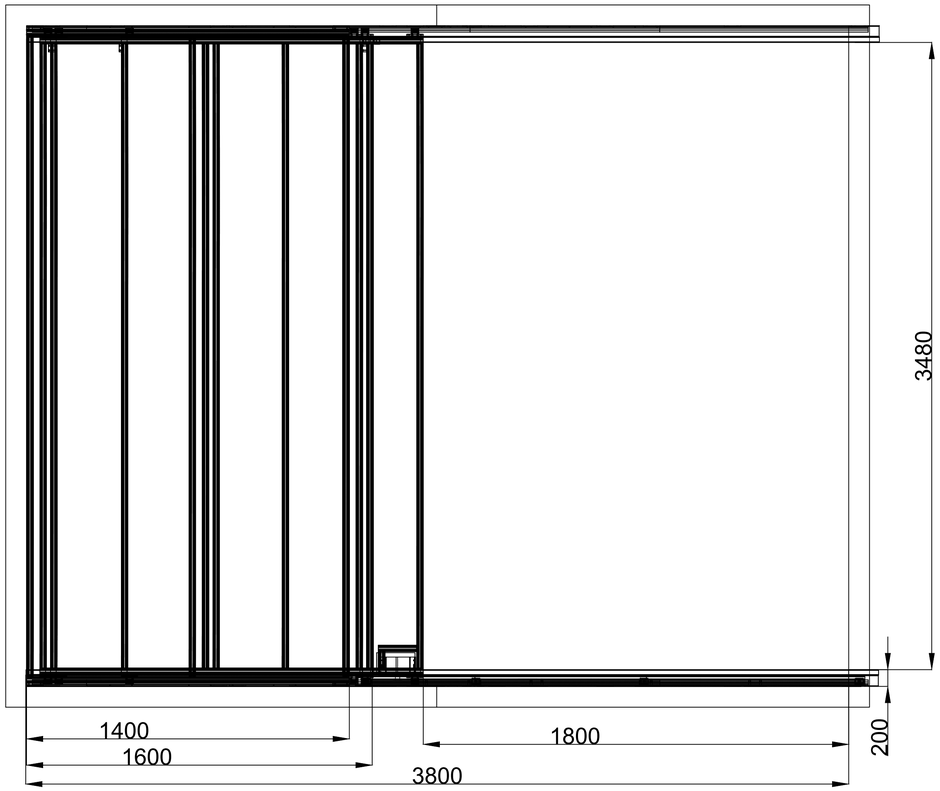

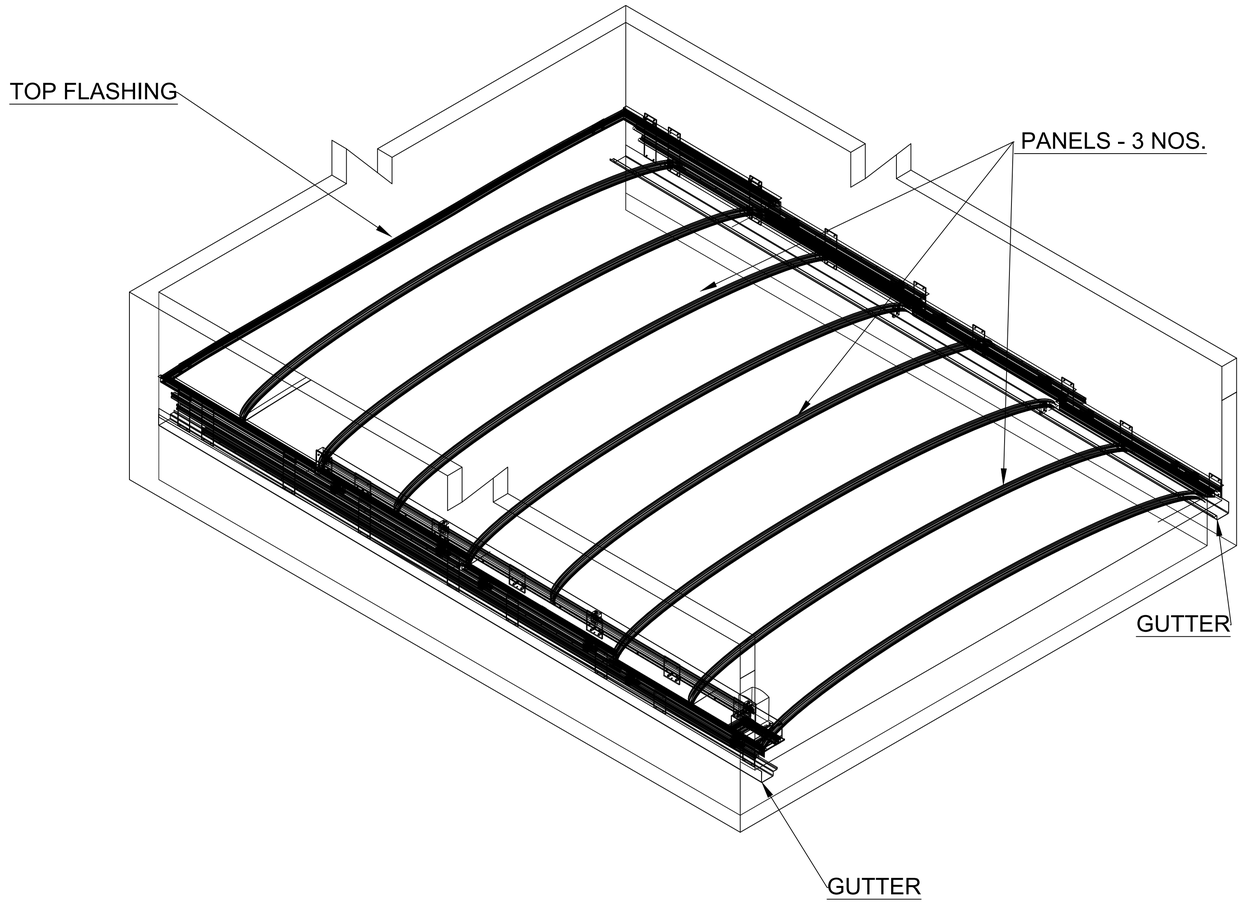

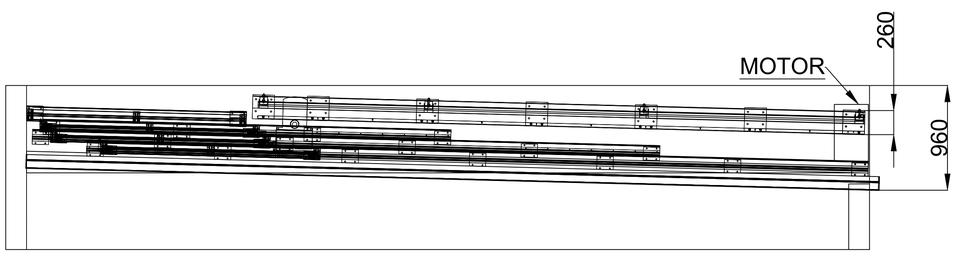

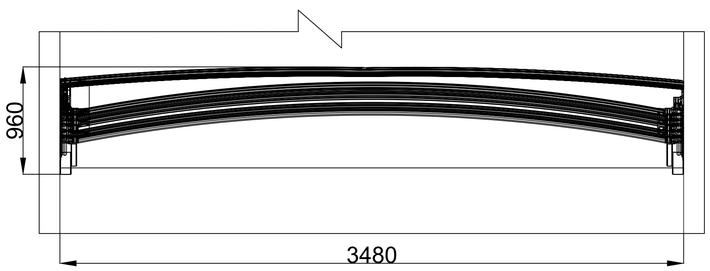

SR NO.	PROFILE /TRACK	SIZES
1	P - 1	60X63XL MM
2	P - 2	50X50XL MM
3	P - 3	105X63XL MM
4	T - 4	105X15XL MM
5	T - 5	135X15XL MM
6	T - 6	100X60XL MM WITH Ø30 BAR

REV NO.	DESCRIPTION	Date	Revised By

TITLE:- GA DRAWING

NIHVA TECHNOLOGIES PVT. LTD.

NIHVA TECHNOLOGIES PVT. LTD. PUNE
Tel : 020 66304033
Email:- info@nihva.com
Website:- www.nihva.com

	NAME	DATE	SIGN
DRAWN	MAHESH S.	26/12/2022	
CHECK	MAHESH S.	26/12/2022	
APPRD.	VIJAY T.	26/12/2022	

CLIENT - NIHVA TECHNOLOGIES PVT.LTD

LOCATION - HYDERABAD

PRODUCT: RETRACTABLE ROOF

If any queries contact : design@nihva.com

DWG NO:-NIHVA/22-23/MFG/0048 REV- 0

ALL DIMENSION ARE IN mm

SCALE: NTS SCALE:-- 1:1 SHEET: 01 OF 01