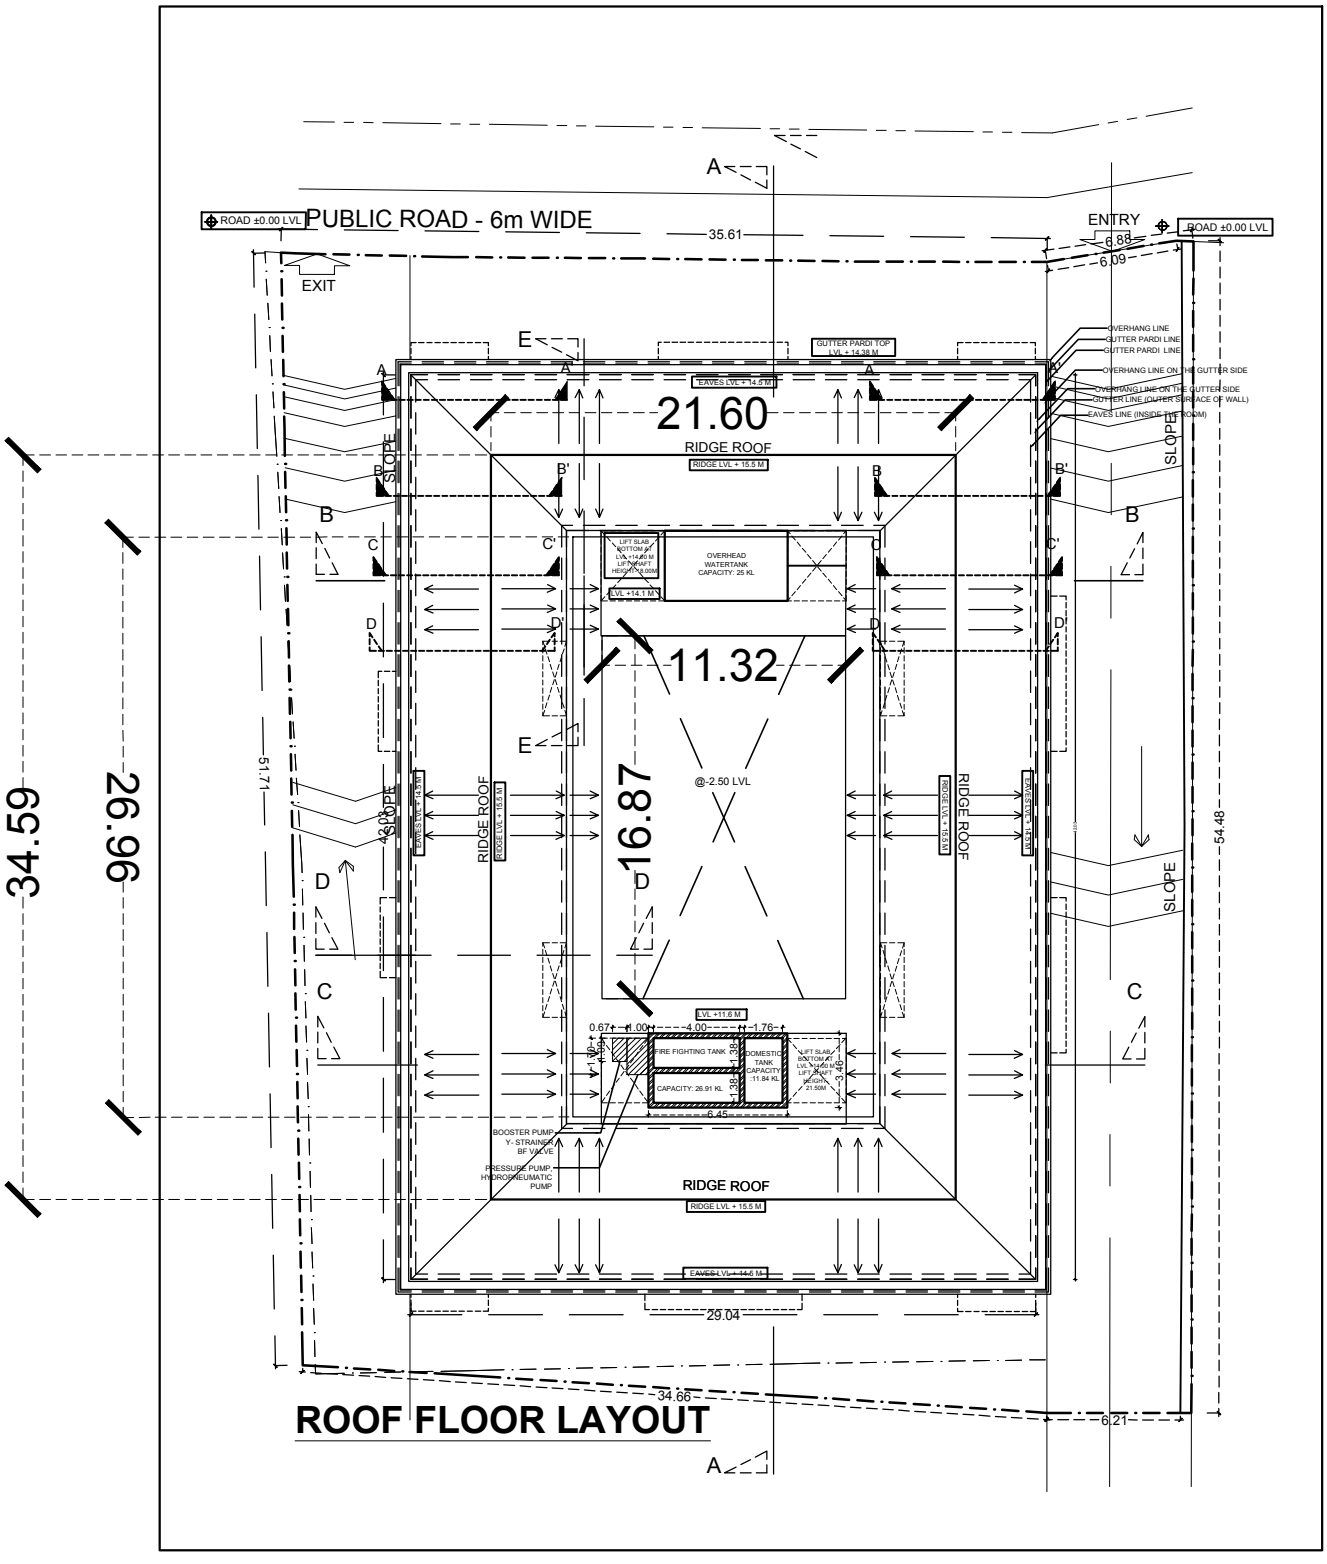

ROAD ±0.00 LVL
PUBLIC ROAD - 6m WIDE
35.61
ENTRY
EXIT
6.88
6.09
ROAD ±0.00 LVL
GUTTER PARDI TOP LVL +14.38 M
EAVES LVL +14.5 M
21.60
RIDGE ROOF
RIDGE LVL + 15.5 M
OVERHEAD WATERTANK CAPACITY: 25 KL
LVL +14.1 M
11.32
16.87
@-2.50 LVL
LVL +11.6 M
FIRE FIGHTING TANK
CAPACITY: 26.91 KL
DOMESTIC TANK CAPACITY 11.84 KL
6.45
4.00
1.76
1.00
0.67
BOOSTER PUMP
Y- STRAINER
BF VALVE
PRESSURE PUMP
HYDROPNEUMATIC PUMP
RIDGE ROOF
RIDGE LVL + 15.5 M
EAVES LVL + 14.6 M
29.04
SLOPE
SLOPE
SLOPE
SLOPE
RIDGE ROOF
RIDGE ROOF
OVERHANG LINE
GUTTER PARDI LINE
GUTTER PARDI LINE
OVERHANG LINE ON THE GUTTER SIDE
OVERHANG LINE ON THE GUTTER SIDE
GUTTER LINE (OUTER SURFACE OF WALL)
EAVES LINE (INSIDE THE ROOM)
54.48
51.71
34.66
6.21
34.59
26.96
ROOF FLOOR LAYOUT