

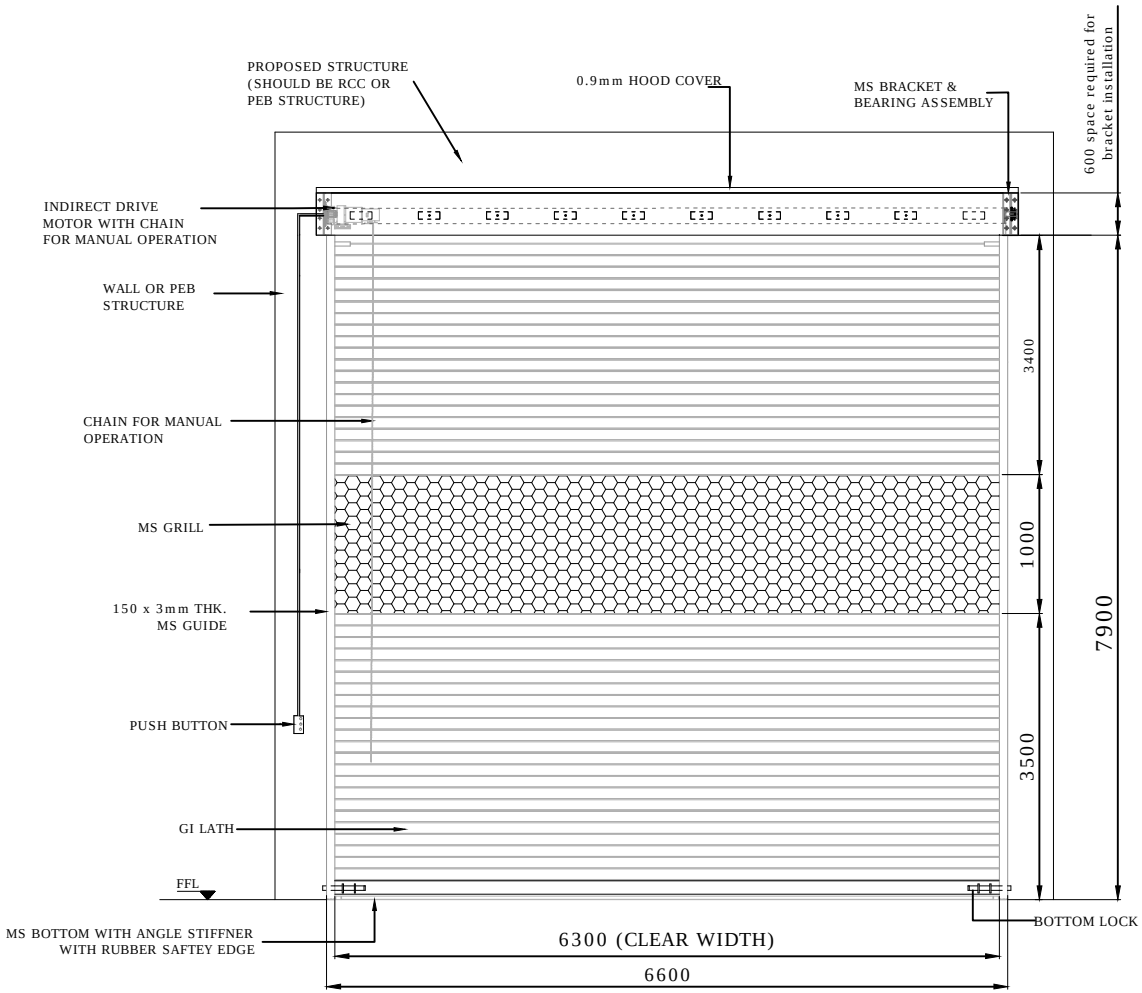



INSIDE ELEVATION

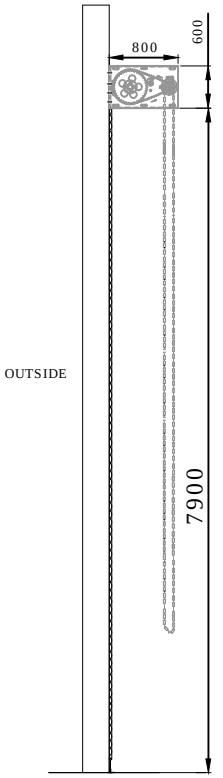


SIDE VIEW

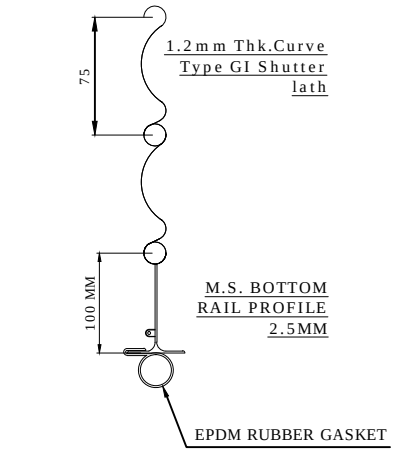

M.S. BOTTOM RAIL PROFILE 2.5MM

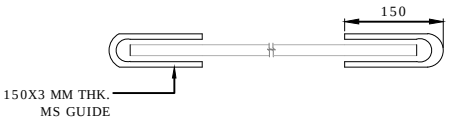

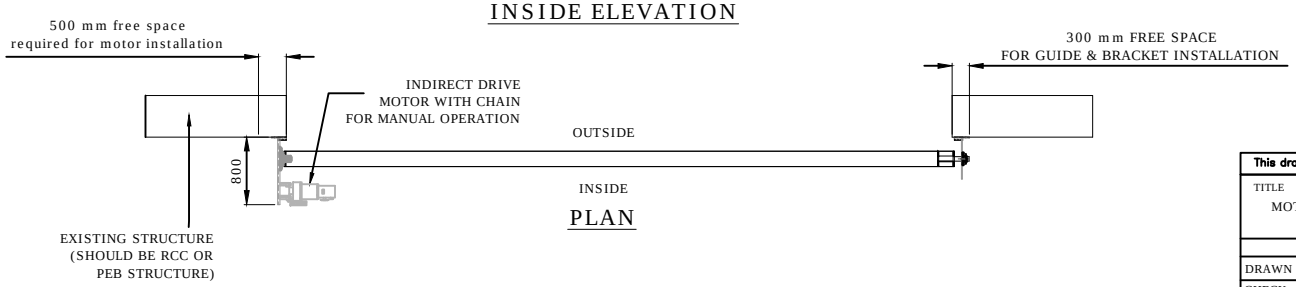

PLAN

CLEAR WIDTH (CW)	CLEAR HEIGHT (CH)	QUANTITY
6300	7900	1

This drawing & designing is the property of NIHVA TECHNOLOGIES. Not to be sold or copied to any other concern.

TITLE: MOTORIZED ROLLING SHUTTER

NIHVA TECHNOLOGIES PVT. LTD. PUNE
Tel : 020 66304033
Email:- info@nihva.com
Website:- www.nihva.com

	SIGN	DATE
DRAWN	OMKAR	29/09/17
CHECK	SAGAR	29/09/17
APPROVAL	SHEKHAR	29/09/17
REV.		

CLIENT -
PROJECT -
SITE -
DWG. NO. : NIHVA/17-18/VDR/0127
If any queries contact : projects@nihva.com
SCALE: NTS | WT: | SHEET: 01 OF 01
ALL DIMENSION ARE IN mm