



GA DRAWING FOR SCISSOR LIFT 1500LX2200W , CAPACITY - 3 TON

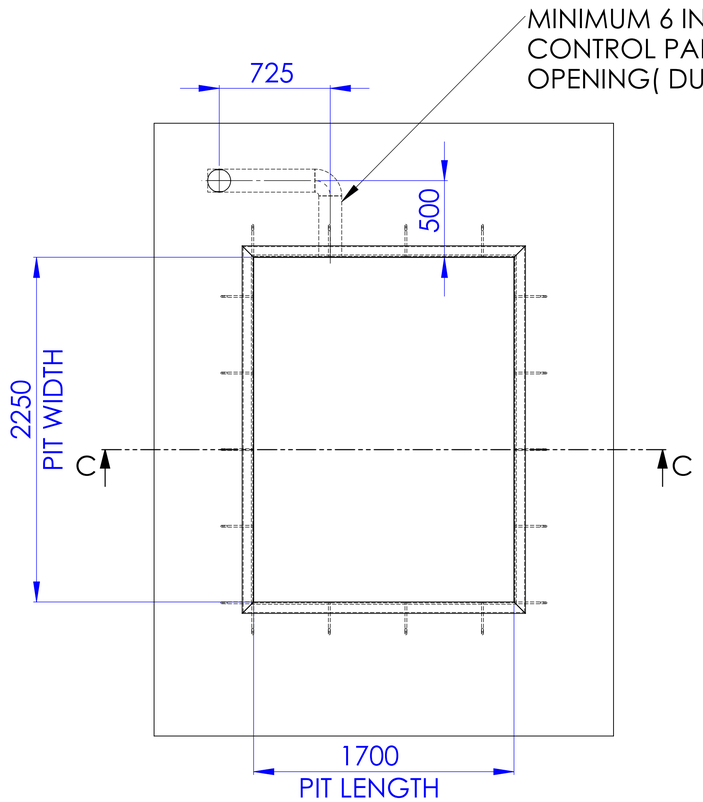


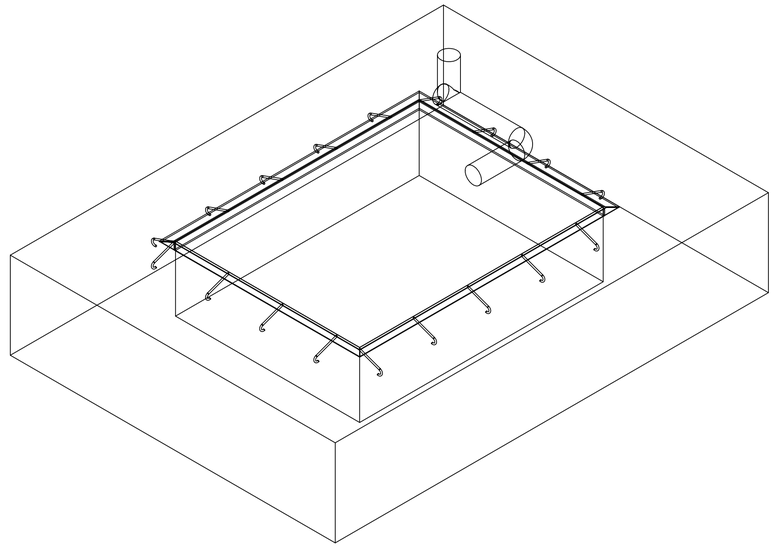

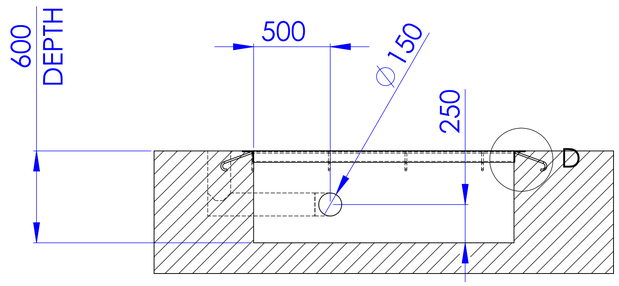

SECTION C-C
SCALE 1 : 20

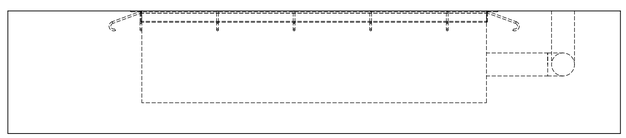

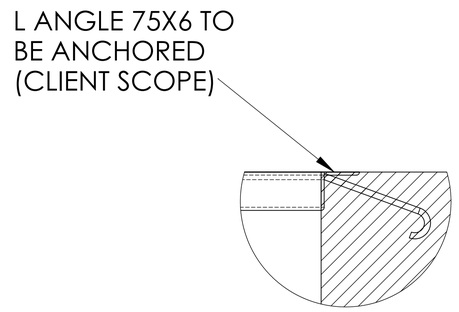

DETAIL D
SCALE 1 : 6

NOTES-

1. PIT CLEAR DIMENSIONS - 2250WX1700LX600H
2. DUCT OF MINIMUM 6 INCH DIAMETER TO BE PROVIED FROM POWERPACK TO PIT OPENING .
3. L ANGLE TO BE ANCHORED AT ALL SIDES OF PIT (ANGLE 75X6 IS IN CLIENT SCOPE).
4. PIT SURFACE SHOULD BE PLAIN & ATLEAST TAKE 4500KG OF LOADING .
5. PIT & ALL CIVIL WORK IS IN CLIENT SCOPE .

UNLESS OTHERWISE SPECIFIED: DIMENSIONS ARE IN MILLIMETERS SURFACE FINISH: TOLERANCES: LINEAR: ANGULAR:	NIHVA We Make Possible	DEBURR AND BREAK SHARP EDGES	DO NOT SCALE DRAWING / REVISION R00
			CLIENT - SERUM , HADAPSAR
NAME / SIGNATURE / DATE			TITLE: PIT DRAWING
DRAWN SIDDHESHWAR 7.7.2021			
CHKD			
APPVD			
MFG			
Q.A	MATERIAL:		DWG NO. NIHVA/21-22/028/SL/PIT / A1
	WEIGHT:		SCALE:1:50 / SHEET 1 OF 1