

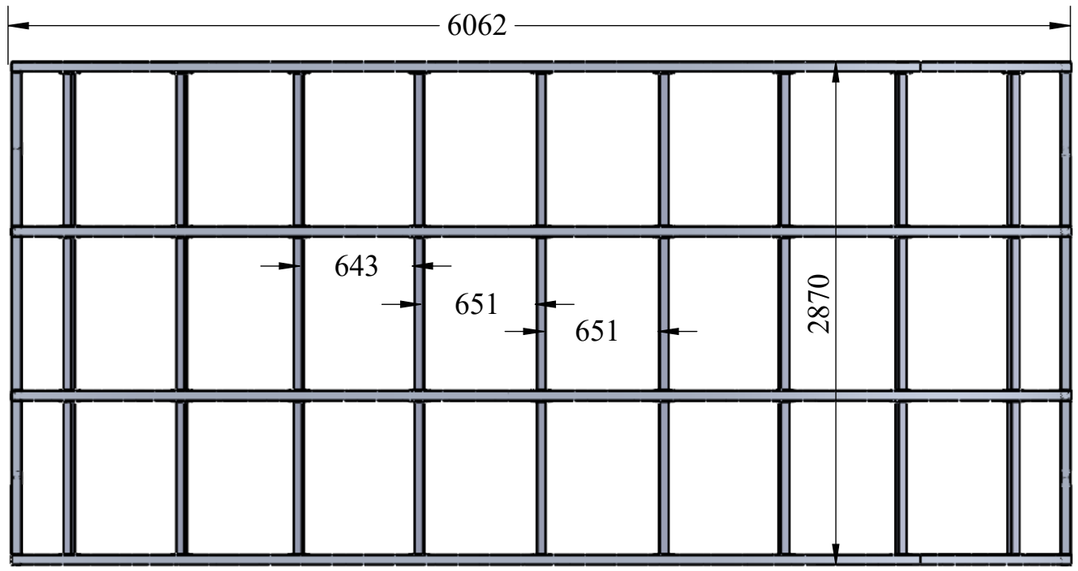


ITEM NO.	PART NUMBER	DESCRIPTION	QTY.
1	PRJ-DR PALAVE-P2.1	GNT_006	2
2	P3.2	GNT_006	2
3	PRJ-DR PALAVE-P2.2	GNT_006	2
4	PRJ-DR PALAVE-SQ TUBE 50X50X1.5 MM L-875	INHOUSE +STD	27

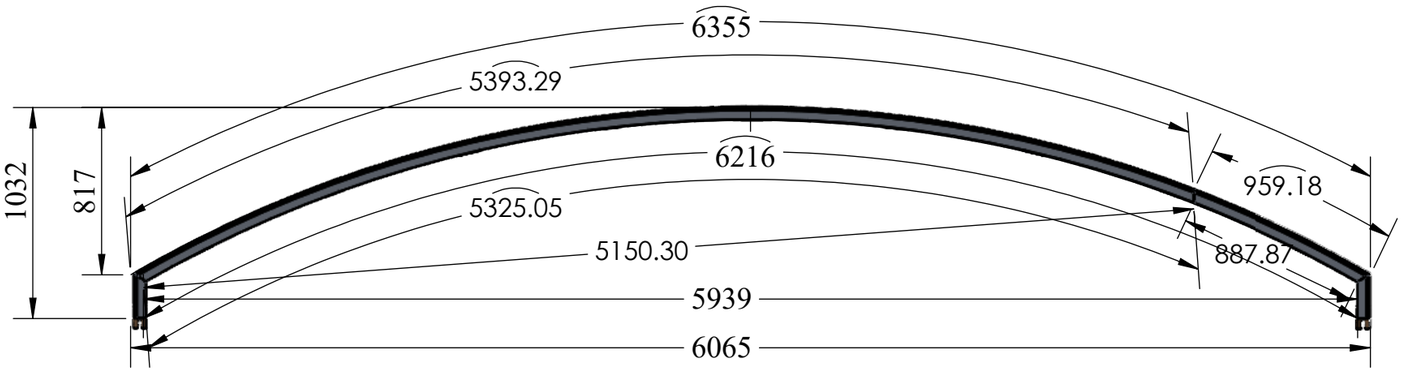

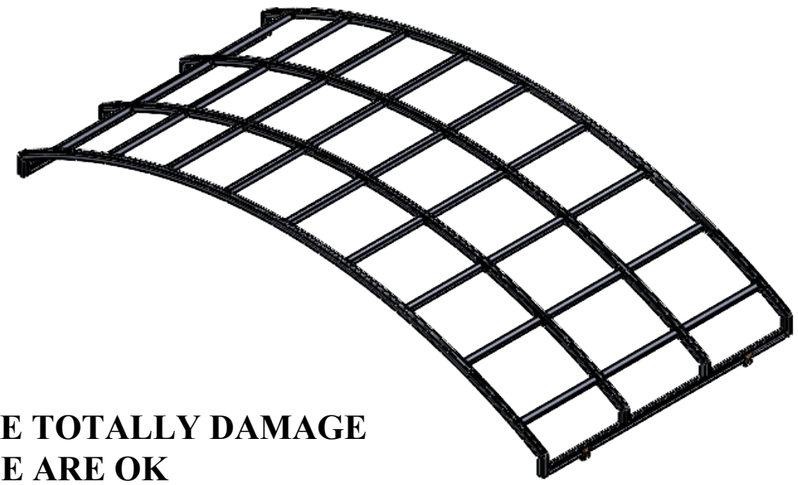

NOTE:-
1) PANEL NO 2 ARE TOTALLY DAMAGE
GNT 006 3 PROFILE ARE OK
BUT 1 CORNER PROFILE IS NOT OK
2) THIS SUPPORT TUBE NOT CONSIDER .

TITLE - ROOF AUTOMATION				NIHVA TECHNOLOGIES PVT.LTD.PUNE	
DWG NO - NTPL-236-PM-001-00-00-00				Website - www.nihva.com	
	NAME	SIGNATURE	DATE	PROJECT NO - NTPL-236-PM	
DRAWN	V.B.		17-06-2025	PRODUCT - RETRACTABLE ROOF	REVISION -
CHK'D	S.W.		17-06-2025	SITE LOCATION -	WEIGHT -
APPV'D	V.T.		17-06-2025	MATRIAL -	QTY - 1
if any queries contact - supportautomation@nihva.com				PROJECTION METHOD:	SCALE :
ALL DIMENSION ARE IN mm			A3		SHEET 2 OF 15