

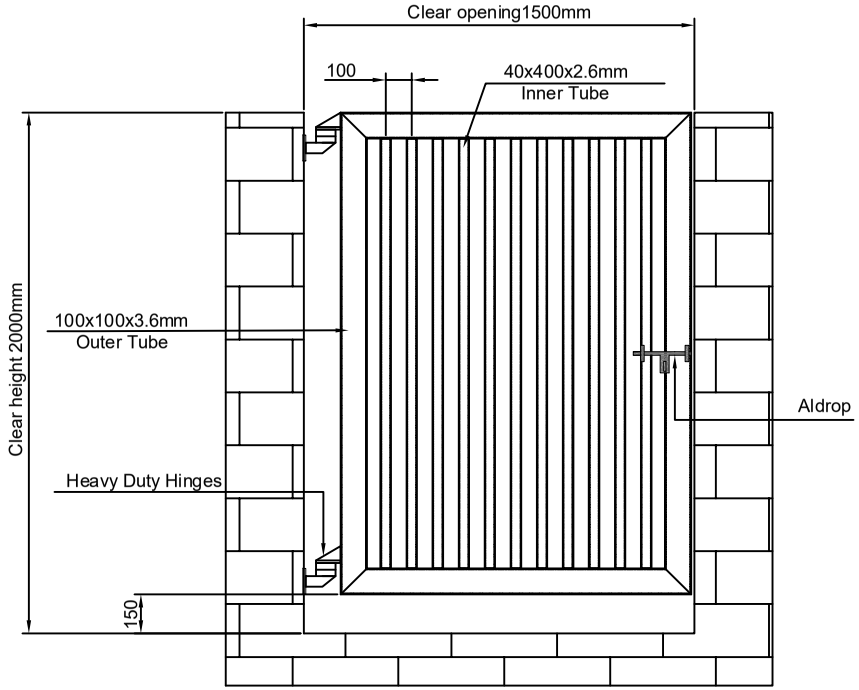


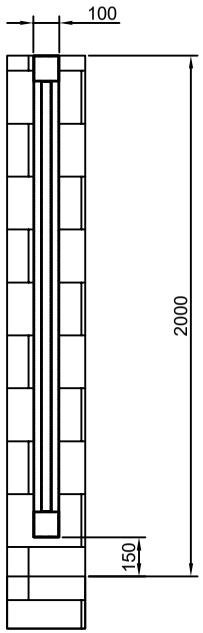

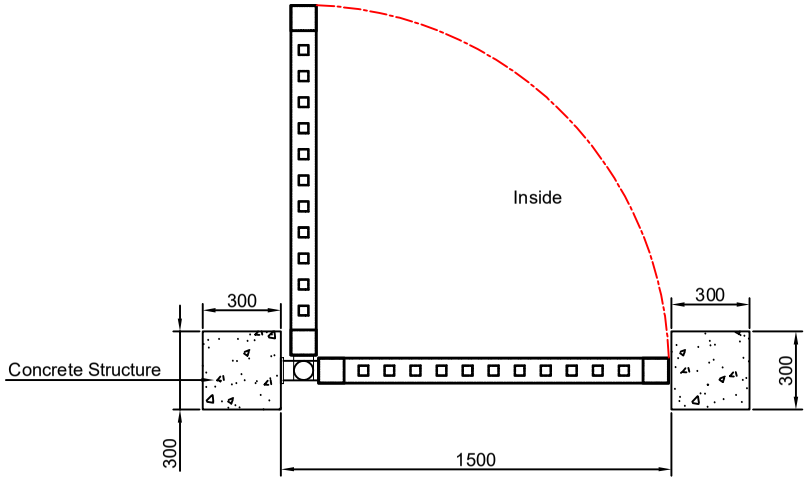

Technical Specs of Swing Gate

1. Opening Width - 1500mm
2. Gate Height - 2000mm
3. Outer tube size - MS SHS 100x100x3.6mm
4. Inner tube size - MS SHS 40x40x2.6mm
5. Total leaf weight ≈ Approx.196 kg
6. Operation - Manual

Note-

1. All dimension are in mm.
2. All civil work is under client scope.

This drawing & design is the property of NIHVA TECHNOLOGIES. Not to be sold or copied to any other concern.

TITLE:- WICKET GATE

NIHVA TECHNOLOGIES PVT. LTD.
NIHVA TECHNOLOGIES PVT. LTD. PUNE
Tel : 020 66304033
Email:- info@nihva.com
Website:- www.nihva.com

	NAME	DATE	SIGN
DRAWN	SUJATA.B	14-10-2021	
CHECK	G.PATIL	14-10-2021	
APPRD.	A.KURHADE	14-10-2021	

If any queries contact : design@nihva.com

ALL DIMENSION ARE IN mm

CLIENT -

LOCATION - SCON PROJECT

PRODUCT - WICKET GATE

DWG NO:-NIHVA\21-22\0251 | REV- 0

SCALE: NTS | SCALE:-- 1:1 | SHEET: 01 OF 01

Rev No.	Revision	Date	Revised By

CAD PATH:-