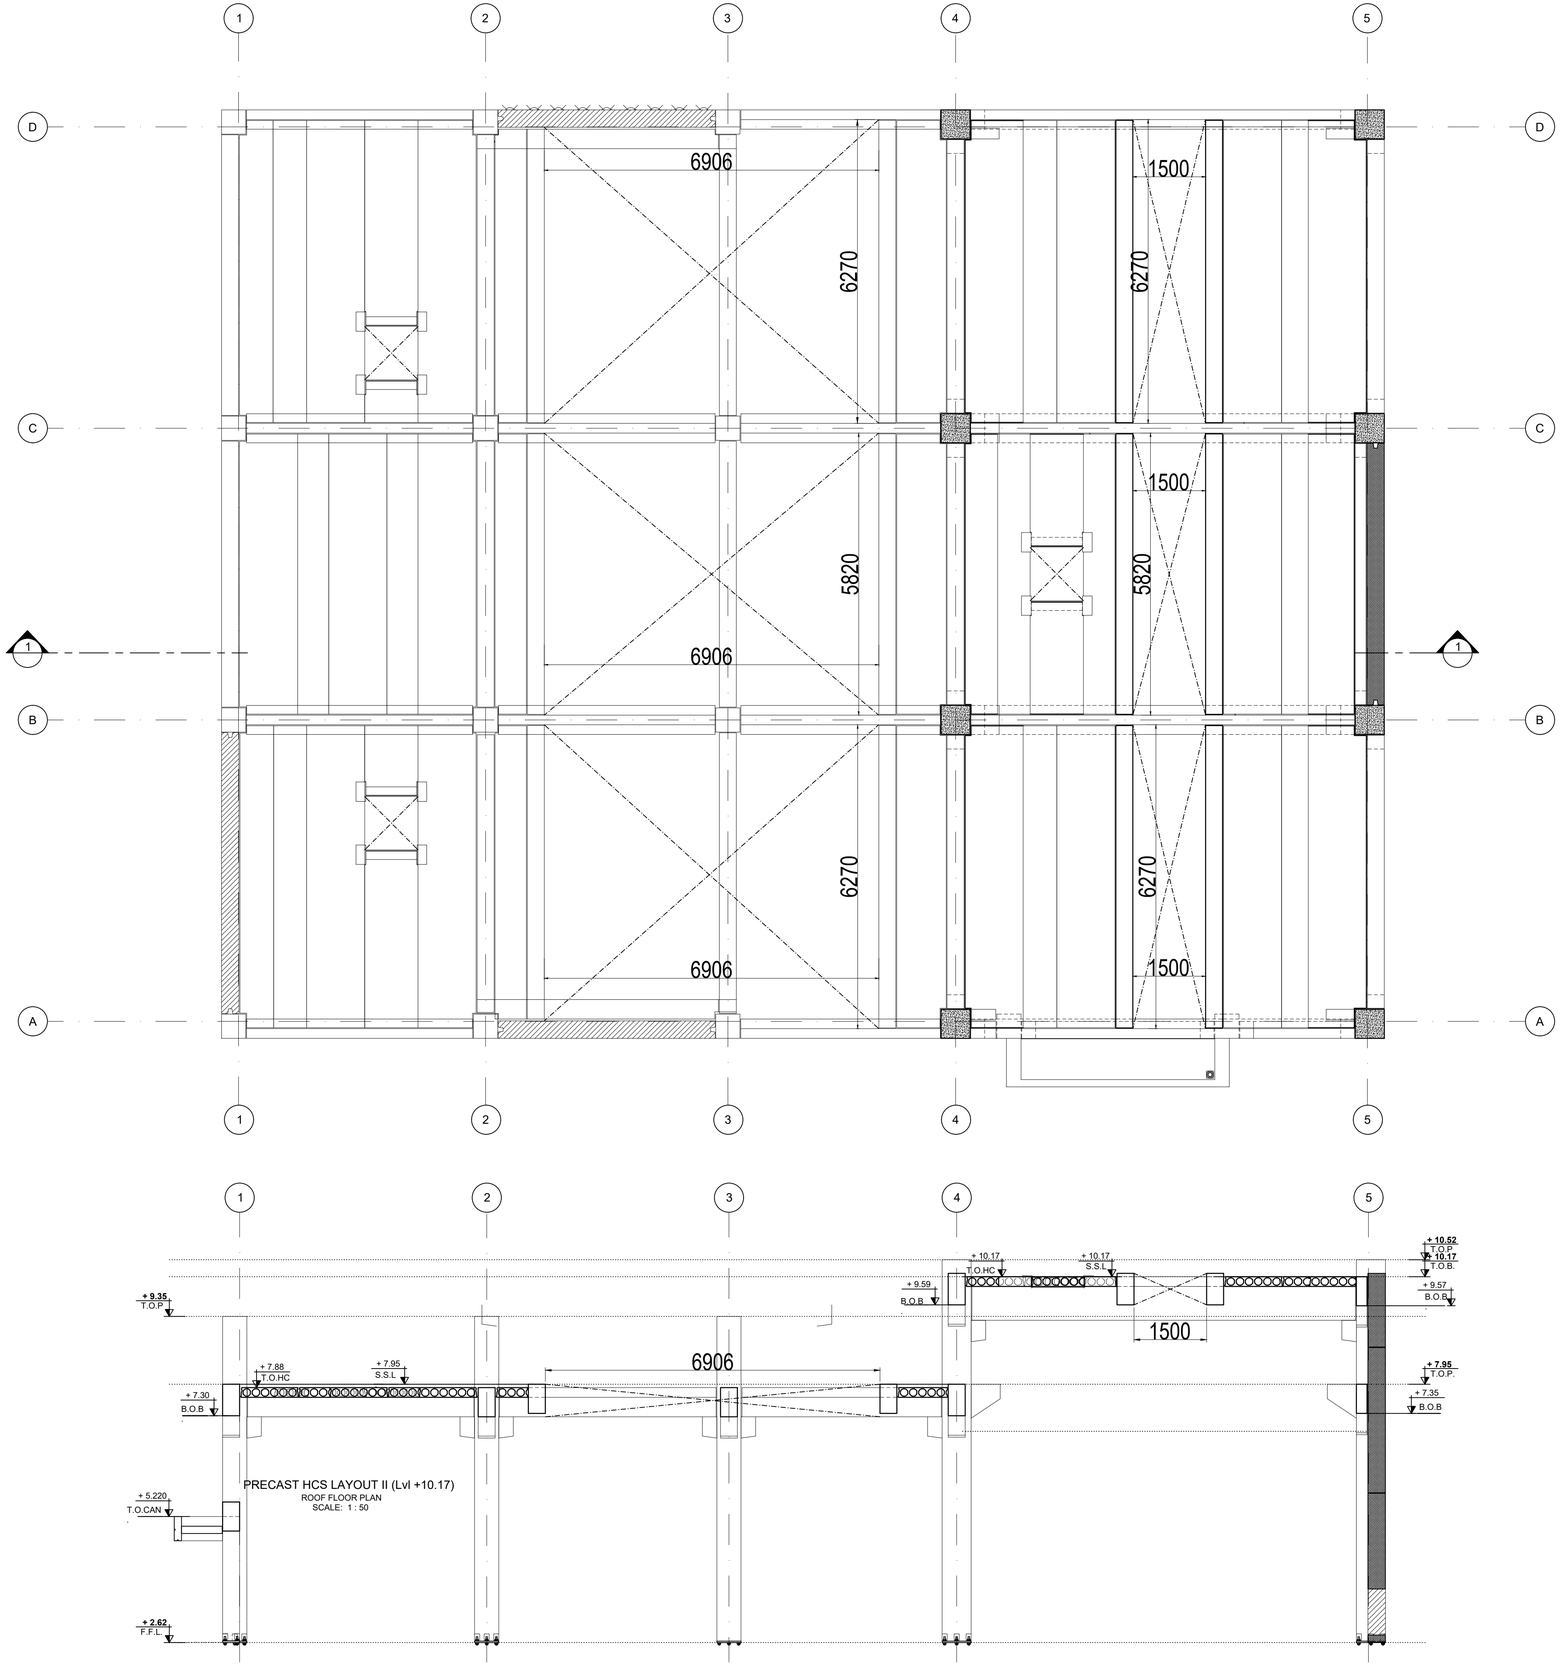


PRECAST HCS LAYOUT II (Lvl +10.17)
ROOF FLOOR PLAN
SCALE: 1 : 50

Section 1-1

SCALE: 1 : 50