


N O T E S :

1. ALL DIMENSIONS ARE IN MILLIMETERS UNLESS MENTIONED.
2. DRAWINGS SHALL NOT BE MEASURED, FOLLOW WRITTEN DIMENSIONS.
3. ANY DISCREPANCY IN THIS DRAWING OR ANY OTHER DRAWINGS RELATED TO THIS DRAWING SHALL BE BROUGHT TO THE NOTICE OF THE ARCHITECTS IMMEDIATELY.
4. THIS DRAWING IS TO BE READ IN CONJUNCTION WITH RELEVANT DETAIL DRAWINGS AS MENTIONED IN THE DRAWING.
5. ALL EXTERNAL/INTERNAL MASONARY WALLS ARE 230MM / 115MM THK FLYASH BRICKWORK AND TO BE BUILT TILL 3000MM LEVEL UNLESS OTHERWISE MENTIONED.

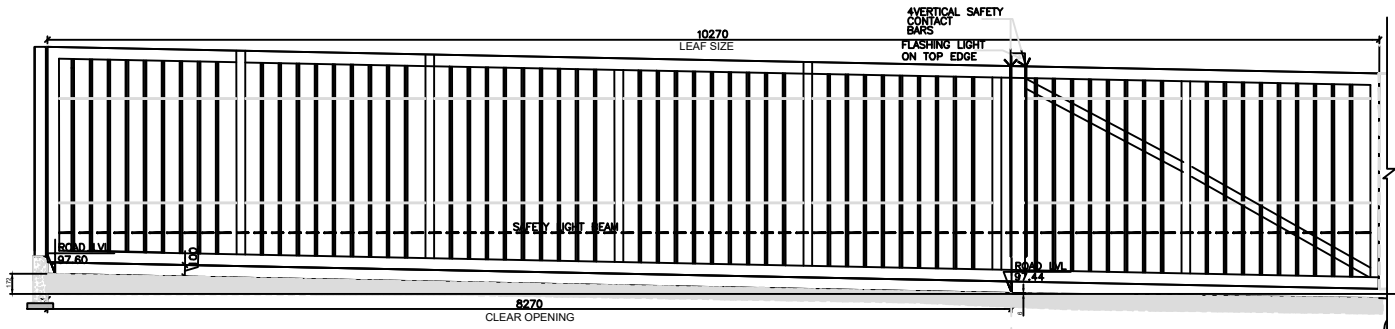

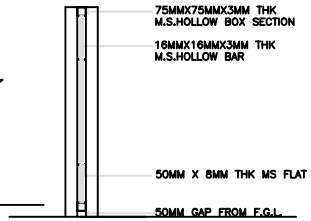

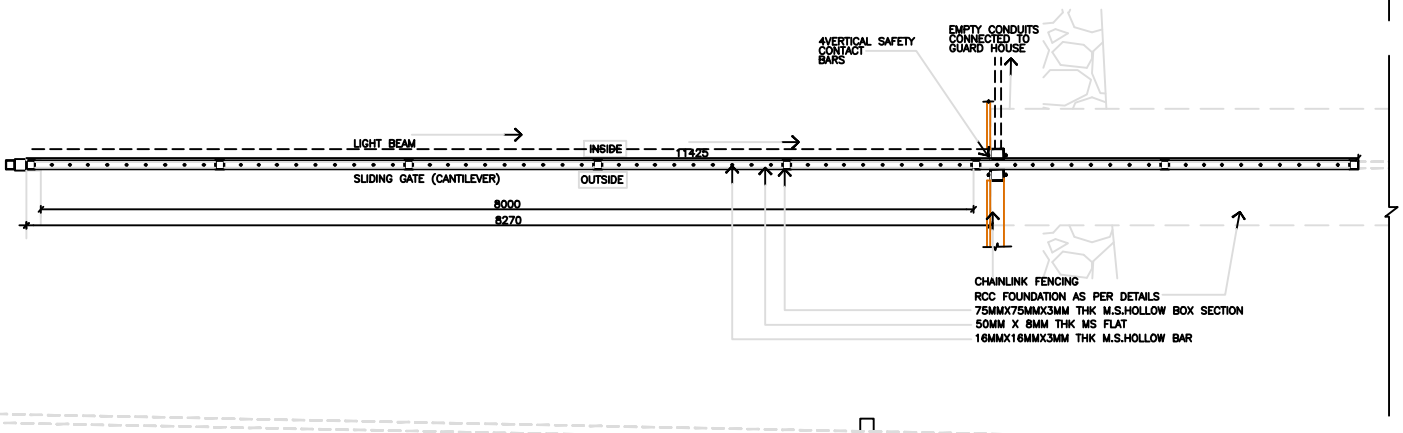





TOTAL GATE WEIGHT = 700 Kg

This drawing & design is the property of NIHVA TECHNOLOGIES. Not to be sold or copied to any other concern.

TITLE:- Motorized Cantilever Sliding Gate G.A.drawing

	NAME	DATE	SIGN
DRAWN	NIRMALA	19/10/2023	
CHECK	A.K	19/10/2023	
APPRD.	V.T	19/10/2023	

If any queries contact : design@nihva.com

ALL DIMENSION ARE IN mm

NIHVA TECHNOLOGIES PVT. LTD.
NIHVA TECHNOLOGIES PVT. LTD, PUNE
Tel : 020 66304033
Email:- info@nihva.com
Website:- www.nihva.com

CLIENT -

LOCATION -

PRODUCT - Motorized Sliding Gate | QTY-01

DWG NO:- | REV-00

SCALE: NTS | SCALE:-- 1:1 | SHEET: 01 OF 01