


DRAWING

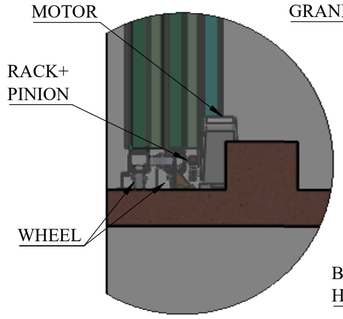


DETAIL A
SCALE 1 : 18

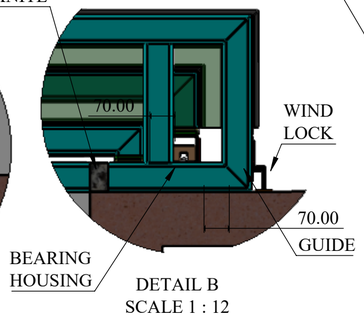


DETAIL B
SCALE 1 : 12

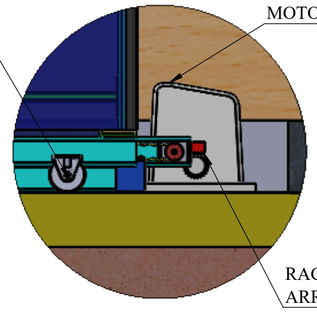


DETAIL C
SCALE 1 : 12

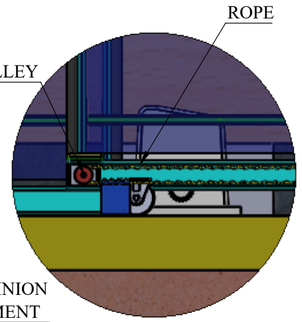


DETAIL D
SCALE 1 : 12

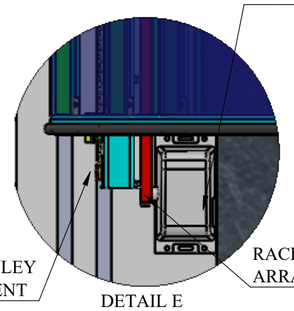


DETAIL E
SCALE 1 : 12

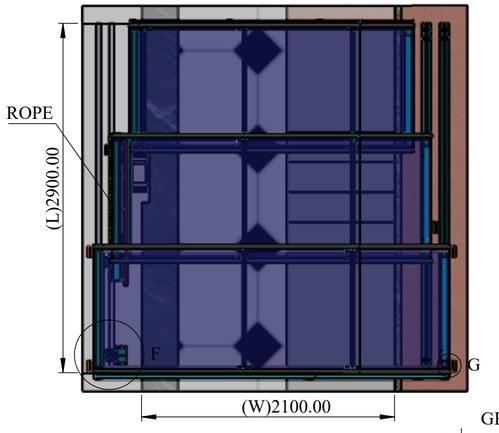

T.V.

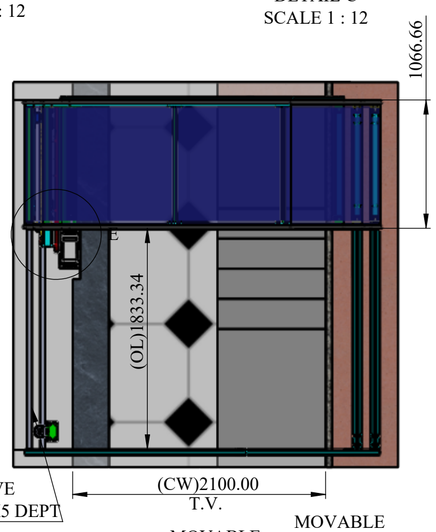


T.V.

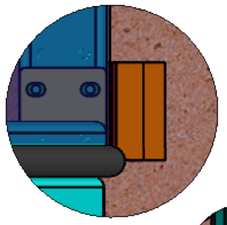


DETAIL G
SCALE 1 : 4


WIND LOCK

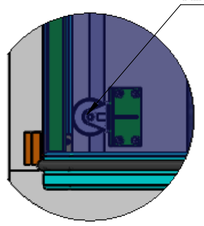


DETAIL F
SCALE 1 : 12

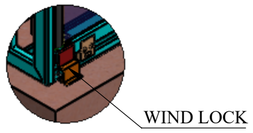


DETAIL H
SCALE 1 : 18

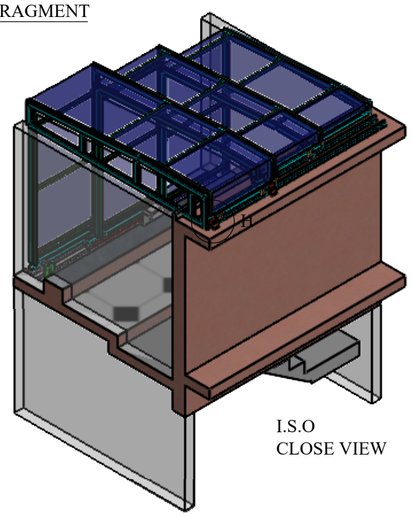


I.S.O
CLOSE VIEW

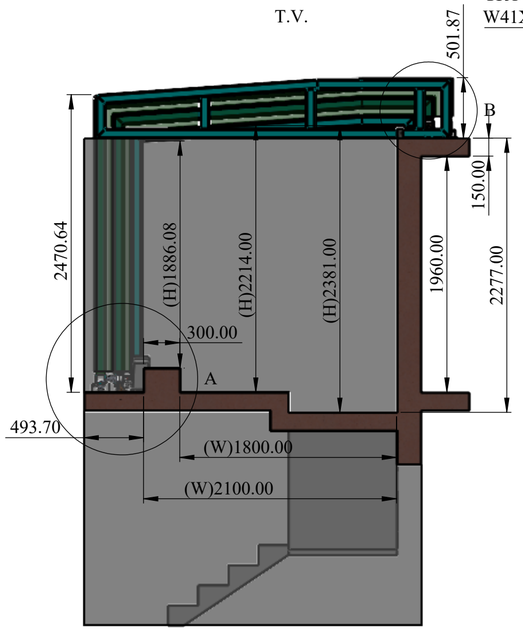


F.V.

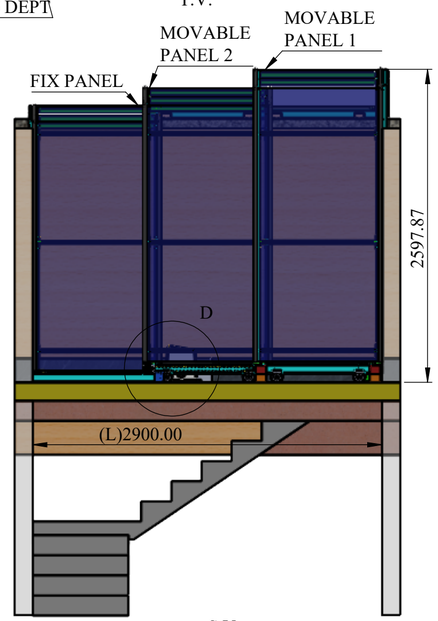

S.V.

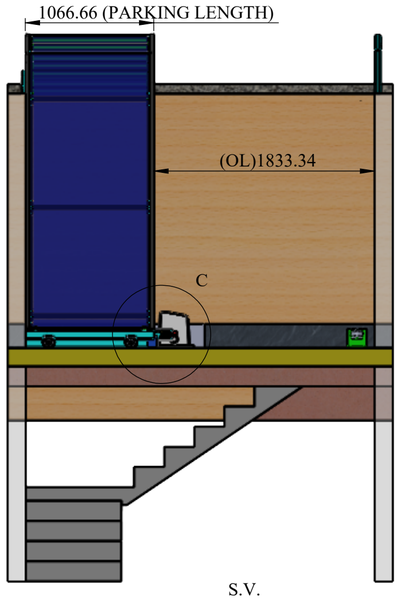

S.V.

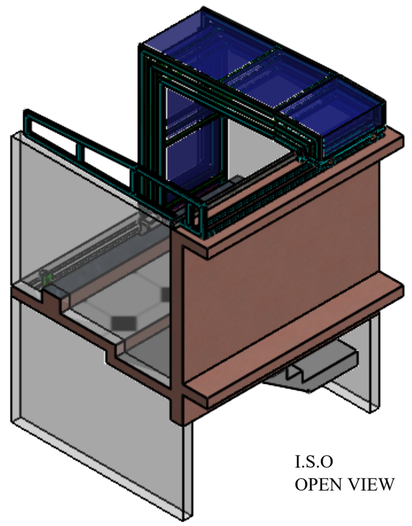

I.S.O
OPEN VIEW

REV DESCRIPTION	DATE	REV NO
	29-08-2026	REV 00
1.		

NOTE :

THIS DRAWING IS ONLY FOR CLIENT APROVAL
BASE STRUCTURE IN CLIENT SCOPE
EPDM RUBBER FLAPER IS PROVIDED FOR AIR & WATER SEAL
TOTAL SYSTEM WEIGHT - 2223 KG
FOR WHEEL GUIDE REQ TO CREATE A GROOVE W41X5MM DEPT.

SPECIAL INSTRUCTION'S :

This drawing & design is the property of NIHVA TECHONOLOGIES PVT. LTD. Not to be sold or copied to any other concern

TITLE - ROOF AUTOMATION

DWG NO - NTPL-

NIHVA TECHNOLOGIES PVT.LTD.PUNE
Website - www.nihva.com

	NAME	SIGNATURE	DATE
DRAWN	V.W.		29-08-2026
CHK'D	S.P.		31-08-2026
APPV'D	V.T.		31-08-2026

PRODUCT - L SHAPE ENCLOSURE
CLIENT NAME - LODHA GROUP.
SITE LOCATION - MUMBAI - MATUNGA.
MATRIAL - | QTY - 1

If any queries contact - info@nihva.com
ALL DIMENSION ARE IN mm | A2
PROJECTION METHOD:
SCALE :
SHEET 1 OF 1