

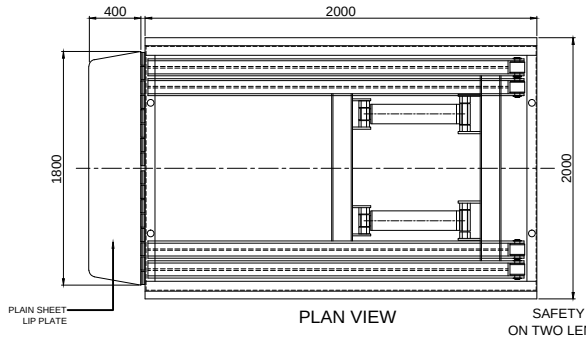



PLAN VIEW

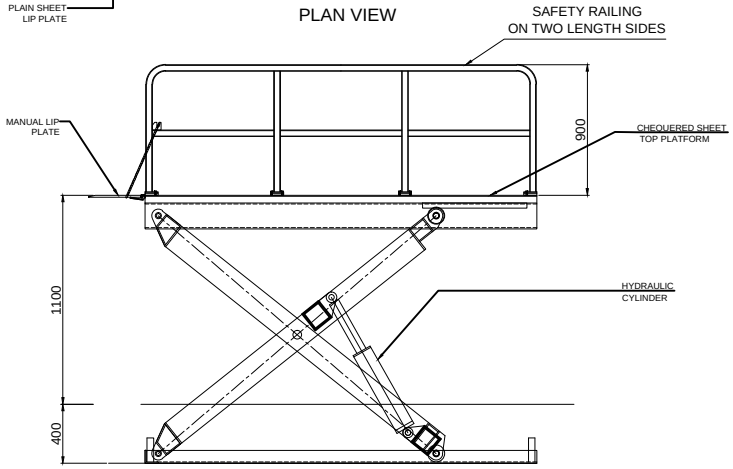


FRONT VIEW - OPEN POSITION OF SCISSOR LIFT

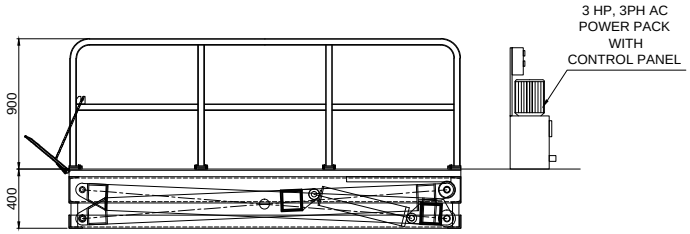


FRONT VIEW - SHUT POSITION OF SCISSOR LIFT

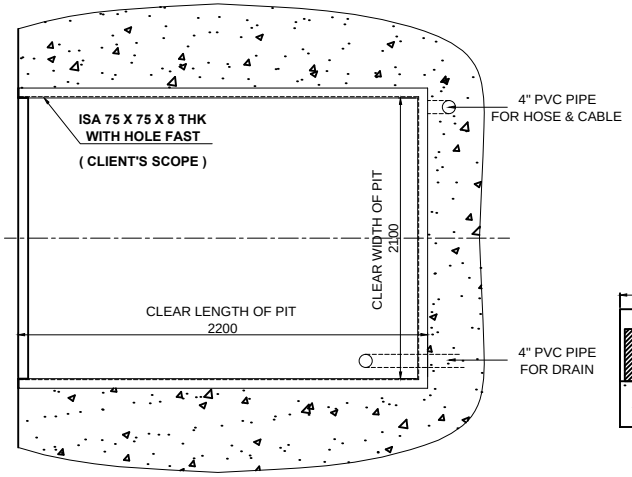

TOP VIEW OF PIT

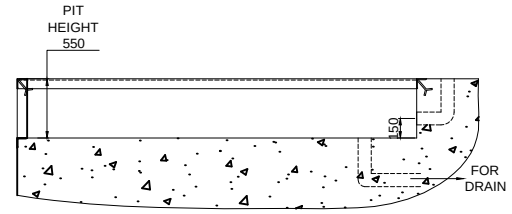

FRONT VIEW OF PIT

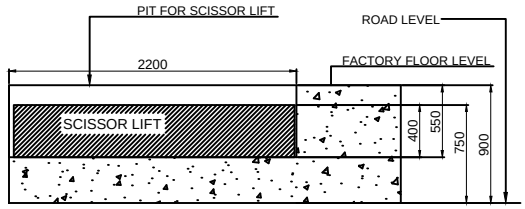

SCISSOR LIFT INSTALLATION LAYOUT

TOLERANCE - ±5mm

PAINT - RAL 1004 GOLDEN YELLOW

CAPACITY	3 TON
PLATFORM SIZE	2000 (L) X 2000(W)
POWER PACK	3 HP, 3 PH
SHUT HEIGHT	400 MM
LIFT HEIGHT FROM PLATFORM TOP	1100 MM
TOTAL HEIGHT FROM GROUND	1850 MM

NOTE :

1. HYDRAULIC HOSE LENGTH FROM POWERPACK TO PIT OPENING : 5 MTR
2. ELECTRICAL CABLE FROM CONTROL PANEL TO PIT OPENING : 5 MTR
3. COLOR : GOLDEN YELLOW RAL 1004.
4. INPUT SUPPLY : 3 PHASE 400 VOLT WITH NEUTRAL NEAR POWER PACK LOCATION.
5. PAINTING - ALL PARTS IN GOLDEN YELLOW , ZEBRA MARKS FOR SIDE OF PLATFORM
6. GA DRAWING WITH ALL VIEWS IN SCALE 1:1 TO BE PROVIDED BEFORE MANUFACTURING.
7. OPERATION & MAINTENANCE MANUAL WITH SPARE PARTS LIST TO BE PROVIDED .
8. ALL RAW MATERIAL TEST CERTIFICATES TO BE PROVIDED .
9. INDIVIDUAL TEST CERTIFICATES OF HYDRAULIC CYLINDER & HYDRAULIC POWER-PACK TO BE PROVIDED BY SUPPLIER.
10. LOAD TEST TO BE PROVIDED BEFORE DISPATCH FOR RATED LOAD .

This drawing & designing is the property of NIHVA TECHNOLOGIES. Not be sold or copy to any other concern.

TITLE
PIT MOUNTED ELECTRO-HYDRAULIC SCISSOR LIFT

NIHVA TECHNOLOGIES PVT. LTD.

NIHVA TECHNOLOGY PVT. LTD. PUNE
Tel : 020 66304033
Email:- info@nihva.com
Website:- www.nihva.com

	SIGN	DATE
DRAWN	SIDDHESHWAR	6.4.2021
CHECK	SIDDHESHWAR	6.4.2021
REV.		
APPROVAL		

CLIENT -
PROJECT -
SITE -
DWG. NO. : NIHVA/20-21/VDR/0122

If any queries contact : nihvacare@nihva.com
SCALE: NTS | WT: | SHEET: 01 OF 01
ALL DIMENSION ARE IN mm