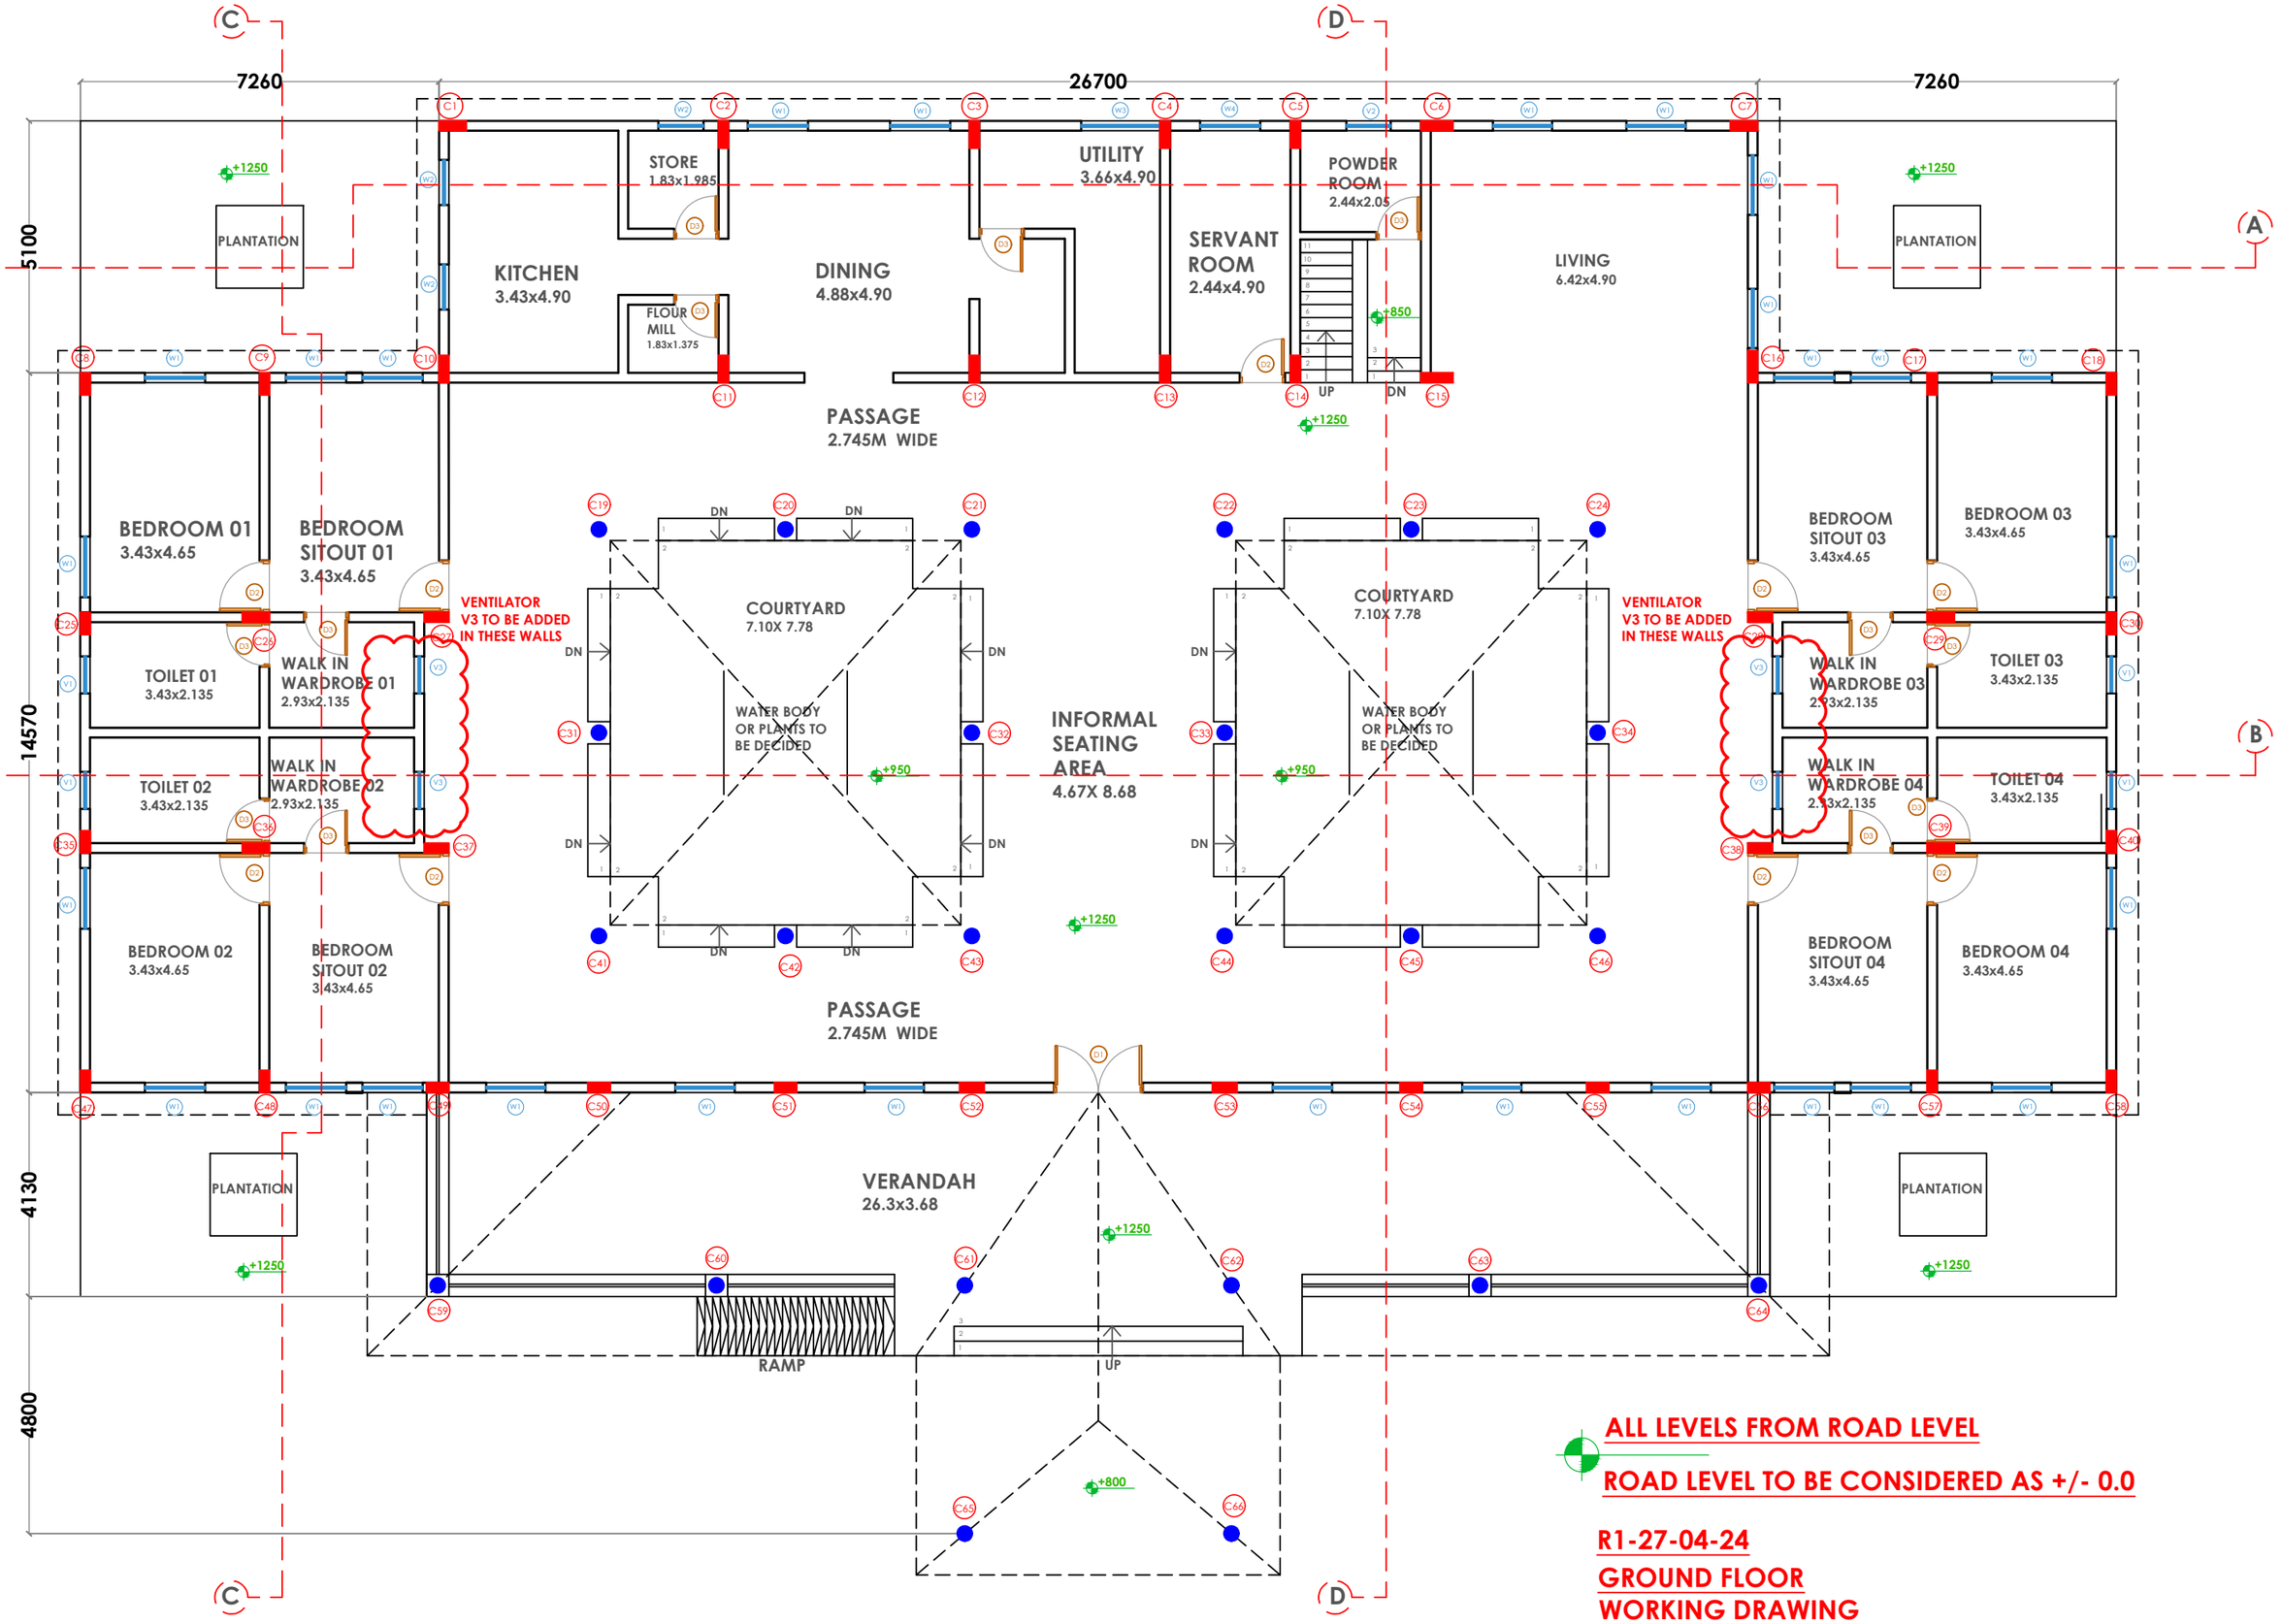


ALL LEVELS FROM ROAD LEVEL

ROAD LEVEL TO BE CONSIDERED AS +/- 0.0

R1-27-04-24

GROUND FLOOR
WORKING DRAWING

PROPOSED BUNGALOW FOR SHRI. SAWADE, JALNA.

N

DATE: 18.07.2023
DEALT: SRUJAN / ATHARRV D
PATH: C5/E/PROJECTS/SAWADE/CAD/INTERIOR LAYOUT

3D
ARCHITECTS AND INTERIOR DESIGNERS