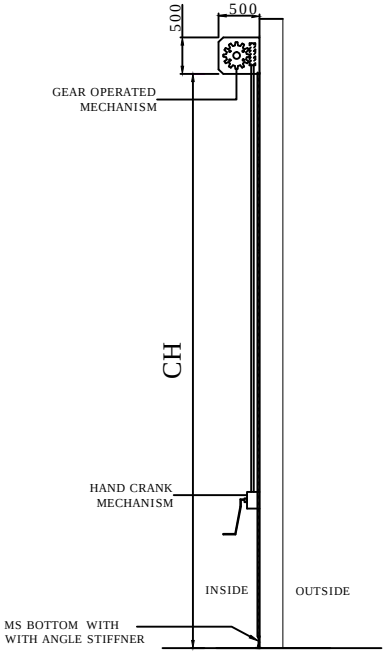

SIDE VIEW

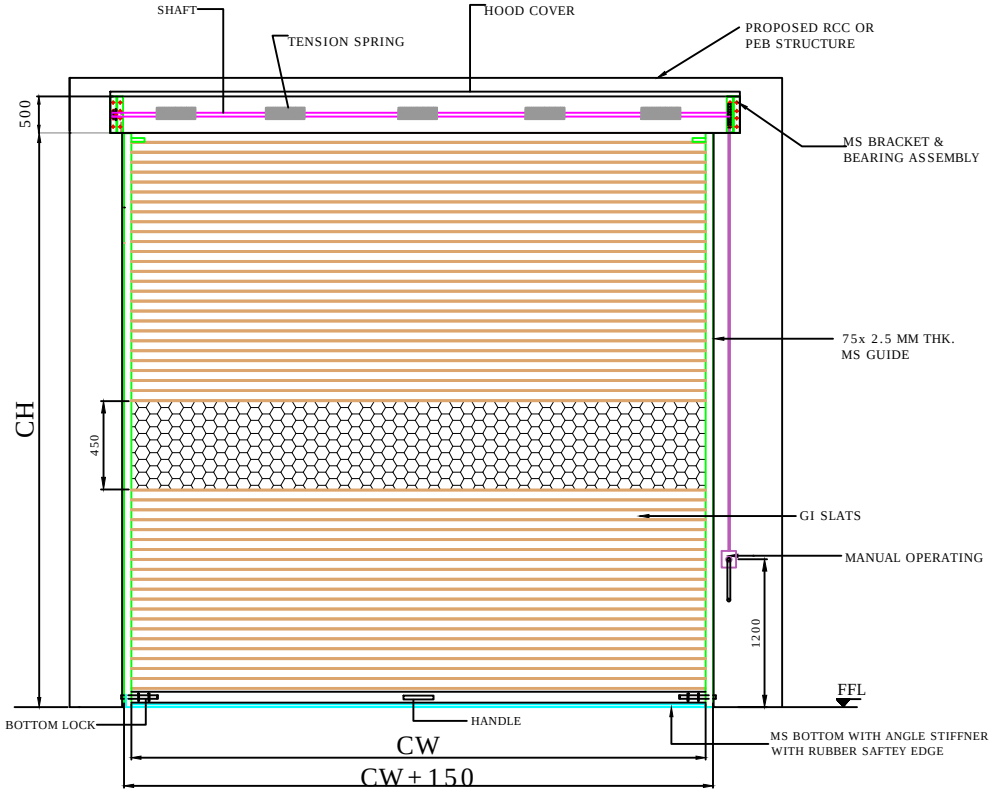

INSIDE ELEVATION

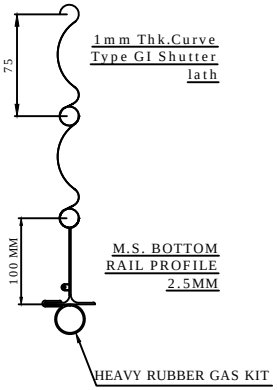

M.S. BOTTOM RAIL PROFILE 2.5MM

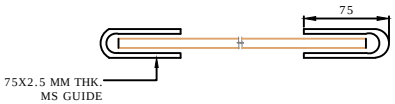

PLAN

CLEAR WIDTH (CW)	CLEAR HEIGHT (CH)	QUANTITY
3000	3000	3
3000	4000	1

DIMENSION :

CLEAR WIDTH	CLEAR HEIGHT	QUANTITY
3000 mm	3000 mm	3 NOS.
3000 mm	4000 mm	1 NOS.

MATERIAL :

THICKNESS :

NOTE: REQUIRED STRUCTURE FOR SHUTTER SHALL BE IN CLIENT SCOPE.

NIHVA TECHNOLOGIES PVT. LTD. PUNE
Email:- info@nihva.com
Website:- www.nihva.com

TITLE:

GEAR OPERATED ROLLING SHUTTER

CLIENT'S APPROVAL :

CLIENT - B.G.SHIRKE

PROJECT - TACO

SITE LOCATION - CHAKAN,PUNE

DWG. NO. : NIHVA/16-17/158

SCALE: NTS	WT:	SHEET:1 OF 1

DRAWN BY: OMKAR	DATE: 02-03-2017
CHECK : SAGAR P.	DATE: 02-03-2017
APPROVED : R.K.	DATE: 02-03-2017

If any queries contact : projects@nihva.com

NOTE: ALL DIMENSIONS ARE IN mm

THIS DRAWING & DESIGN IS THE PROPERTY OF NIHVA TECHNOLOGIES. NOT TO BE SOLD OR COPY TO ANY OTHER CONCERN.