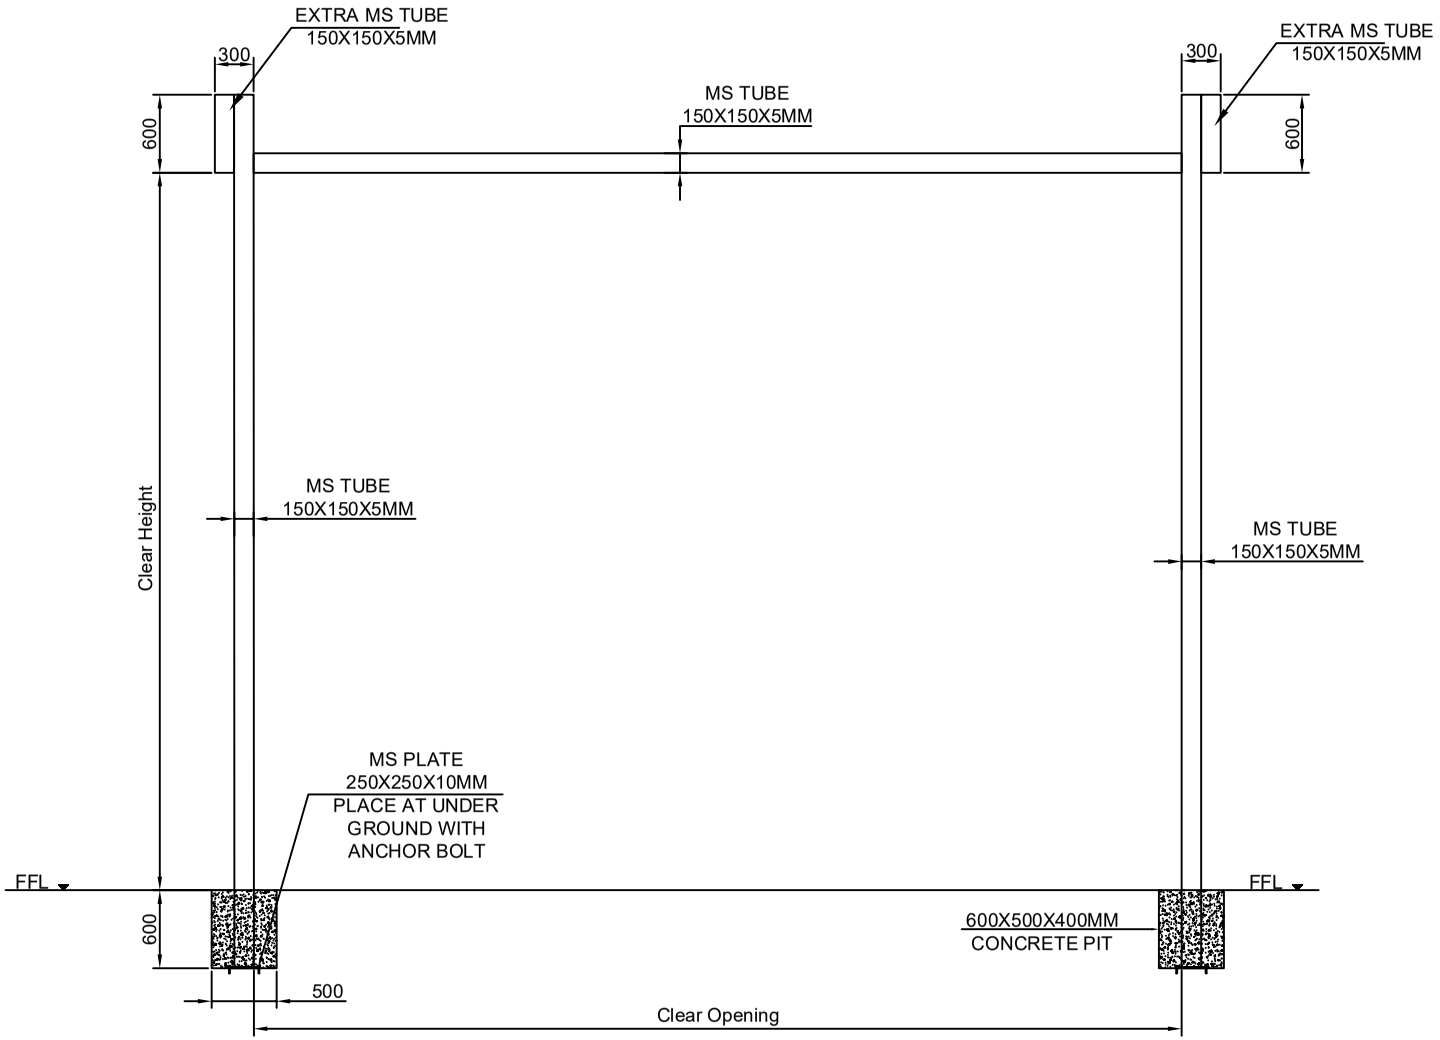


Structure Details for CRM Door-02			
Sl No.	Clear Width(CW)	Clear Height(CH)	Qty
1	7100	5570	1

Note:-
1.All dimensions are in MM
2.All Civil work and required MS Structure support will be in client scope

Rev No.	Revision	Date	Revised By
01.	Clear opening size ghas been changed from 7300 to 7100mm	14/06/2022	Sujata

This drawing & design is the property of NIHVA TECHNOLOGIES. Not to be sold or copied to any other concern.

TITLE:- MS TUBE STRUCTURE

NIHVA
NIHVA TECHNOLOGIES PVT. LTD.

NIHVA TECHNOLOGIES PVT. LTD. PUNE
Tel : 020 66304033
Email:- info@nihva.com
Website:- www.nihva.com

	NAME	DATE	SIGN
DRAWN	SUJATA	10/06/2022	
CHECK	P.JAIN	10/06/2022	
APPRD.	V.TARAK	10/06/2022	

If any queries contact : design@nihva.com

ALL DIMENSION ARE IN mm

CLIENT - LESTECH
LOCATION - POSCO MANGAON
PRODUCT - SLIDING DOOR
DWG NO:-NIHVA/22-23/CL/0057 REV- 01
SCALE: NTS SCALE:-- 1:1 SHEET: 01 OF 01