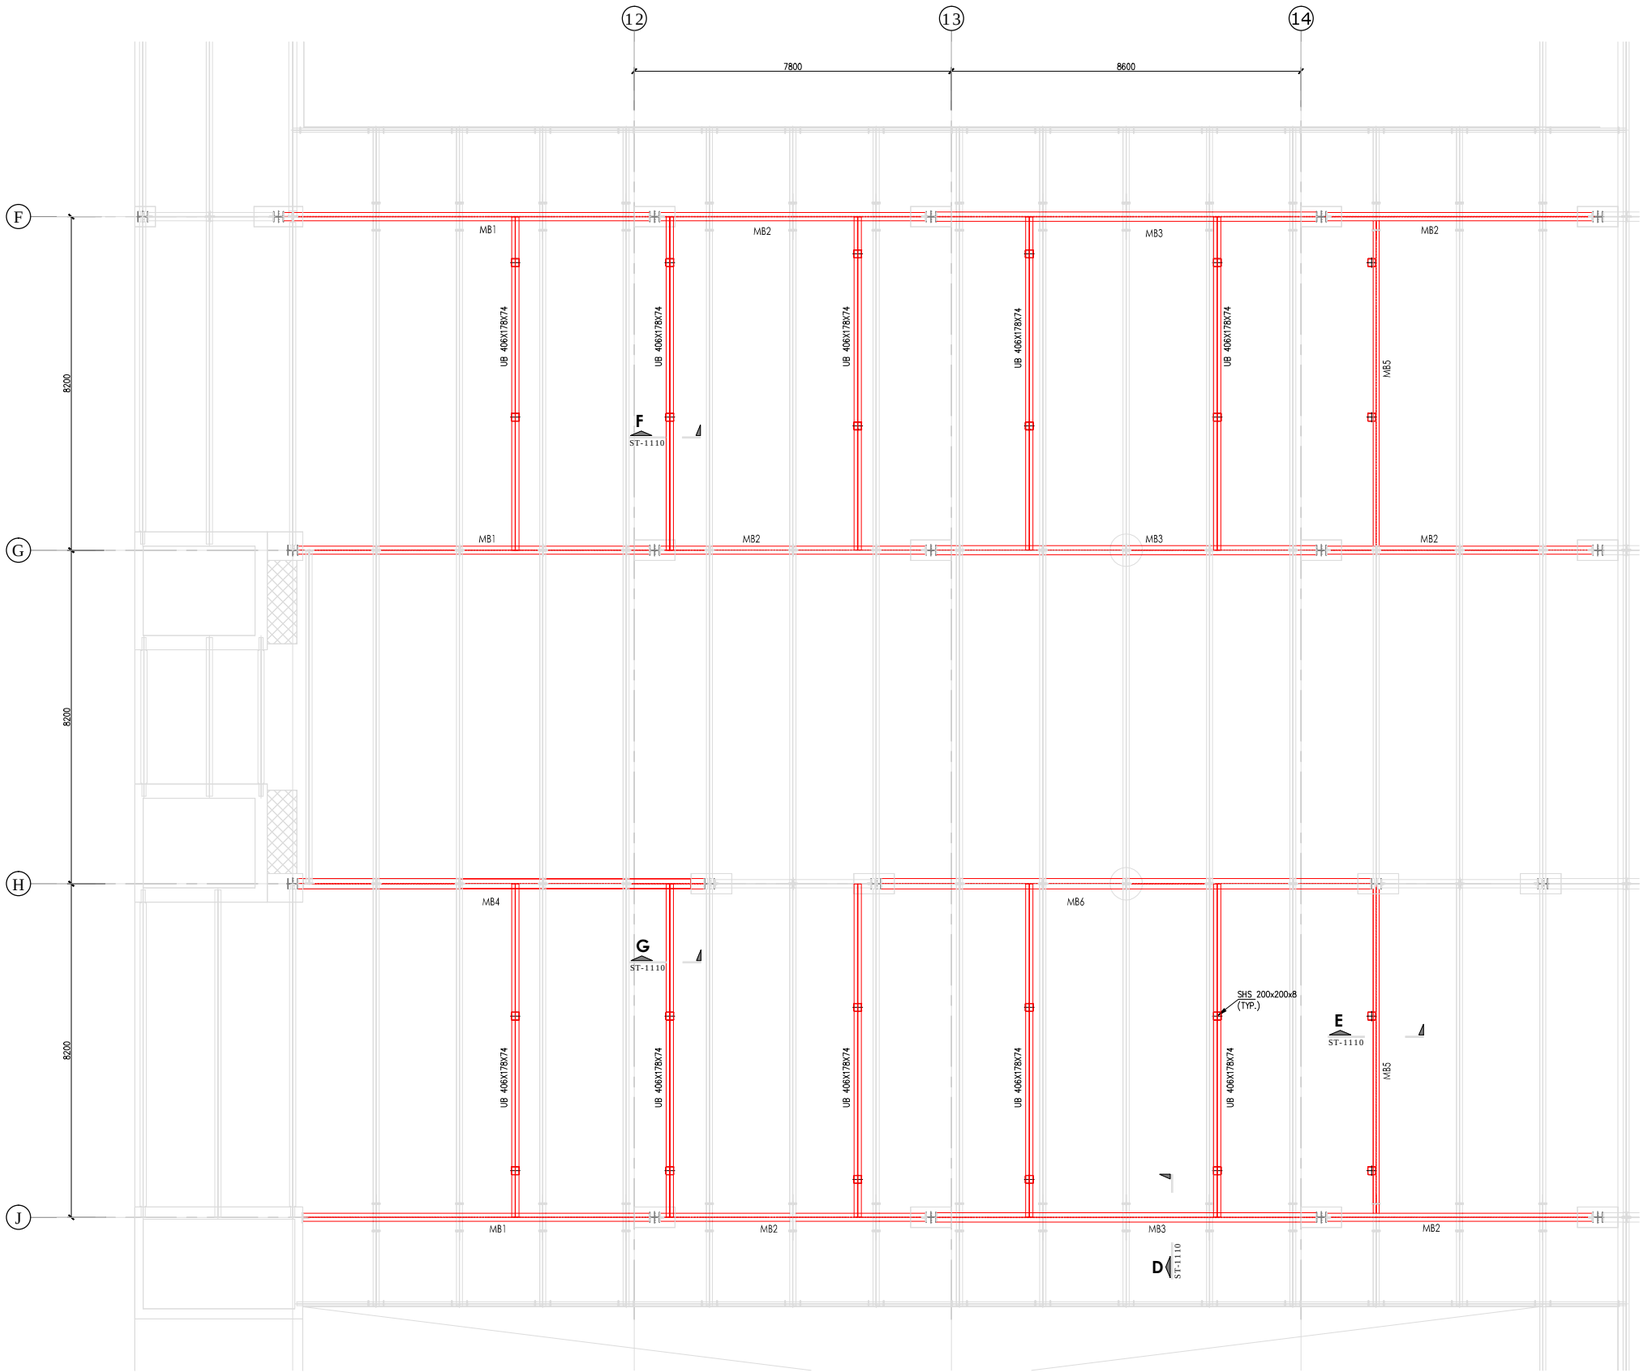



LEVEL-10 FRAMING LAYOUT

Sc: 1/75

NOTES

- ALL DIMENSION IN MM.
- DO NOT SCALE FROM DRAWING.
- THIS DRAWING TO BE READ IN CONJUNCTION WITH RELEVANT ARCH. STRUCTURAL & MEP. DETAIL AND SPECIFICATIONS. CONTRACTOR SHALL COORDINATE THESE DWG. WITH SITE CONDITION AND REPORT IF ANY DISCREPANCY FOR CLARIFICATION BEFORE PROCEEDING WITH THE WORK.
- ALL MATERIAL TO BE APPROVED BY ARCHITECT/ ENGINEER.
- CONTRACTOR SHOULD SUBMIT THE SHOP DRAWING FOR APPROVAL.

KEY PLAN

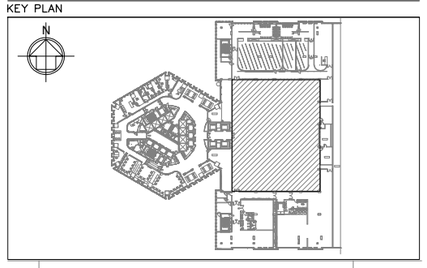

REV	DESCRIPTION	DATE
00	ISSUED FOR TENDER	12-APR-2026

REVISIONS

THIS DRAWING IS THE PROPERTY OF DSG AND SHALL NOT BE COPIED OR REPRODUCED IN ANY MANNER WITHOUT THE WRITTEN CONSENT OF DSG.

QR-Code	MUNICIPALITY STAMP

PREVIOUS BP No. :	83174	Application No :	M/2023/0001159
CONSULTANT REG. No :	M/42 GRADE : A	CONSULTANT REG. No :	000000 GRADE : A
CONSULTANT STAMP & SIGNATURE :		SUB-CONSULTANT STAMP & SIGNATURE :	
TECHNIQAL MANAGER :	N. JARROUJ	TECHNIQAL MANAGER	XXXX
REGISTRATION No. :	1195-A	REGISTRATION No :	XXXX

CONSULTANT

EGEC – QATAR
ENGINEERING CONSULTATION
P. O. Box: 21686 Doha – Qatar
Tel.: +974 44643135 Fax: 44653562
www.egec-xprt.com

CONSULTANT

ARCHITECTURAL
INT DESIGN
STRUCTURAL
ELECT MECH
SUPERVISION
MANAGEMENT
W L L

TEL +974 44521666 FAX +974 44363812 P.O. BOX 5785
Email info@mzandpartners.com www.mzandpartners.com

MZP WLL

CLIENT/DEVELOPER

QATAR ENERGY LNG

PROJECT

QATAR GAS HEADQUARTERS
(10TH FLOOR)
FIT-OUT AND ENHANCEMENT WORKS PROJECT

LOCATION: DOHA, QATAR | PIN NO.: -

SHEET TITLE

LEVEL-10 FRAMING LAYOUT

Project No.	Discipline	Date	Scale	Stage	Format
GP-25256	S	APRIL 2026	AS SHOWN	IFT	A1
		Drawn: DT	Checked: FH	Approved: FMI	
Originator: DSG	Drawing No.: ST-1101				Rev.No.: 00

THIS DRAWING MUST NOT BE USED FOR CONSTRUCTION UNLESS STAMPED AND SIGNED ISSUED FOR CONSTRUCTION AS APPROVED.

Plot Style Table : ---- Plot Device : None Page Setup : ---- Plot Date : Monday, March 30, 2026 12:00:36 PM File Name : ST-1101 - LEVEL-10 FRAMING LAYOUT.dwg Plotted By : Nithin Mathew