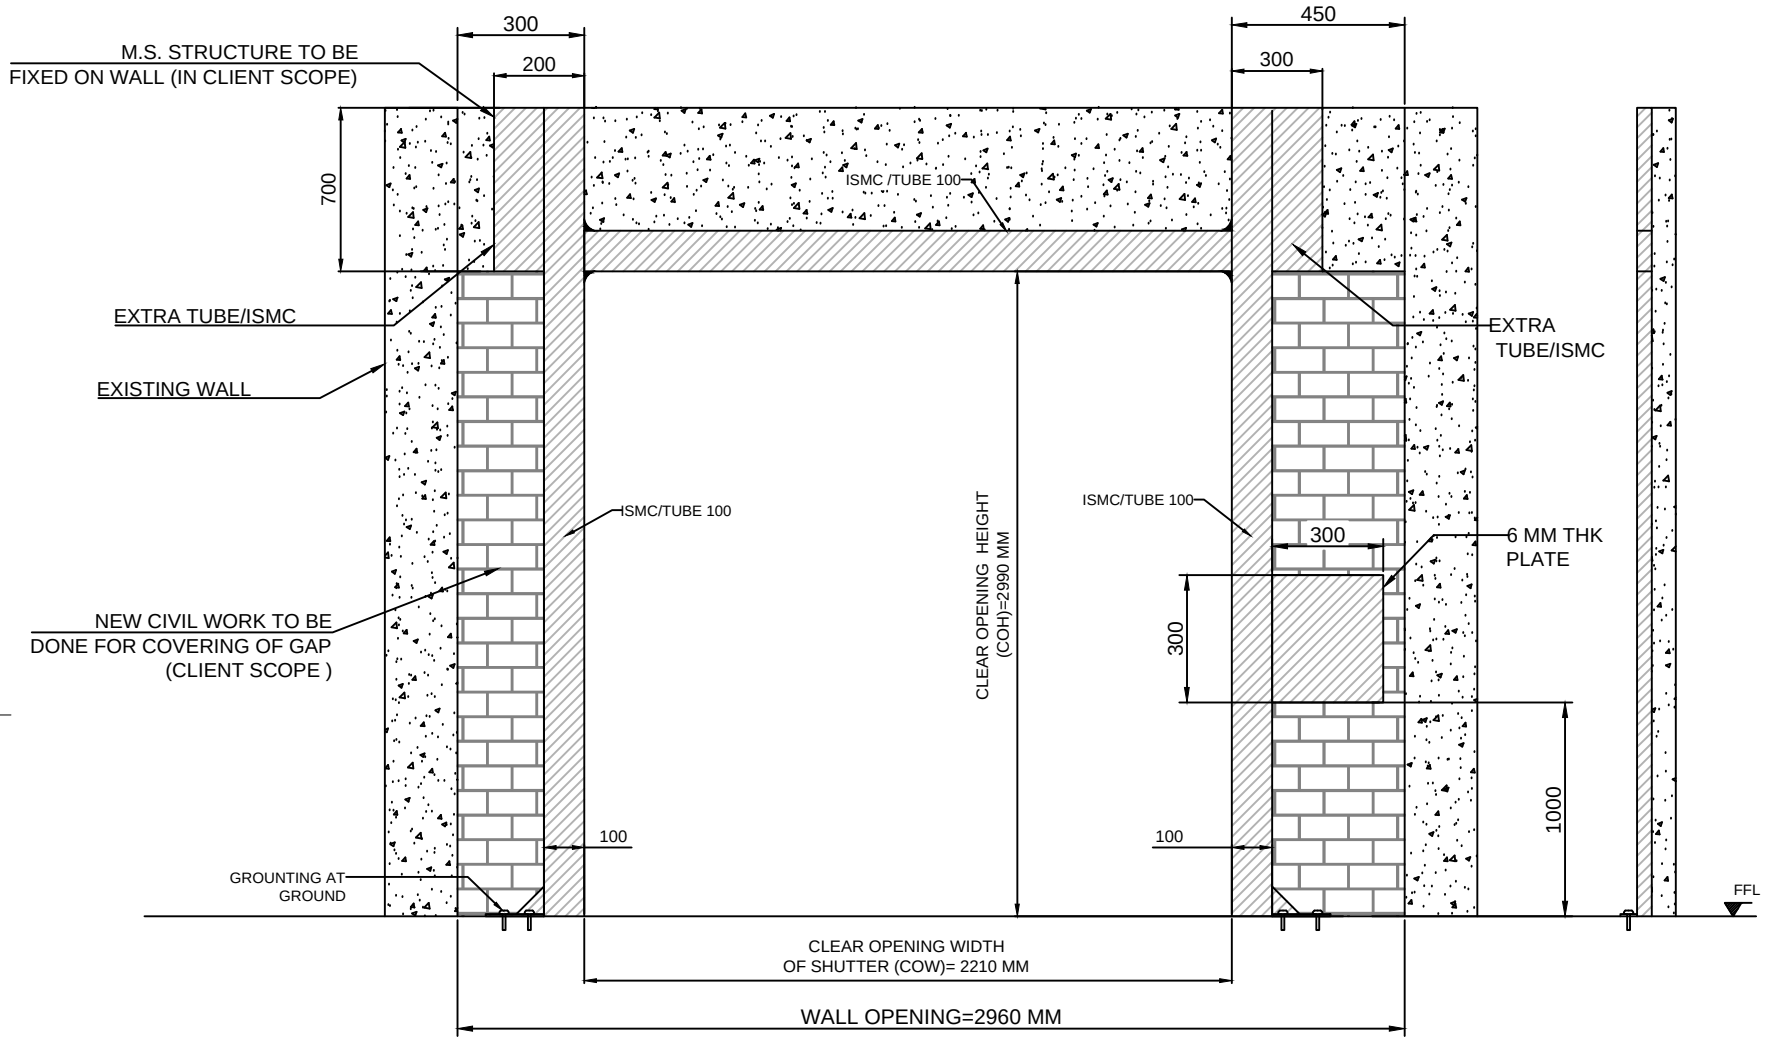


STRUCTURE

SR NO	CLEAR OPENING WIDTH(CW)	CLEAR OPENING HEIGHT(CH)	QTY	LOCATION
1	2210	2990	1	2

NOTES-
(1) MS STRUCTURE , FITTING & ALL CIVIL WORK IS IN CLIENT SCOPE.
(2) SHUTTER WILL BE ONLY INSTALLED AFTER READINESS OF STRUCTURE AS PER DRAWING PROVIDED.
(3) SPACE OF 700 mm ABOVE CLEAR HEIGHT IS REQUIRED FOR INSTALLATION OF GEAR OPERATED ROLLING SHUTTER.

TOLERANCE - ±10mm

This drawing & design is the property of NIHVA TECHNOLOGIES. Not to be sold or copied to any other concern.

TITLE M.S. STRUCTURE 2

NIHVA TECHNOLOGIES PVT. LTD.
Website:- www.nihva.com
NIHVA TECHNOLOGIES PVT. LTD. PUNE
Tel : 020 66304033
Email:- info@nihva.com

	NAME	SIGN	DATE
DRAWN	S.M.S.		11.1.2021
CHECK	V.T.		11.1.2021
APPRD.			

CLIENT - TRANS ENGG
PROJECT -
SITE LOCATION -
If any queries contact : design@nihva.com
DWG. NO. : NIHVA/20-21/0129
REV- R00
ALL DIMENSION ARE IN mm
SHEET: 02 OF 02