

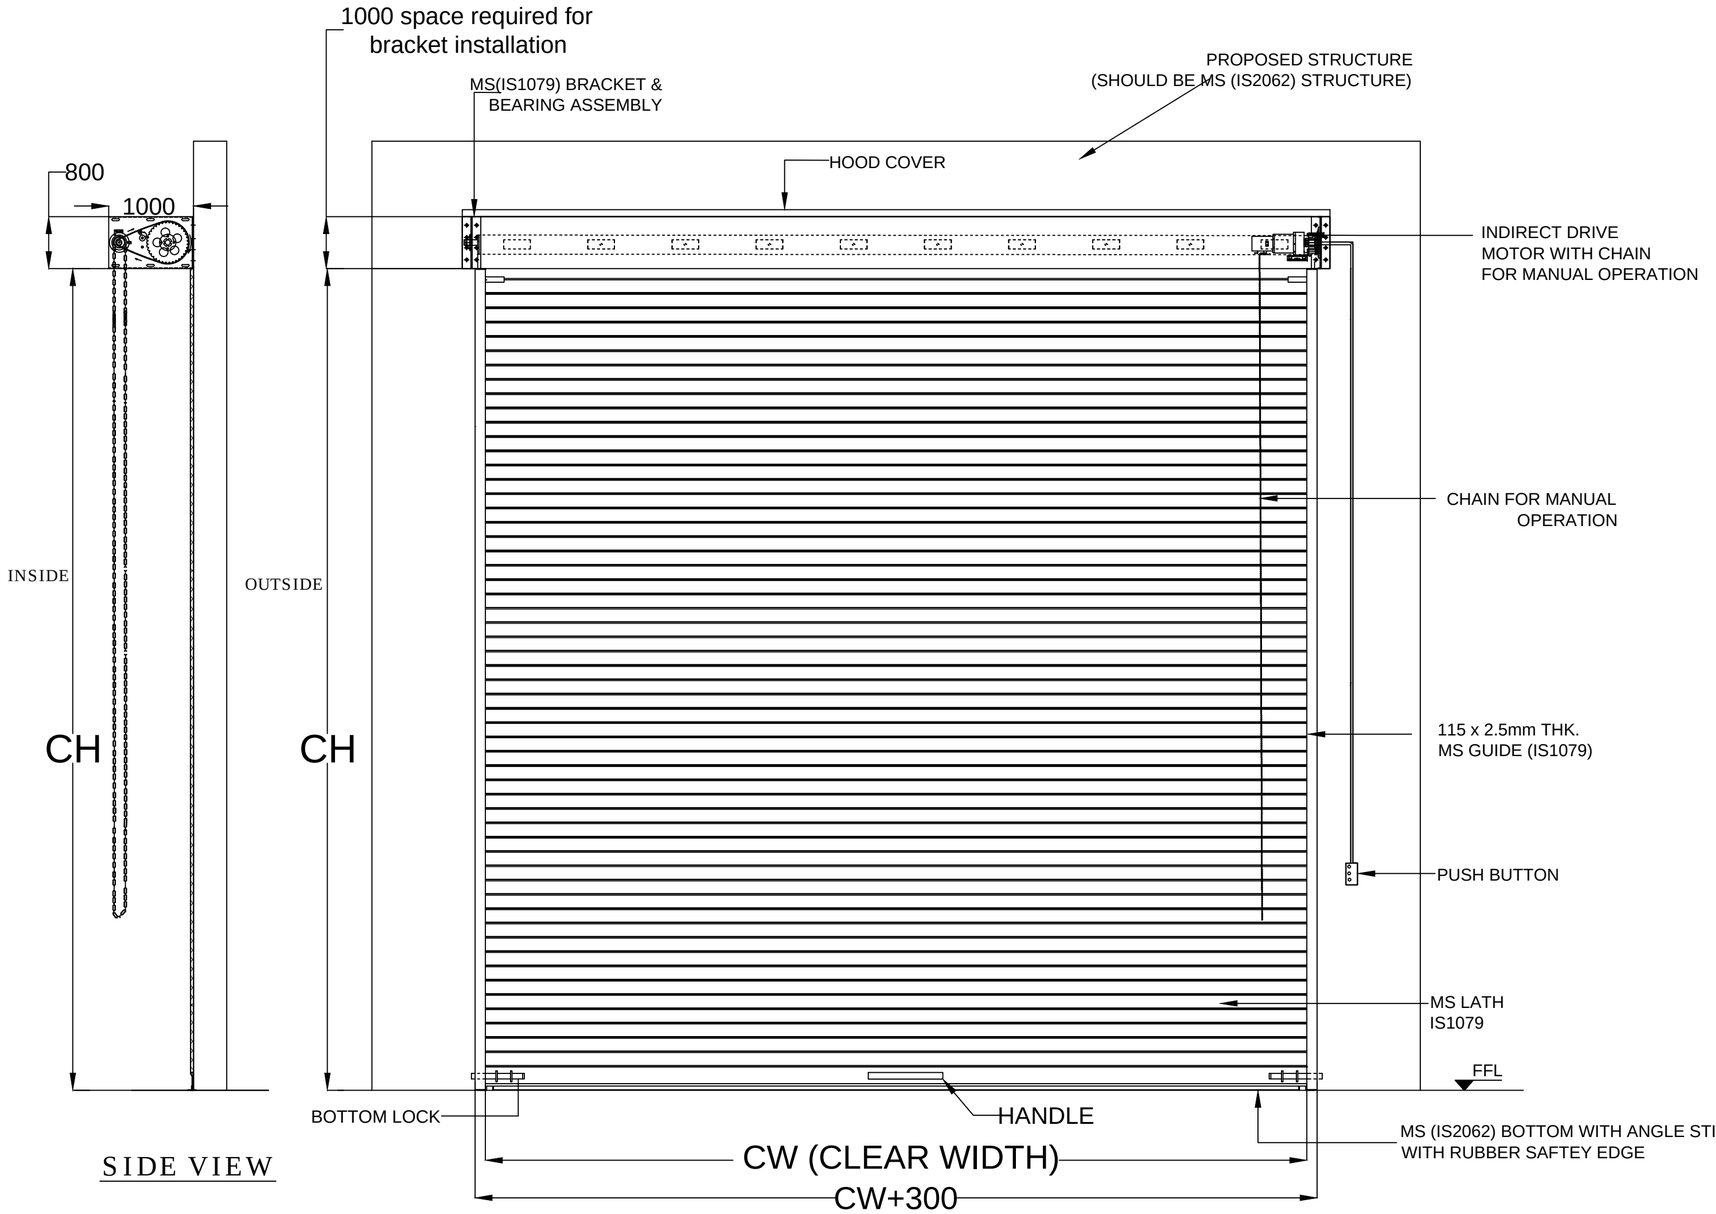


SIDE VIEW

ELEVATION

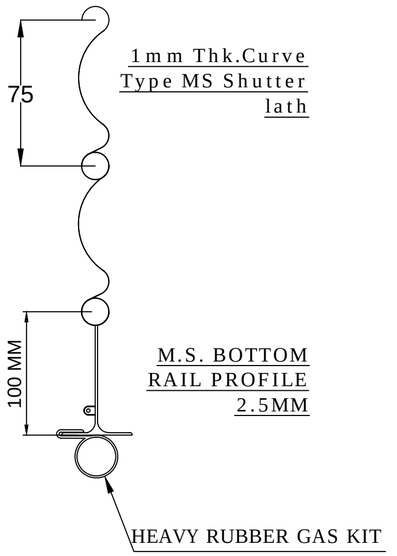


M.S. BOTTOM RAIL PROFILE 2.5MM

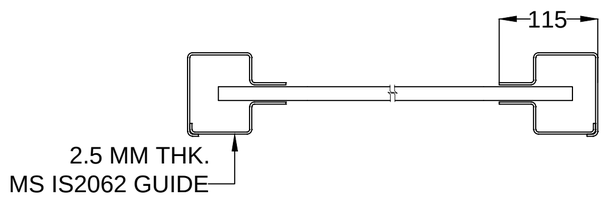

COLOR:- 1.RAL7035(LIGHT GRAY)
2.RAL9016(TRAFFIC WHITE)
3.RAL5005(SIGNAL BLUE)
4.RAL7004(SIGNAL GRAY)
5.RAL5015(SKY BLUE)

CLEAR WIDTH (CW)	CLEAR HEIGHT (CH)	QUANTITY
5000	6000	12

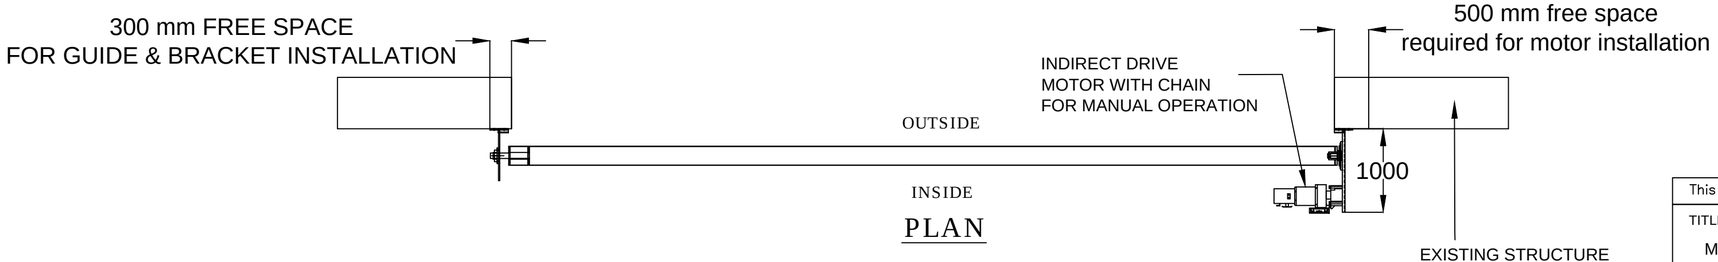

PLAN

Rev 01:- 04/02/2022
1.Added IS material specification for MS material.
2.Added motor capacity details.
3.Mentioned RAL code.

NOTE:-
1.REQUIRED STRUCTURE FOR ROLLING SHUTTER SHALL BE IN NIHVA SCOPE.
2. ALL REQUIRED CIVIL WORK IN CLIENT SCOPE.
3. 3 PHASE POWER SUPPLY SHOULD BE PROVIDED BY CLIENT.
4. MOTOR : JIELONG , 1 TON, 3PH

This drawing & designing is the property of NIHVA TECHNOLOGIES. Not to be sold or copied to any other concern.

TITLE
MOTORIZED ROLLING SHUTTER

NIHVA TECHNOLOGIES PVT. LTD.
NIHVA TECHNOLOGIES PVT. LTD. PUNE
Tel : 020 66304033
Email:- info@nihva.com
Website:- www.nihva.com

	NAME	SIGN	DATE	
DRAWN	G.P.		13/09/21	CLIENT - REWARD CONSTRUCTION
CHECK	A.K.		13/09/21	PROJECT -
APPROVAL	V.T.		13/09/21	SITE - INDAPUR

If any queries contact : design@nihva.com | DWG. NO. : NIHVA/21-22/0232 | REV. - 01
ALL DIMENSION ARE IN mm | SCALE: NTS | WT: | SHEET: 01 OF 01