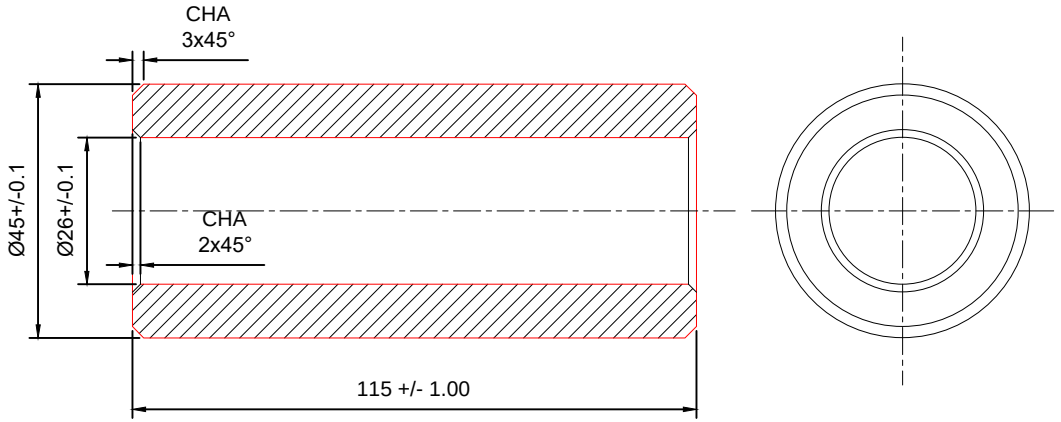



NOTE:~ MTL : MS

BUSH Ø45 X 118L = 18 NOS

NOTE : ~ PLEASE MAINTAIN 7 MM GAP BETWEEN TWO LIP BUSHES.

This drawing & design is the property of NIHVA TECHNOLOGIES. Not to be sold or copied to any other concern.

TITLE

LIP MOUNTING BUSH

NIHVA TECHNOLOGIES PVT. LTD.

NIHVA TECHNOLOGIES PVT. LTD. PUNE
Tel : 020 66304033
Email:- info@nihva.com
Website:- www.nihva.com

| | NAME | SIGN | DATE |
|---|---|---|---|
| DRAWN | PRADEEP | | 02.05.2018 |
| CHECK | PRADEEP | | 02.05.2018 |
| APPRD. | PRADEEP | | 02.05.2018 |

If any queries contact : design@nihva.com

ALL DIMENSION ARE IN mm

CLIENT -

PROJECT - DLIK1005

SITE LOCATION -

DWG. NO. : NIHVA/18-19/DLIK1005_009

SCALE: NTS | WT: | REV- 0