


PRODUCED BY AN AUTODESK EDUCATIONAL PRODUCT

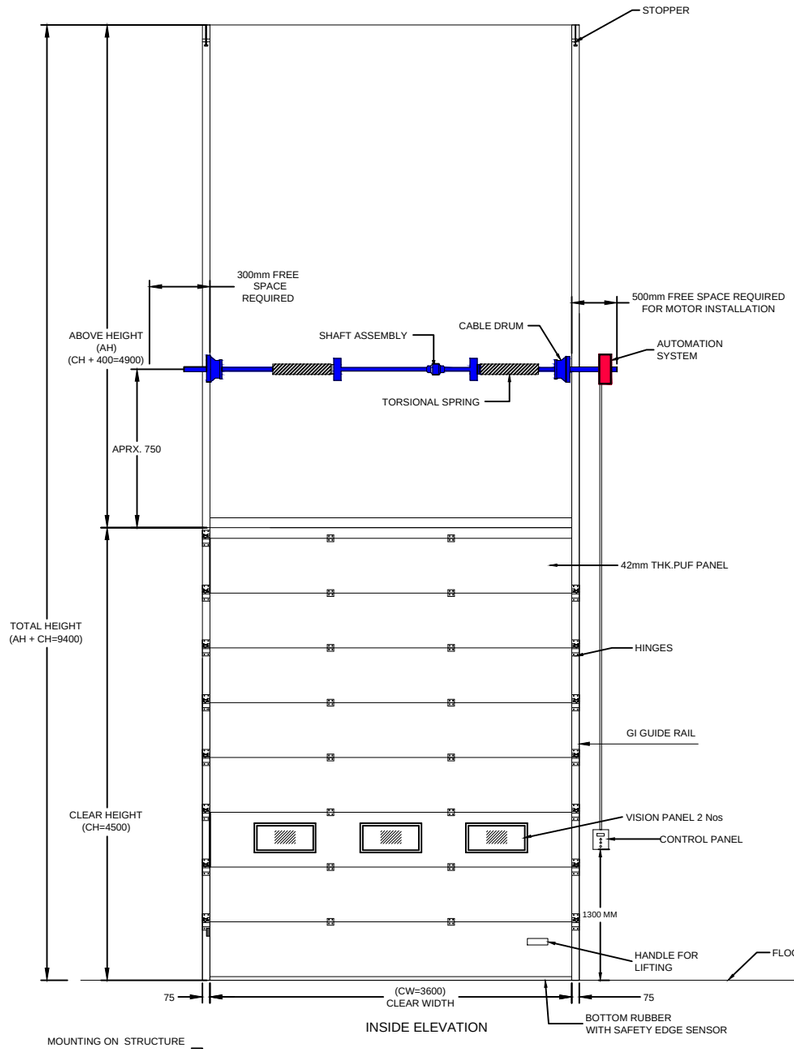


INSIDE ELEVATION

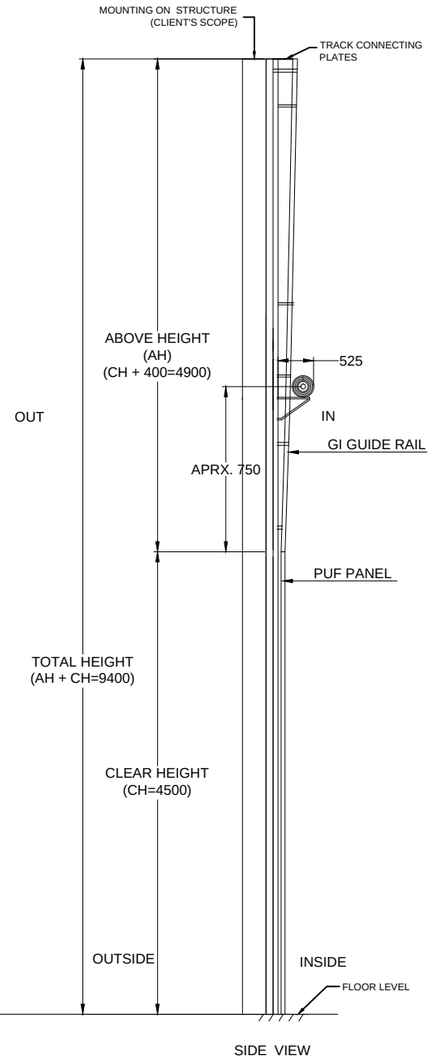

SIDE VIEW

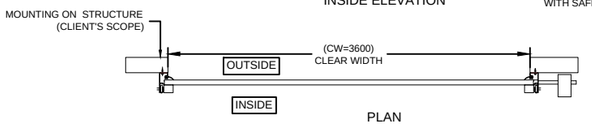

PLAN

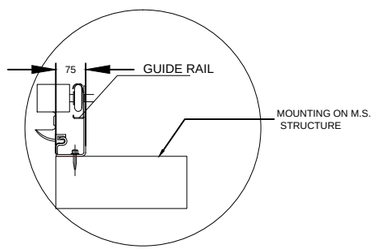

TRACK DETAILS

DIMENSION :

CLEAR WIDTH (CW)	CLEAR HEIGHT (CH)	QUANTITY
3600 mm	4500 mm	1 NOS

TECHNICAL DATA :

COMPONENTS	MATERIALS	SPECIFICATIONS
DOOR PANELS	GI & PUF	42 mm CFC- FREE POLYURETHANE WITH 0.5mm THK, GI PRECOATED PANELS.
DOOR HINGE	———	HEAVY DUTY HINGES FOR INTERLOCKING OF PANELS
SHAFT ASSEMBLY	STD.	TORSIONAL SPRING WITH SHAFT & BEARING PLATES
FINISH		PANELS ARE IN STANDARD RAL 9002 GREY WHITE COLOR

ACCESSORIES-
1. SAFETY EDGE SENSOR.

IMPORTANT NOTES:
1. REQUIRED STRUCTURE FOR DOOR IS IN CLIENT'S SCOPE.
2.SINGLE PHASE POWER SUPPLY REQUIRED AT DOOR LOCATION.
3.ALL CIVIL WORK IS IN CLIENT'S SCOPE.

NIHVA TECHNOLOGIES PVT. LTD. PUNE
Email:- info@nihva.com
Website:- www.nihva.com

TITLE:

VERTICAL LIFTING SECTIONAL DOOR
RS05. East Side Upper Dock

CLIENT'S APPROVAL :

CLIENT - AJAY KALE AND ASSOSIATES

PROJECT -

SITE LOCATION - PIRANGUT

DWG. NO. : NIHVA/21-22/CLT/281	REV- 00
SCALE: NTS	WT:	SHEET:01 OF 02

	NAME	DATE	SIGN
DRAWN	G.I.P.	23.12.2021	
CHECK	A.K.	23.12.2021	
APPROVAL			

If any queries contact : design@nihva.com

NOTE: ALL DIMENSIONS ARE IN mm

Rev.no	Revision	Revised BY	Date
1.	Mentioned title name RS05	Sujata	28/12/2021


THIS DRAWING & DESIGNING IS THE PROPERTY OF NIHVA TECHNOLOGIES. NOT TO BE SOLD OR COPIED TO ANY OTHER CONCERN.

PRODUCED BY AN AUTODESK EDUCATIONAL PRODUCT

PRODUCED BY AN AUTODESK EDUCATIONAL PRODUCT

PRODUCED BY AN AUTODESK EDUCATIONAL PRODUCT

PRODUCED BY AN AUTODESK EDUCATIONAL PRODUCT

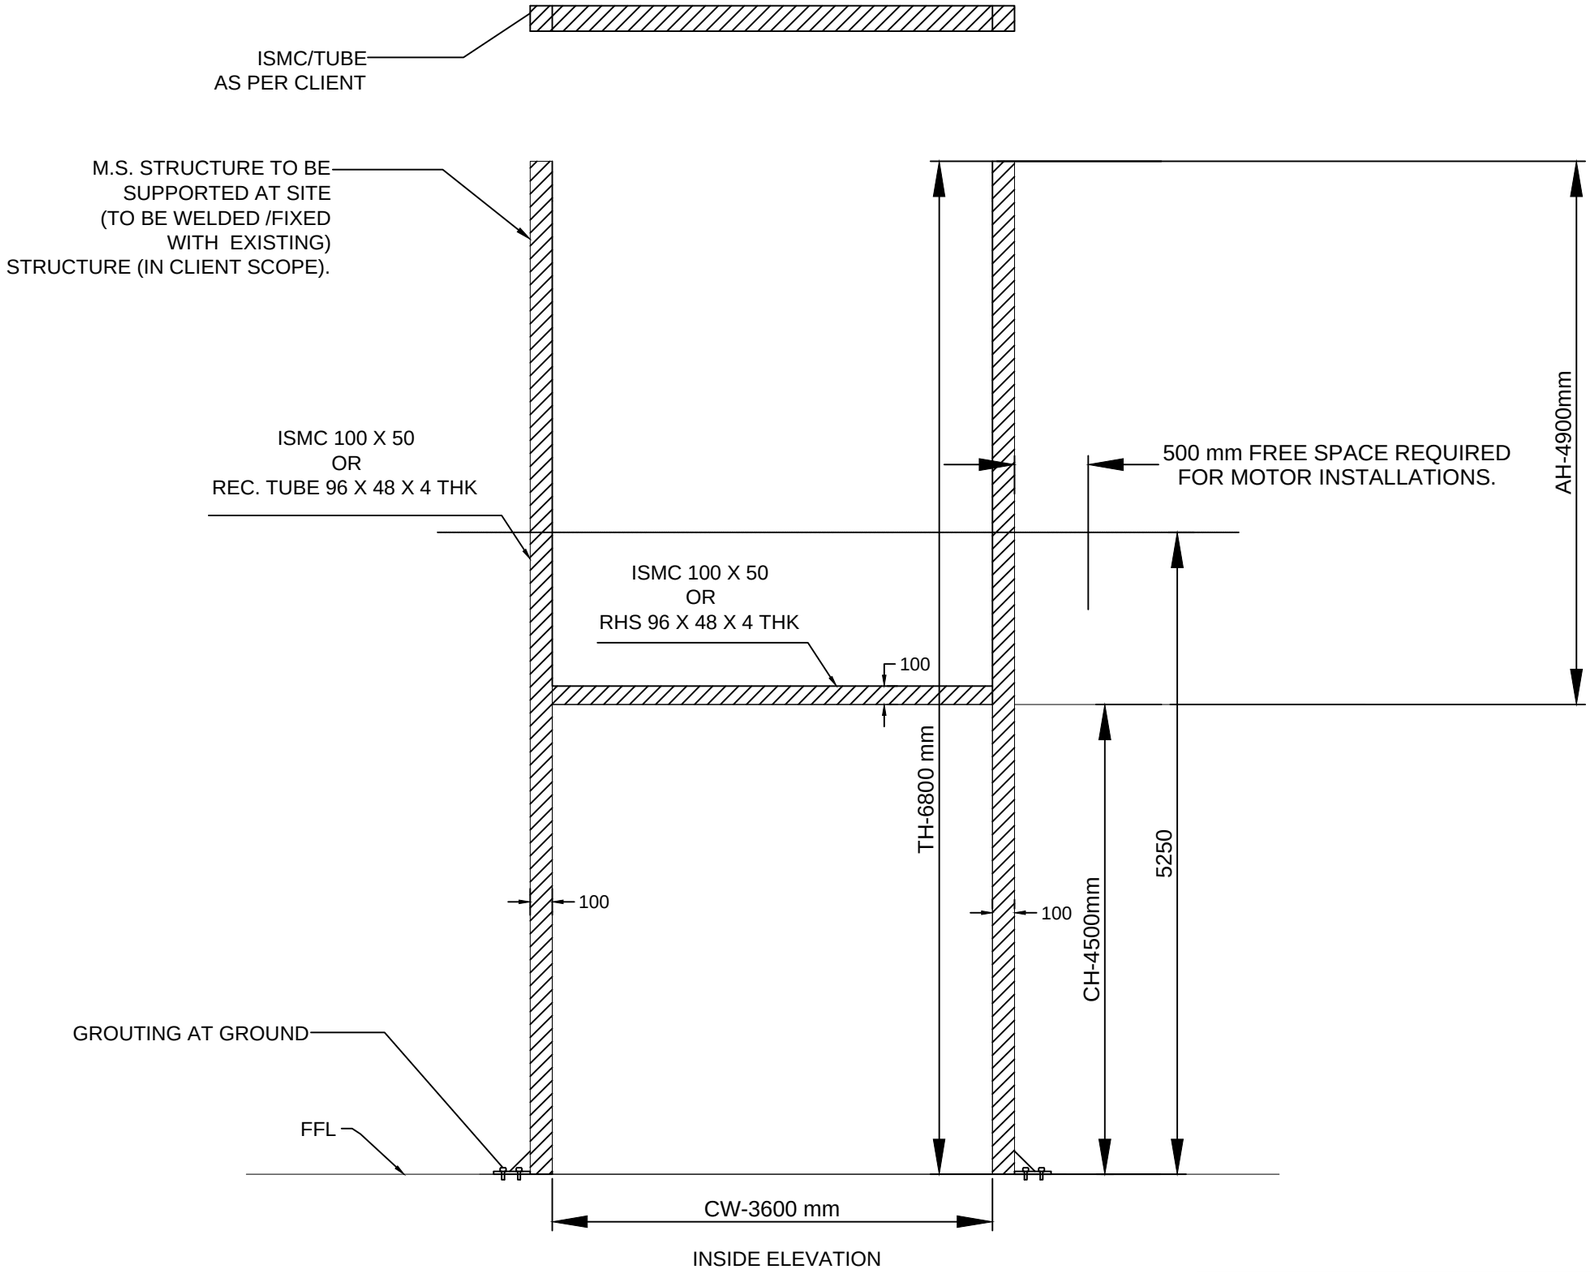

INSIDE ELEVATION

SR NO	CLEAR WIDTH CW	CLEAR HEIGHT CH	AH	QTY
1	3600 mm	4500mm	4900	1 nos

NOTES-
(1) REQUIRED M.S. STRUCTURE , FITTING & ALL CIVIL WORK IN CLIENT SCOPE .
(2) PRODUCT WILL BE INSTALLED AFTER READINESS OF STRUCTURE AS PER DRAWING.

This drawing & design is the property of NIHVA TECHNOLOGIES. Not to be sold or copied to any other concern.

TITLE: STRUCTURE FOR SECTIONAL DOOR

NIHVA TECHNOLOGIES PVT. LTD.
NIHVA TECHNOLOGIES PVT. LTD. PUNE
Tel : 020 66304033
Email:- info@nihva.com
Website:- www.nihva.com

	NAME	SIGN	DATE
DRAWN	G.P.		23.12.2021
CHECK	A.K.		23.12.2021
REV.			
APPROVAL			

CLIENT -AJAY KALE AND ASSOSIATES
PROJECT -
SITE LOCATION -
DWG. NO. : NIHVA/21-22/CLT/281
SCALE: NTS | WT: | SHEET: 02 OF 02

If any queries contact : design@nihva.com

ALL DIMENSION ARE IN mm

PRODUCED BY AN AUTODESK EDUCATIONAL PRODUCT

PRODUCED BY AN AUTODESK EDUCATIONAL PRODUCT

PRODUCED BY AN AUTODESK EDUCATIONAL PRODUCT