

THIS PRINT IS THE PROPERTY OF NIHVA IT IS TO BE USED ONLY FOR THE PURPOSE FOR WHICH IT WAS LENT AND MUST NOT BE USED IN ANY WAY DERTIMENTAL TO THE INTEREST OF THIS COMPANY AND IS SUBJECT TO RETURN ON DEMAND.

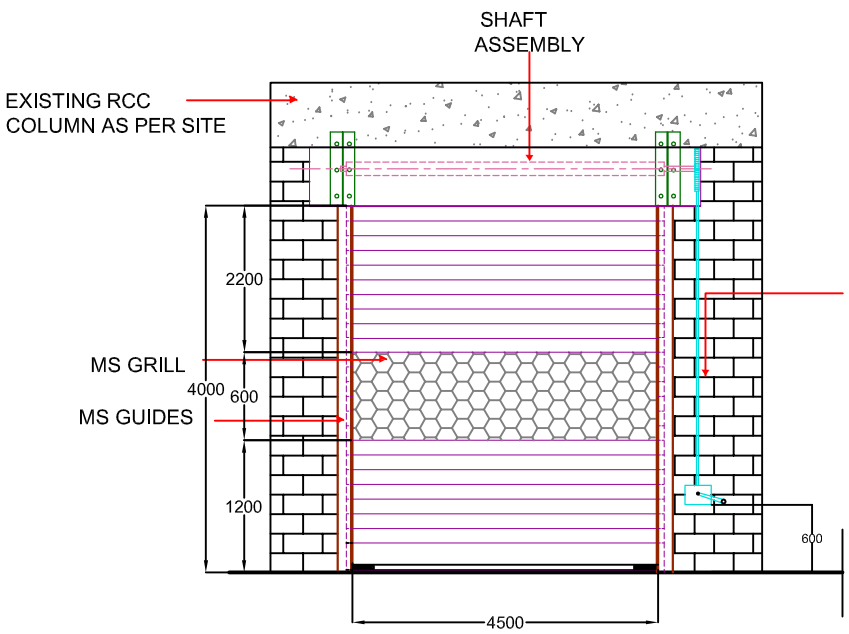


INSIDE ELEVATION


Clear Opening size:-
(W)4.5 mx(H)4.0m

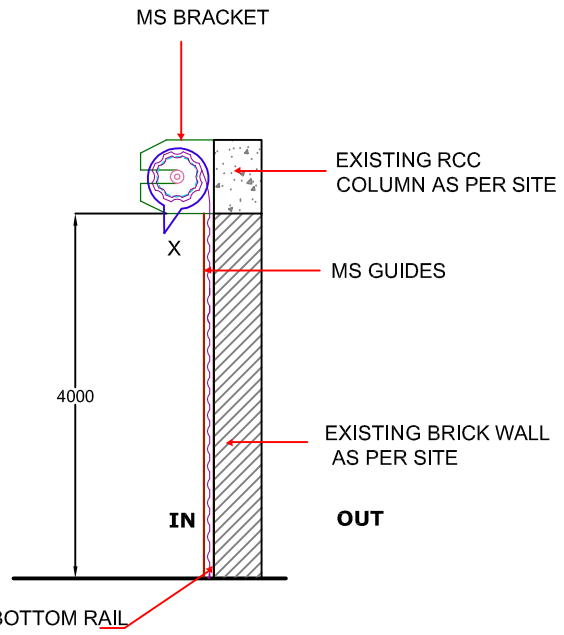


SIDE VIEW

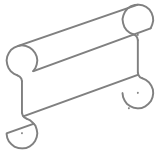

Box/Straight Type Slat Profile

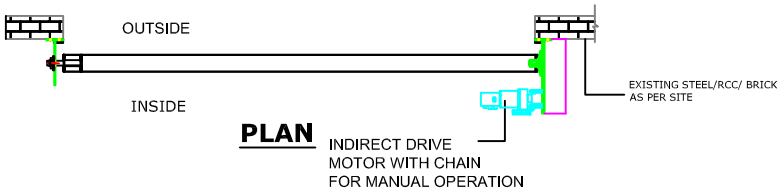

PLAN

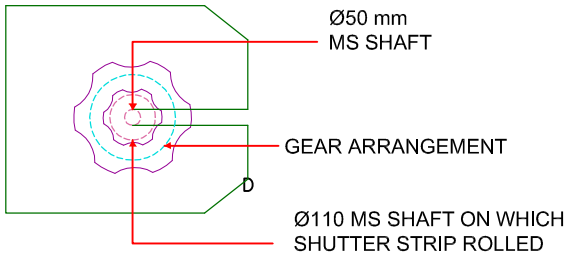

Bracket



Side guide

TITLE: Manual Gear Operated Rolling Shutter	DO NOT SCALE DRAWING		NIHVA TECHNOLOGIES PVT. LTD. Pune:-411044 Tel :- 020 66304033 Email :- info@nihva.com
		SIGN	DATE	
CLIENTS APPROVEL:–	DRAWN			CLIENT: Shapoorjl Palonjl Co. Ltd
	CHECK			PROJECT / SITE: GE,CHAKAN
	ENG			PRODUCT NAME:
UNLESS & OTHERWISE SPECIFIED DIMENSION ARE IN M.M.	APPRD.			DWG. NO.: NVA/SP/03R
	PROD			REV.: 0
	MFG			SCALE: NTS WT: SHEET: 1 OF 1
	Ref. No.			