




SIDE VIEW

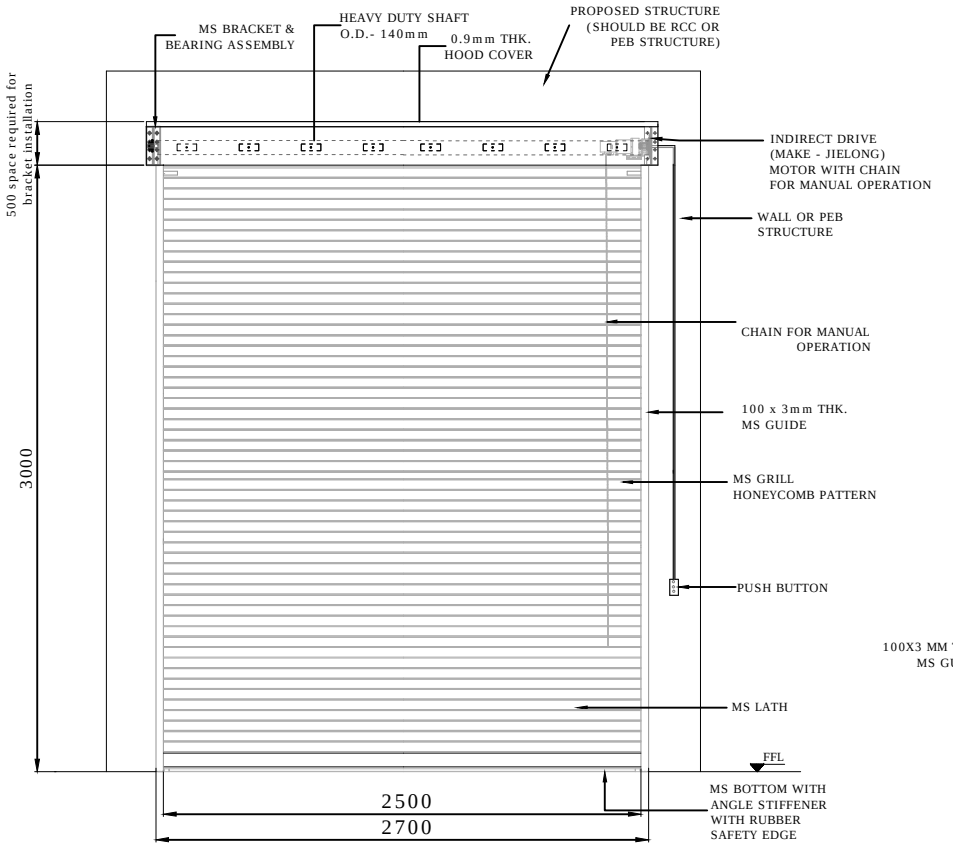


ELEVATION

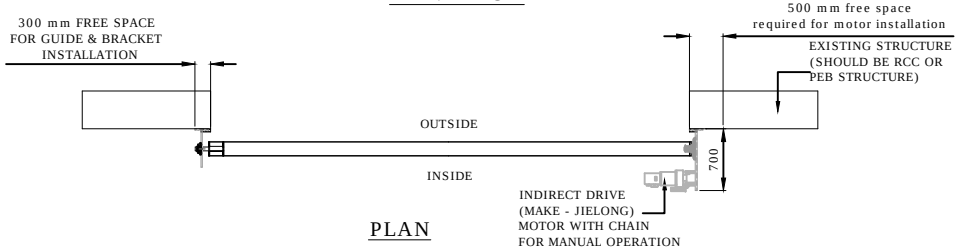

PLAN

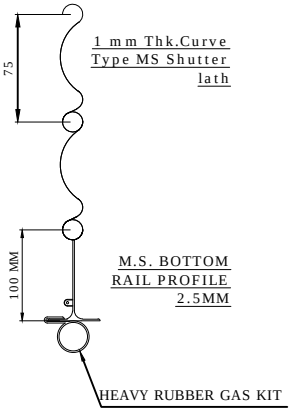

M.S. BOTTOM RAIL PROFILE 2.5MM

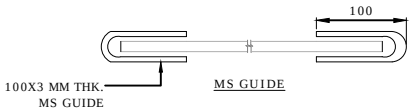

SHUTTER SPEED- APPROX. 0.05m/s

SHUTTER TYPE	CLEAR WIDTH (CW)	CLEAR HEIGHT (CH)	GUIDE SIZE	BRACKET SIZE	SHAFT SIZE (O.D)	QUANTITY	LOCATION
RSD	2500	3000	100X3mm	375X375X5mm	140mm	5	MAIN BUILDING

DIMENSION :

CLEAR WIDTH	CLEAR HEIGHT	QUANTITY
2500	3000	05 NOS

MATERIAL:

THICKNESS :

NOTE:
1.REQUIRED STRUCTURE FOR ROLLING SHUTTER WILL BE CLIENT'S SCOPE.
2.SINGLE PHASE. 3 CORE 1.5 SQ. CABLE REQUIRE AT SITE(CLIENT'S SCOPE)
3. SHUTTER WILL BE POWDER COATED CLIENT SHOULD CONFIRM RAL COLOR SHADE.

REV NO	DATE	DESCRIPTION
REV 0	29-11-17	INITIAL DRAWING

NIHVA TECHNOLOGIES PVT. LTD.
NIHVA TECHNOLOGIES PVT. LTD. PUNE
Email:- info@nihva.com
Website:- www.nihva.com

TITLE:

MOTORIZED ROLLING SHUTTER 2.5X3m

CLIENT'S APPROVAL :

CLIENT - SCON PROJECTS

PROJECT -ENZENE BIOSCIENCES LTD.

SITE LOCATION - CHAKAN.

DWG. NO. : NIHVA/17-18/0296 | REV.:- 0

SCALE: NTS | WT: | SHEET:1 OF 1

		DATE	SIGN.
DRAWN	SURAJ	29-11-2017	
CHECK	OMKAR	29-11-2017	
APPRD	SHEKHAR	29-11-2017	

If any queries contact : projects@nihva.com

NOTE: ALL DIMENSIONS ARE IN mm

THIS DRAWING & DESIGN IS THE PROPERTY OF NIHVA TECHNOLOGIES. NOT TO BE SOLD OR COPIED TO ANY OTHER CONCERN.