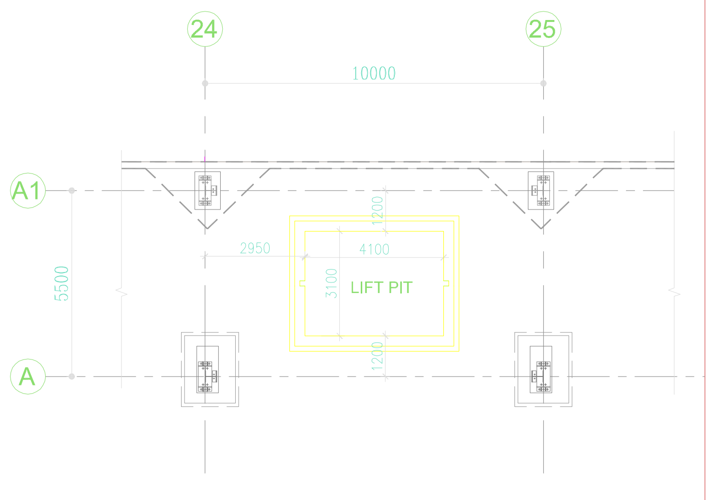

PART PLAN OF FACTORY L.E.B

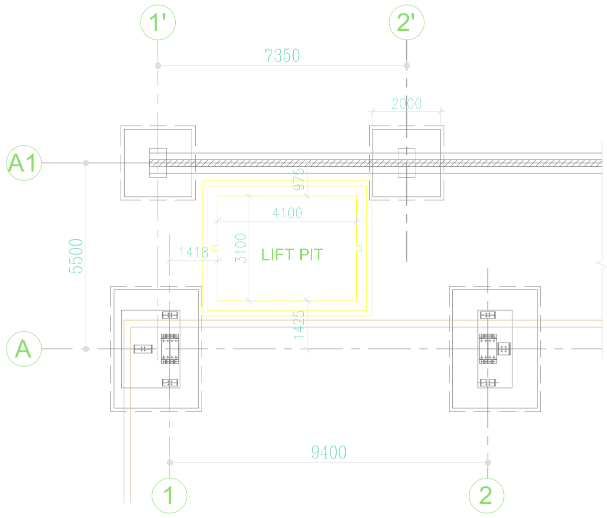

PART PLAN OF FACTORY H.E.B

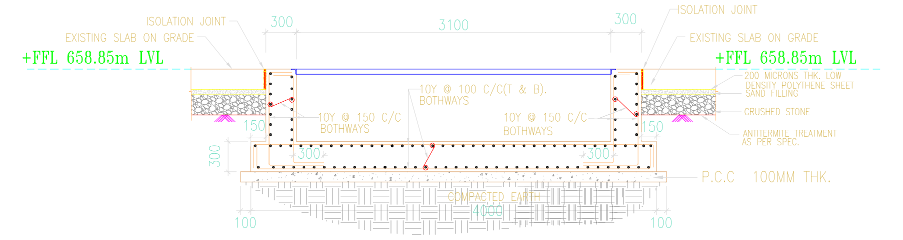

SECTION 2-2

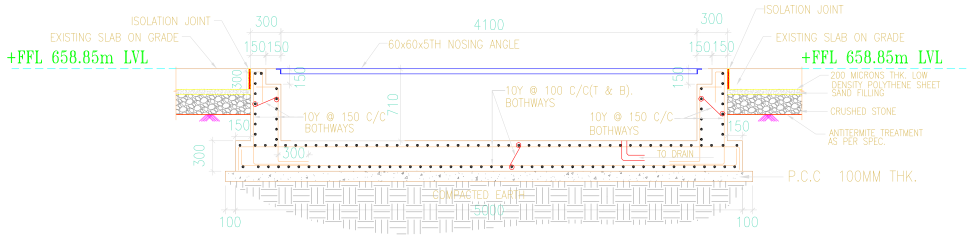

SECTION 1-1

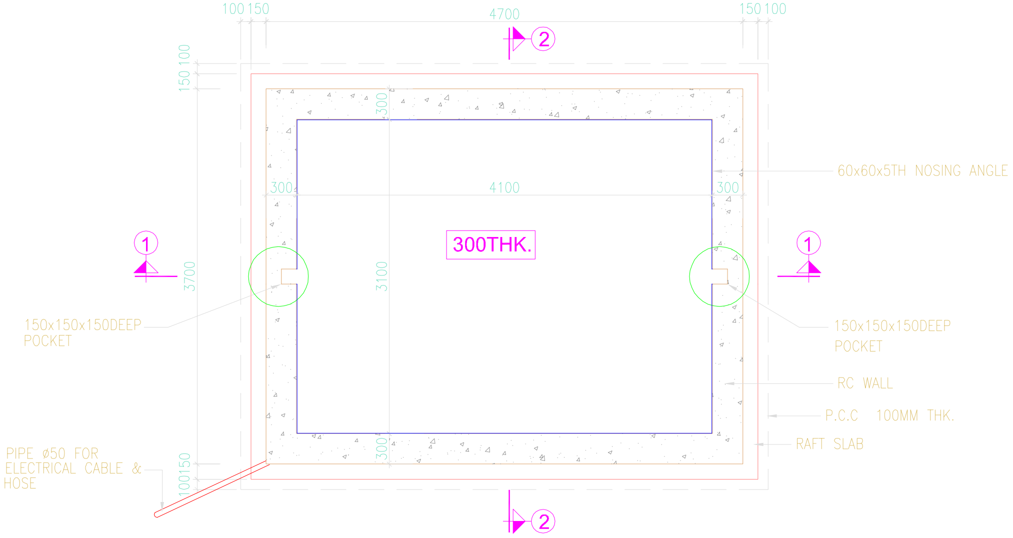

PLAN OF LIFT PIT

1. THIS DRAWING IS PREPARED BASED ON INPUT RECEIVED FROM THE VENDOR " NIHVA TECHNOLOGIES PVT. LTD, PUNE - ELECTRO HYDRAULIC SCISSOR LIFT PIT DRAWING DATED: 02.04.2014 REV.-R0"
2. THIS DRAWING SHOULD BE READ ALONG WITH VENDOR SHOP DRAWING . ANY DISCREPENCIES FOUND SHOULD BE BROUGHT TO THE NOTICE OF ARCHITECT BEFORE EXECUTION AT SITE.
3. THE LOCATION OF THE LIFT PIT SHOULD BE CONFIRMED BY THE CLIENT BEFORE EXECUTION AT SITE.

KEY PLAN:
(NOT TO SCALE)

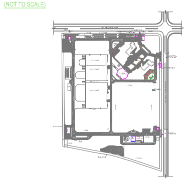

GENERAL NOTES :

1. ALL DIMENSIONS ARE IN MM
2. THIS DRG SHOULD BE READ IN CONJUNCTION WITH RESPECTIVE ARCH.DRG
3. CLEAR COVER
   RC WALL - 35MM
   RAFT - 50MM
4. CONCRETE MIX M25
5. GRADE OF STEEL = Fe500
6. LAP LENGTH OF ALL BARS SHOULD BE 50 TIMES THE DIA OF THE BAR
7. ALL LEVELS ARE IN METRES AND ARE UNFINISHED LEVELS UNLESS OTHERWISE SPECIFIED.
8. DO NOT SCALE DRAWINGS. ONLY WRITTEN DIMENSIONS SHALL BE FOLLOWED, ANY DISCREPANCIES NOTED SHALL BE BROUGHT TO THE THE ARCHITECT PRIOR TO EXECUTION.

REV.	DESCRIPTION	DATE	BY	CHD.
R1	ISSUED FOR CONSTRUCTION	17.04.14	SAJ	SD

AMENDMENT

GRAPHIC SCALE:

PROJECT MANAGER:

CLIENT:
GE India Industrial PVT LTD
Chakan, Pune.

PROJECT:
PROPOSED MULTIMODAL CAMPUS FOR
M/s. GE INDIA INDUSTRIAL PVT.LTD

DRAWING TITLE:
FACTORY - SCISSOR LIFT
LAYOUT & RC DETAILS OF LIFT PIT

SCALE : 1:100 (A1)
DATE : 16.04.14
DRAWN : Arockiamary.S
CHKD : Dhanalakshmi.S
APRD : Shankar.J

DRAWING NO:
GE-P-FAC-ST11-01-03-178612

R1

ARCHITECTURE ∘ INTERIOR DESIGN ∘ ENGINEERING ∘ PLANNING ∘ CONSTRUCTION MANAGEMENT

CRN
C R NARAYANA RAO
10, KARPAGAMBAL NAGAR,
MYLAPORE, CHENNAI-600 004

B.Arch. (Hons.), M.Arch., (Calif.), F.I.I.A., Intl.Assoc.A.I.A.,
Registered Architect.

FACTORY

Construction work shall be executed only as per the latest revision drawing. Once a revision drawing is issued, the validity of the previous revision drawing stands cancelled and as such construction shall not be carried out as per superseded revisions. The Contractor is expected to:
1. Maintain a register of Drawing Receipts, listing drawing number & revision number, title, from whom received, date received, number of copies received, details of transmittal from the issuer & any other relevant details to be advised from time to time.
2. Archive all previous revision issues immediately upon receipt of a new revision and no superseded drawing shall remain in the site of works except in the Contractor's archives for record and reference purposes only.
3. While archiving superseded drawing, the Contractor is expected to stamp all previously issued drawings / prints appropriately, mentioning the date and revision number of the new revision on account of which the previous revision is archived.
4. The Contractor shall allow the representative of Client / PMC / Architect to inspect Contractor
5. Any work carried out by the Contractor using a superseded drawing after the issue of a new revision is liable for rejection and reinstatement as per new revision at Contractor's risk and cost without any entitlement to extension of time

THESE DRAWINGS ARE UNDER COPYRIGHT AND ARE THE PROPERTY OF ---. NONE OF THE DRAWINGS AND RELATED DOC--UMENTS CAN BE REPRODUCED, COPIED IN WHOLE OR IN PART WITHOUT PRIOR EXPRESSED WRITTEN CONSENT OF ---. THESE DRAWINGS CANNOT BE HANDED OVER TO A THIRD PARTY OR USED FOR ANY PURPOSE, OTHER THAN THAT FOR WHICH IT HAS BEEN LOANED. AFTER FULFILLING THE PURPOSE OF ISSUE THE DRAWINGS SHALL BE RETURNED TO ---.