

Revision		Date	By
A	Corrected mullion hoist positions, floor pits altered	2022-09-02	EB
B	New measurements, doors redrawn	2022-10-11	EB

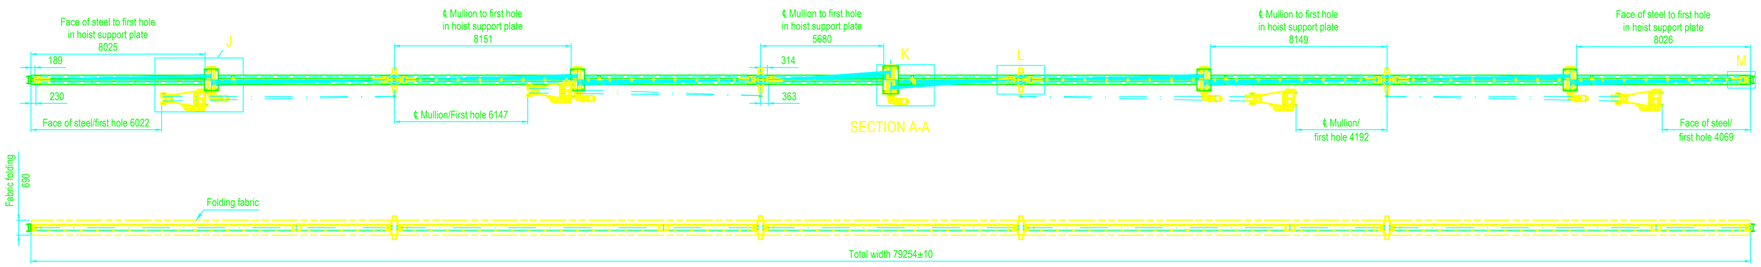


SECTION A-A


SECTION B-B

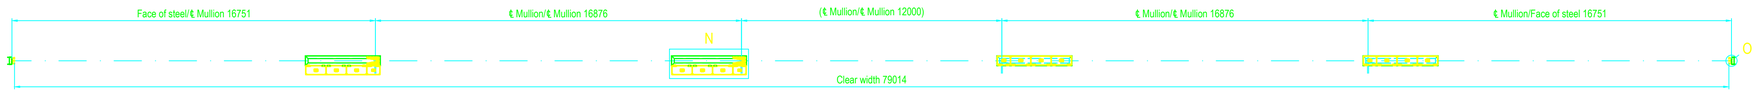


SECTION C-C

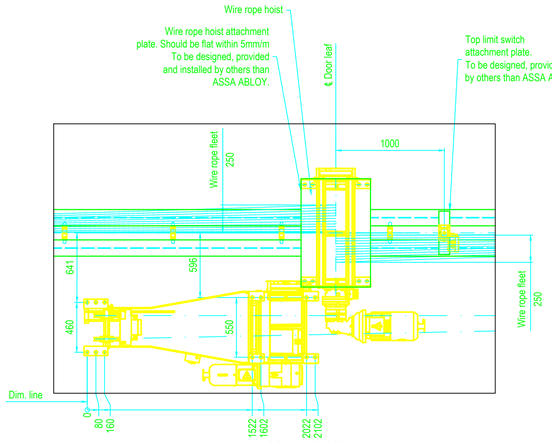


DETAIL J, SCALE (1:20)

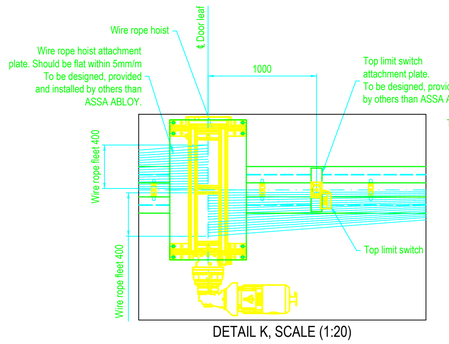


DETAIL K, SCALE (1:20)

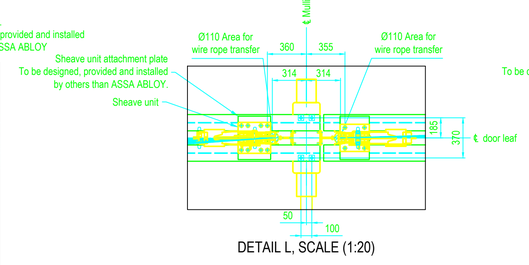


DETAIL L, SCALE (1:20)

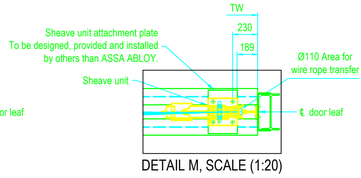

DETAIL M, SCALE (1:20)

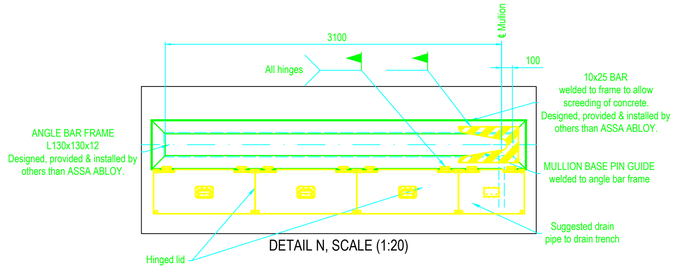

DETAIL N, SCALE (1:20)

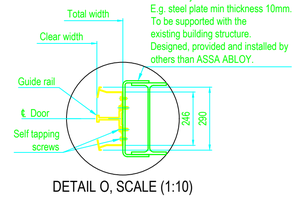

DETAIL O, SCALE (1:10)

DOOR IDENTITY NUMBER: 84800001

LOAD DIAGRAM & NOTES, ref. to drwng. no. 77446

INTERFACE, SECTIONS ref. to drwng. no. 77445

INTERFACE, ELEVATION ref. to drwng. no. 77443

DESIGNED: EB	SIZE: A1F	SCALE: 1:100	
CODE: 84800	If not otherwise stated: Tolerances ISO 2768-m EN ISO 13920-B Cutting class ISO 9013:442 Weld class ISO 5817:C Surface finish Smooth raw surface	GMR Aero Technic Hangar1 India Megadoor 84000x23000/14000 Interface, Plan views	
ITEM NO			
DATE: 2022-08-23			PLOT DATE
ASSA ABLOY		DRAWING NO: 77444	REVISION: B