





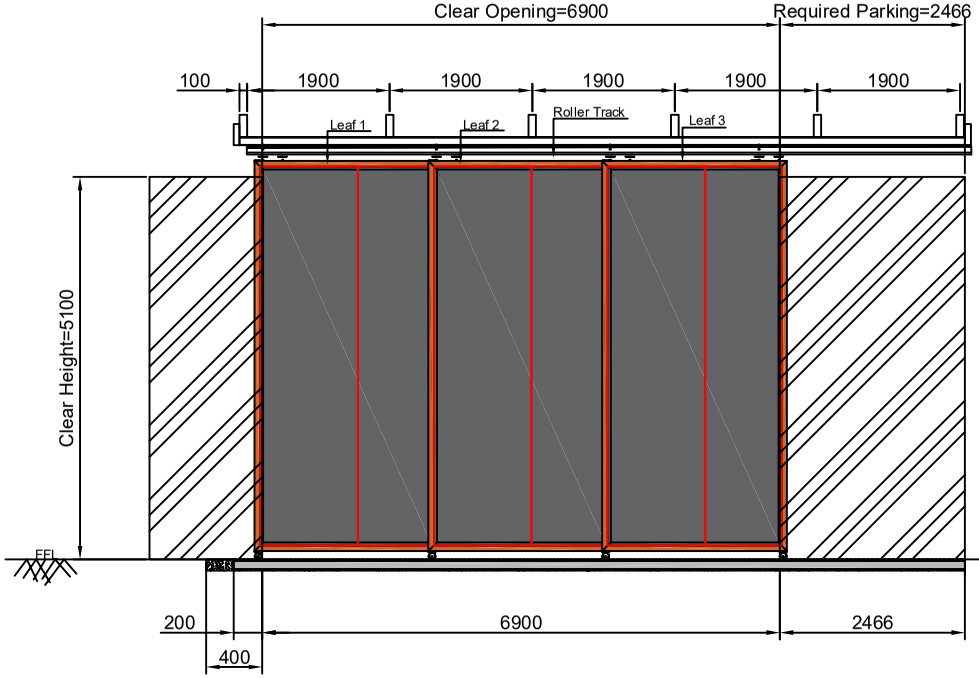

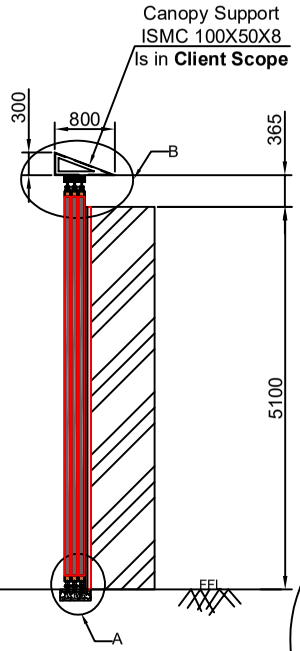


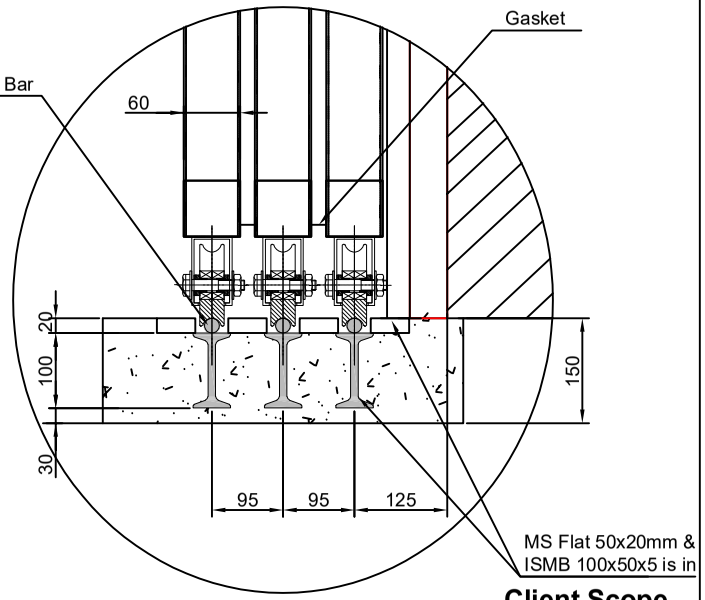

Detail A

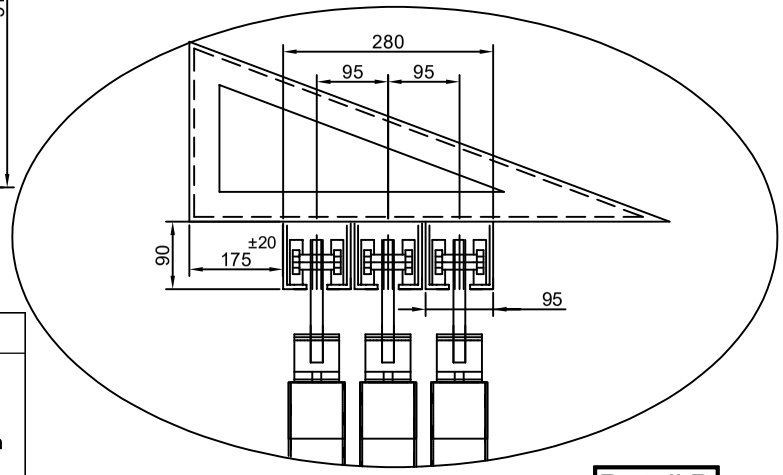

Detail B

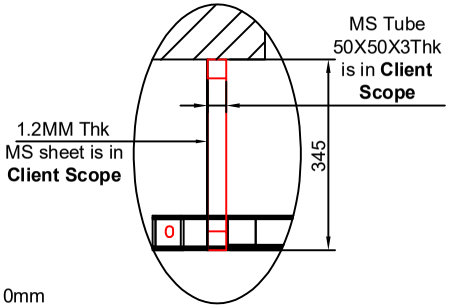

Detail C

Client scope
*Front Gutter need to be shift. * roof need to be shifted by 365mm *Civil foundation need to be done for tracks

Note:--

1.All dimension are in MM
2.All Civil work will be in client scope
3.Required Parking space will be 2465
4.Manufacturing,civil and installation tolerance will be ±10mm
5.Top and Bottom track should be in parallal within ±3mm
6.Nihva Supervisor on site for Monitoring/Checking of civil work

Color code	Color
5018	Turquoise blue

Rev.No	Revision	Date	Revised By
00	Released drawing	29/04/2022	Sujata
1.	Revised as per Client Comments	02/05/2022	Sujata

This drawing & design is the property of NIHVA TECHNOLOGIES. Not to be sold or copied to any other concern.

TITLE:- 3 LEAF RIGHT SIDE CRM DOOR 11/Gate 25

NIHVA TECHNOLOGIES PVT. LTD.

NIHVA TECHNOLOGIES PVT. LTD. PUNE
Tel : 020 66304033
Email:- info@nihva.com
Website:- www.nihva.com

	NAME	DATE	SIGN
DRAWN	SUJATA	29/04/2022	
CHECK	M.SUTAR	29/04/2022	
APPRD.	V.TARAK	29/04/2022	

CLIENT - LESTECH
LOCATION - POSCO MANGAON
PRODUCT - SLIDING DOOR
If any queries contact : design@nihva.com
DWG NO:-NIHVA/22-23/CLT/0016 REV- 1
ALL DIMENSION ARE IN mm
SCALE: NTS SCALE:-- 1:1 SHEET: 01 OF 01