

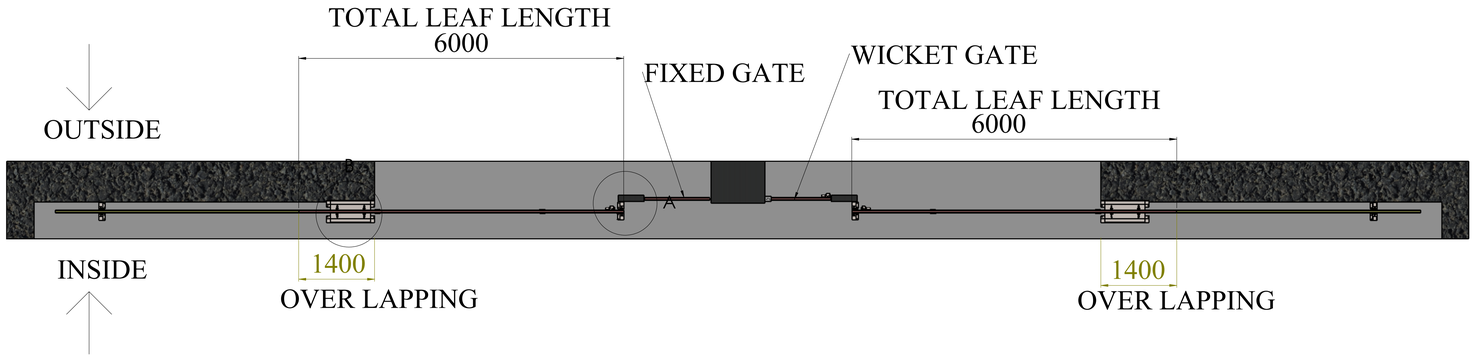


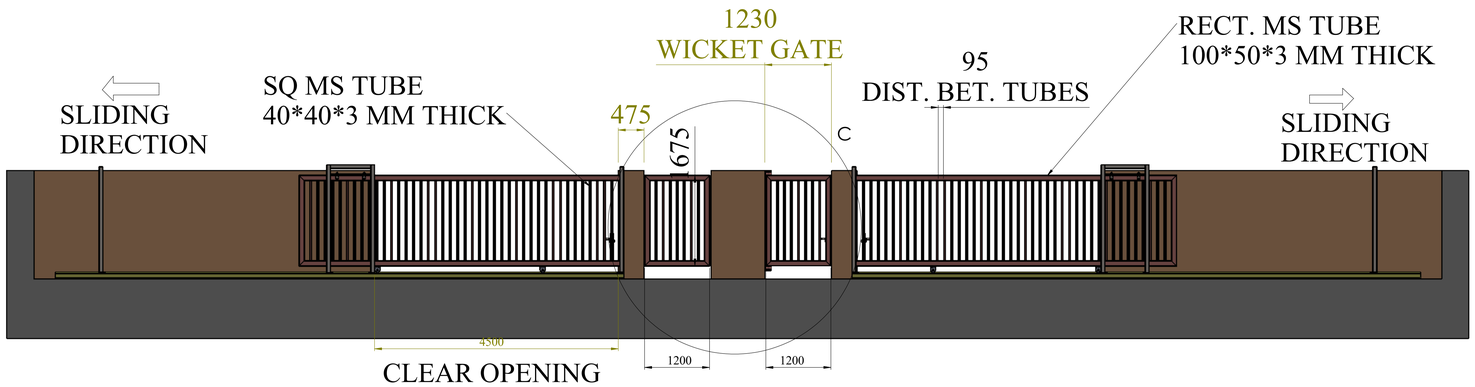


CLEAR OPENING

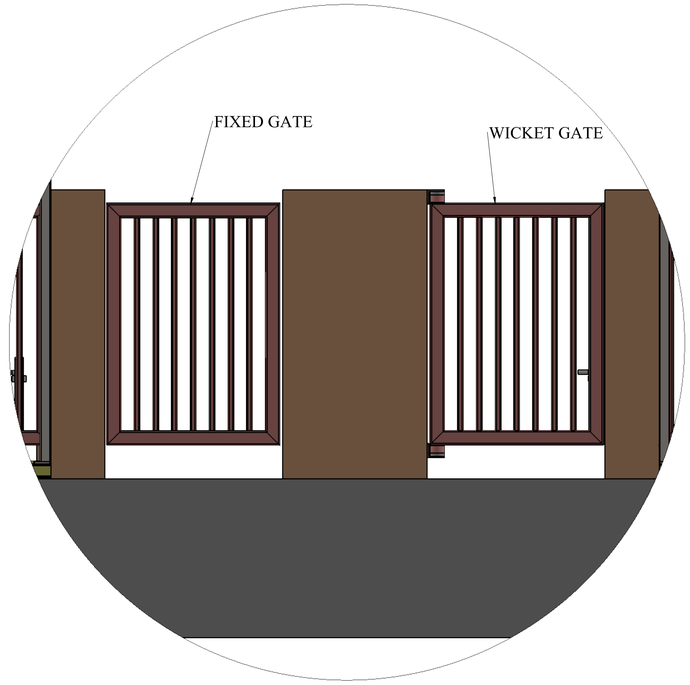


FIXED GATE AND SWING GATE VIEW

DETAIL C
SCALE 1 : 15

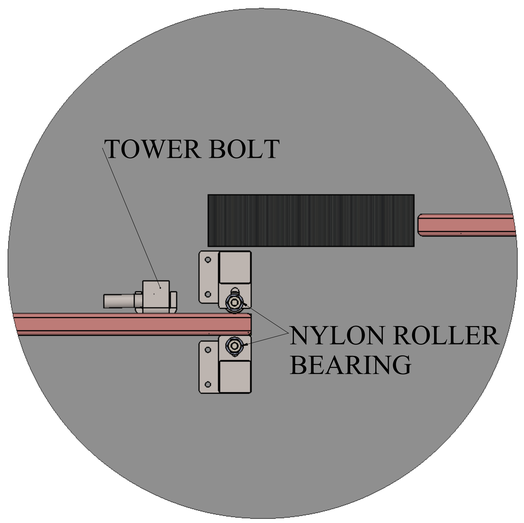


POST 1 AND NYLON ROLLER BEARING ASSEM.

DETAIL A
SCALE 1 : 5

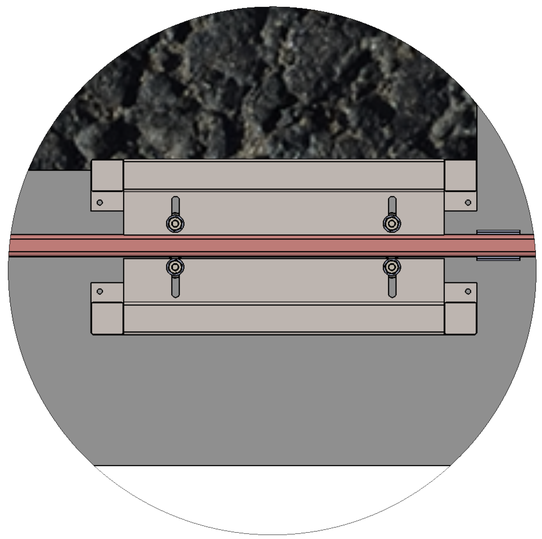

POST 2 AND NYLON ROLLER BEARING ASSEM.

DETAIL B
SCALE 1 : 5

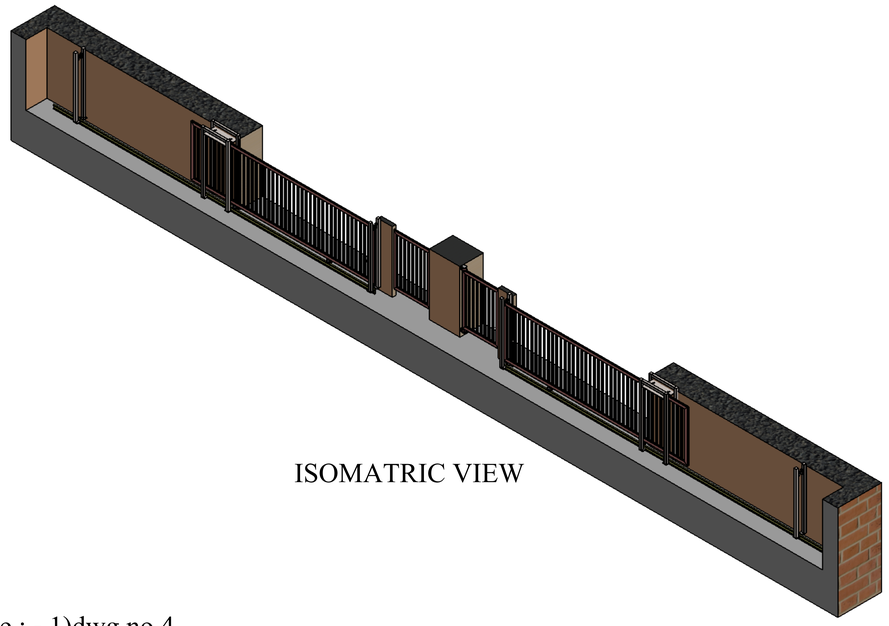

ISOMATRIC VIEW

Note : - 1)dwg no 4
2) barbed wire is not menstion in this dwg.
3) 03 column posts when the gates is in the closed position.
4) 03 column posts when the gates is in the fully open position.

UNLESS OTHERWISE SPECIFIED: DIMENSIONS ARE IN MILLIMETERS SURFACE FINISH: TOLERANCES: LINEAR: ANGULAR:					FINISH:	DEBURR AND BREAK SHARP EDGES	DO NOT SCALE DRAWING	REVISION
	NAME	SIGNATURE	DATE					
DRAWN							TITLE:	
CHK'D								
APPV'D								
MFG								
Q.A							DWG NO.	
					MATERIAL:		SBFINAL ASSM. GA DRAWING	
					WEIGHT:		SCALE:1:100	SHEET 1 OF 1