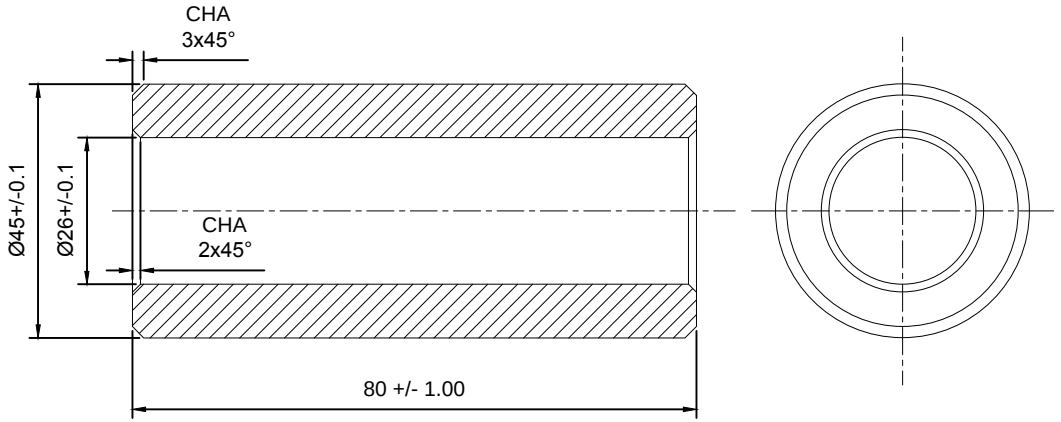


NOTE:~ MTL : MS

BUSH Ø45 X 83L = 08 NOS

NOTE : ~ PLEASE MAINTAIN 7 MM GAP BETWEEN TWO LIP BUSHES.

This drawing & design is the property of NIHVA TECHNOLOGIES. Not to be sold or copied to any other concern.

TITLE

LIP MOUNTING BUSH

NIHVA TECHNOLOGIES PVT. LTD.

NIHVA TECHNOLOGIES PVT. LTD. PUNE
Tel : 020 66304033
Email:- info@nihva.com
Website:- www.nihva.com

	NAME	SIGN	DATE
DRAWN	PRADEEP		05.09.2018
CHECK	PRADEEP		05.09.2018
APPRD.	PRADEEP		05.09.2018

If any queries contact : design@nihva.com	DWG. NO. : NIHVA/18-19/MFG/DLSD1009/010		
ALL DIMENSION ARE IN mm	SCALE: NTS	WT:	REV- 0

CLIENT -

PROJECT - DLSD1009

SITE LOCATION -