


DRAWING

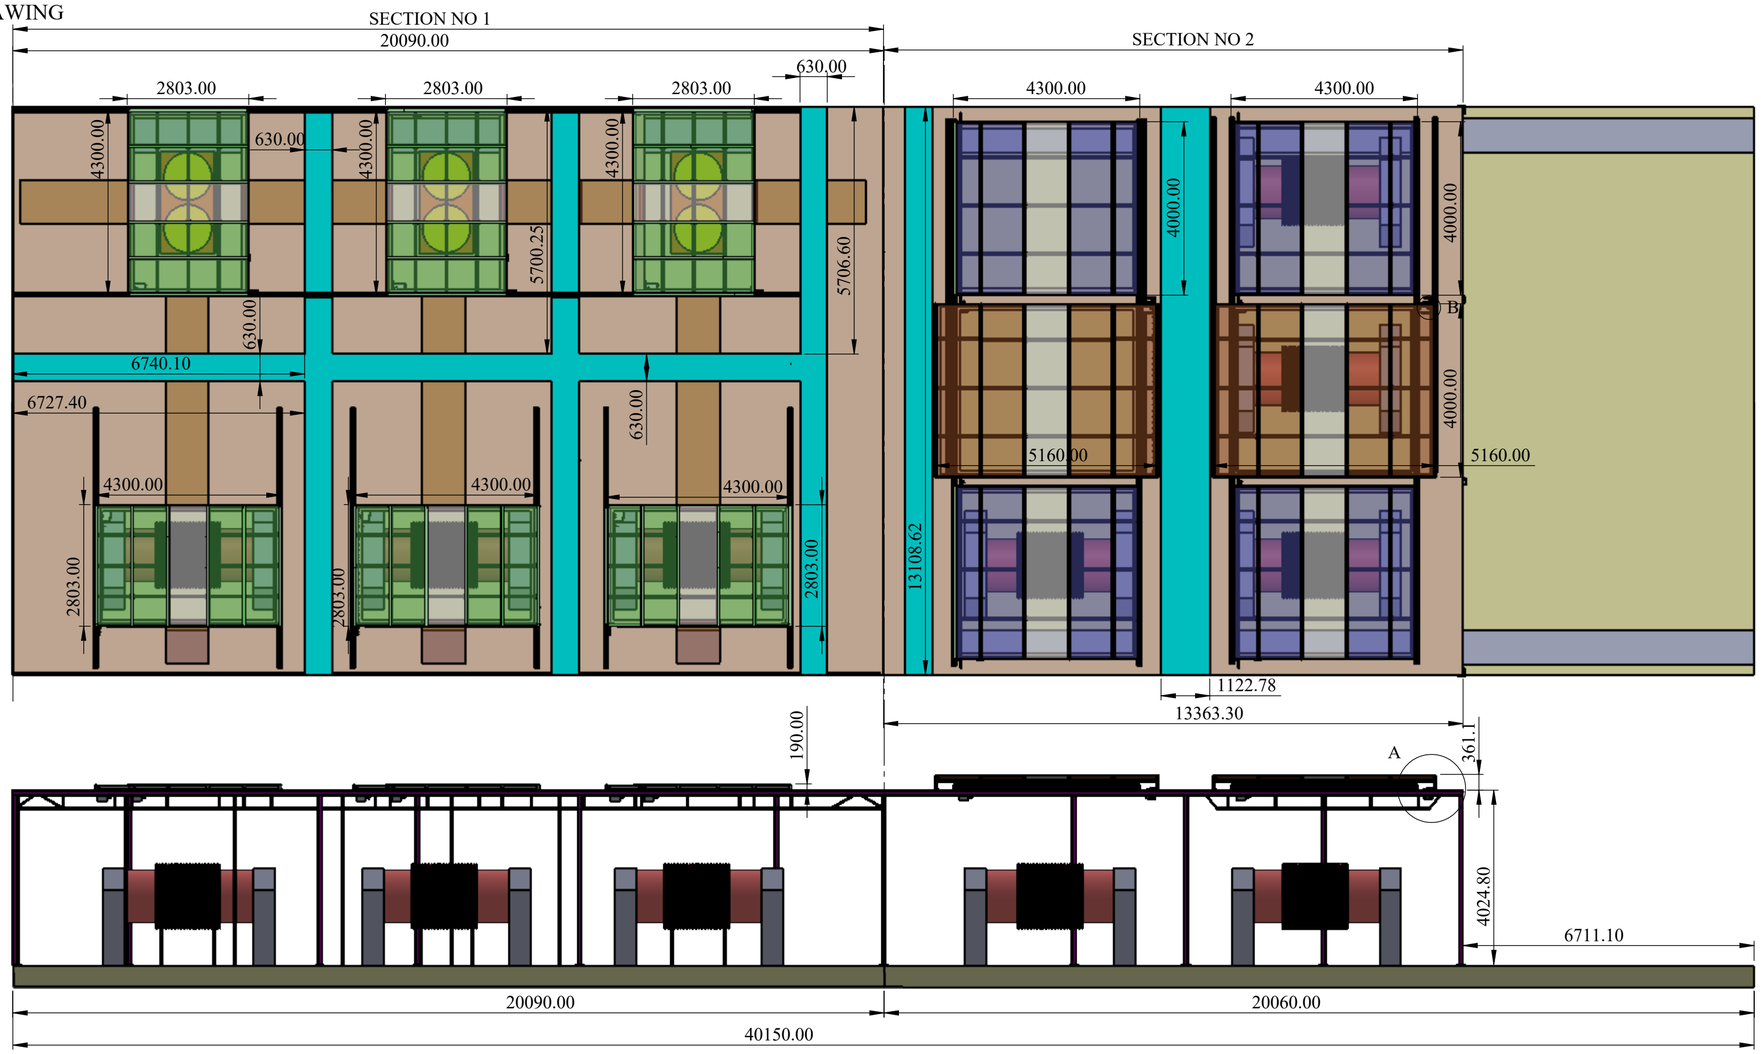

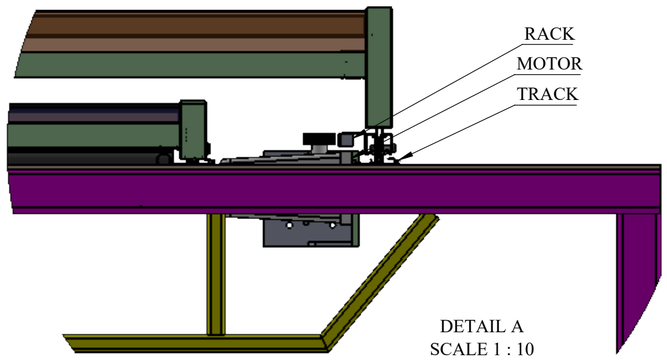

DETAIL A
SCALE 1 : 10
MOTOR ARRANGMENT

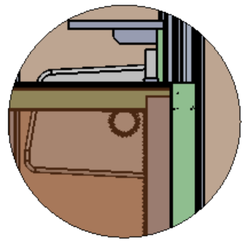

DETAIL B
SCALE 1 : 10

REV DESCRIPTION	DATE	REV NO
	08-08-2025	REV 00
1.		

NOTE :

SPECIAL INSTRUCTION'S :

	NAME	SIGNATURE	DATE
DRAWN	V.W.		28-08-2025
CHK'D	S.P.		04-09-2025
APPV'D	V.T.		05-09-2025

TITLE - ROOF AUTOMATION

DWG NO - NTPL-244-PM-001-00-00-00

NIHVA TECHNOLOGIES PVT.LTD.PUNE
Website - www.nihva.com

PRODUCT - RETRACTABLE ROOF

PROJECT NO - NTPL-244-PM | REVISION - 00

SITE LOCATION - GUJARAT | WEIGHT -

MATRIAL - | QTY - 1

If any queries contact - Design@nihva.com


ALL DIMENSION ARE IN mm | A2

PROJECTION METHOD:

SCALE :

DRAWING

REV DESCRIPTION	DATE	REV NO
	28-08-2025	REV 00
1.		

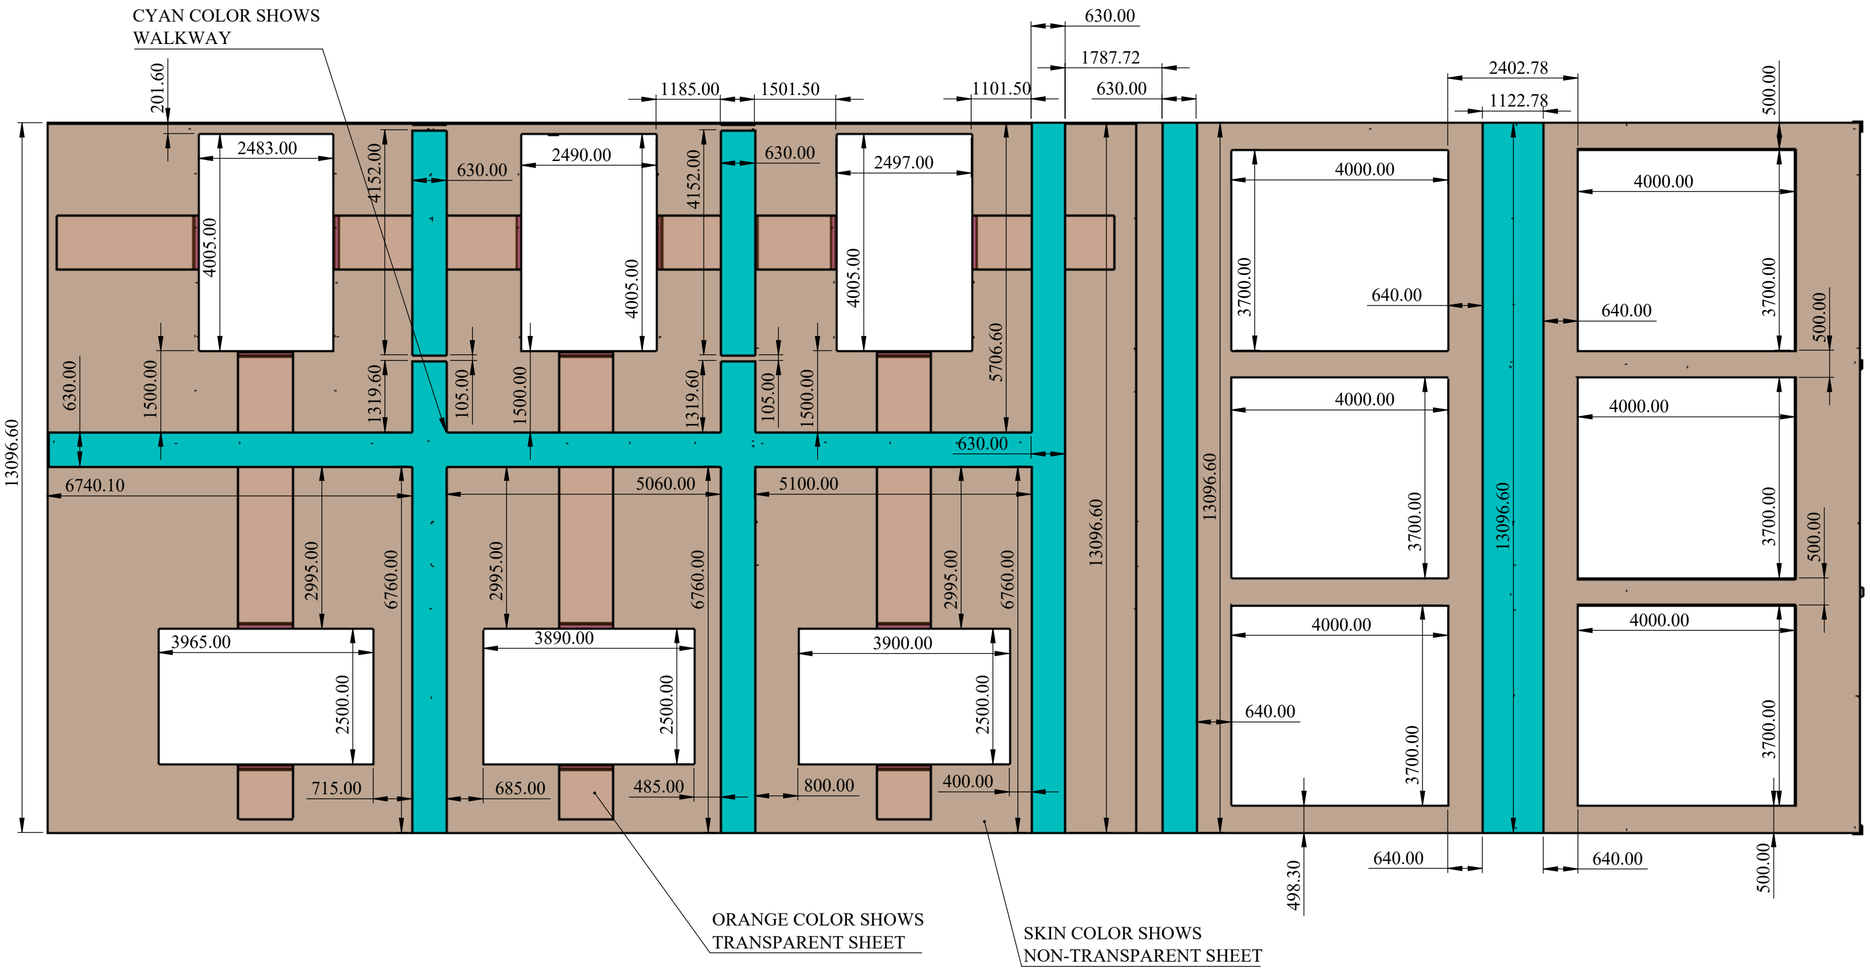

NOTE :

SPECIAL INSTRUCTION'S :

TITLE - ROOF AUTOMATION

DWG NO - NTPL-244-PM-001-00-00-00

NIHVA Technologies Pvt. Ltd.

NIHVA TECHNOLOGIES PVT.LTD.PUNE
Website - www.nihva.com

	NAME	SIGNATURE	DATE
DRAWN	V.W.		28-08-2025
CHK'D	S.P.		04-09-2025
APPV'D	V.T.		05-09-2025

PRODUCT - RETRACTABLE ROOF

PROJECT NO - NTPL-244-PM | REVISION - 00

SITE LOCATION - GUJARAT | WEIGHT -

MATRIAL - | QTY - 1


If any queries contact - Design@nihva.com


ALL DIMENSION ARE IN mm | A2


PROJECTION METHOD:

SCALE :


DRAWING

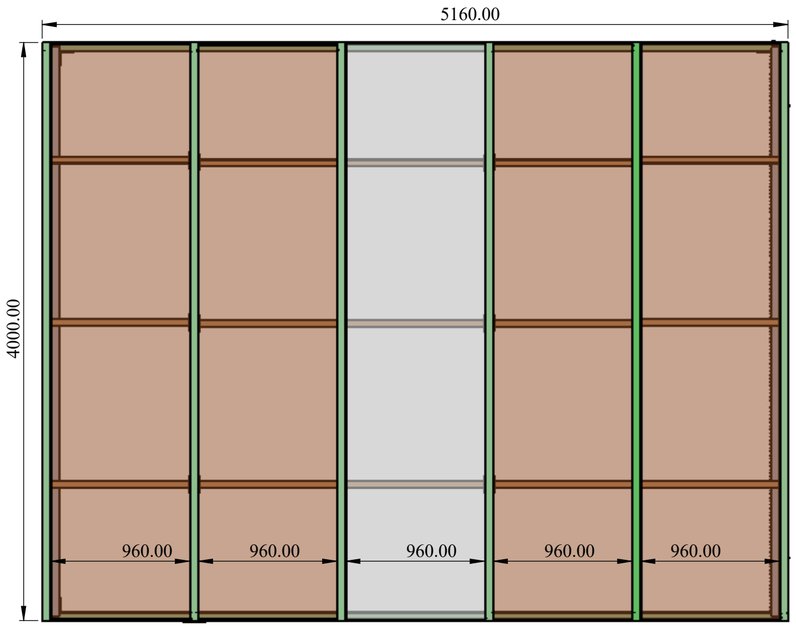


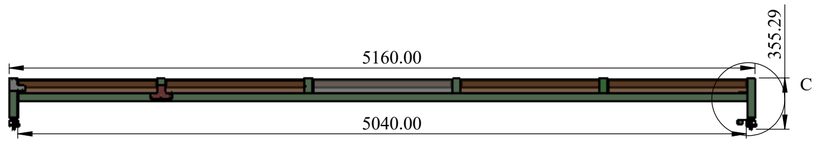

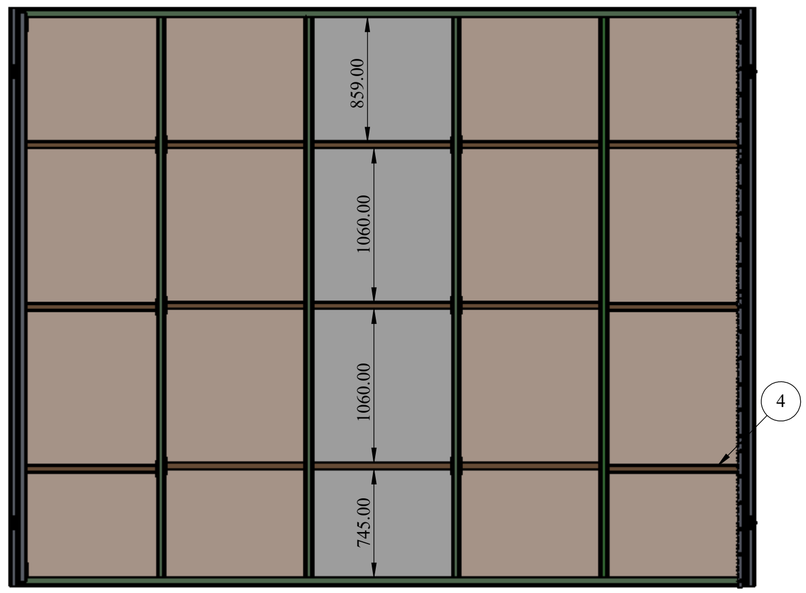

ITEM NO.	PART NUMBER	DESCRIPTION	QTY.
1	.REV_02_PANEEL MODIFY-03..		1
2	.REV_02_PANEL MODIFIY-03 INTERMEDIATE SUPPORT ASSEMBLY..		9
3	.REV_02_SS WHEEL..	SS WHEEL ∅65X18	4
4	.REV_02_PANEL MODIFIY-02 INTERMEDIATE SUPPORT ASSEMBLY..		6
5	L ANGLE PLATE	17X52X3 MM THK	1
6	L PLATE	91X106X3 MM THK	1
7	.REV_02_AL INSIDE CORNER WELD PLATE..	196X40X3 MM THK	4
8	C-MSBL12-35.SLDASM	SHOULDER BOLT	4
9	.REV_02_RACK..		4
10	RACK SUPPORT PLATE.		8

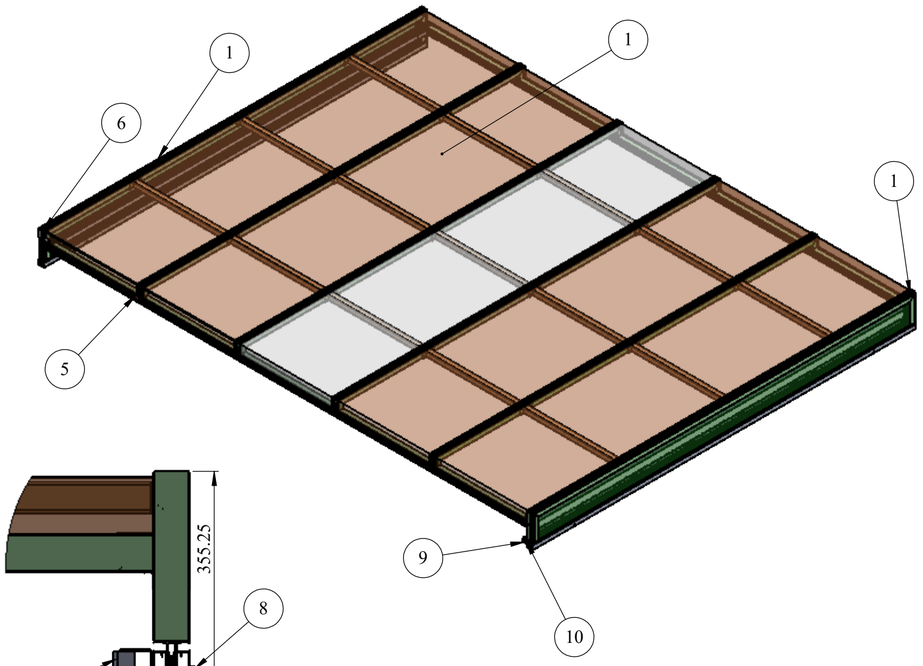

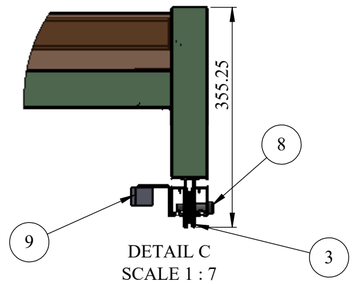

DETAIL C
SCALE 1 : 7

REV DESCRIPTION	DATE	REV NO
	28-08-2025	REV 00
1.		

NOTE :

NAME - SECTION-2 PANEL NO 1 asm
QTY - 02 NOS.

SPECIAL INSTRUCTION'S :

TITLE - ROOF AUTOMATION

DWG NO - NTPL-244-PM-001-00-00-00

NIHVA Technologies Pvt. Ltd.

NIHVA TECHNOLOGIES PVT.LTD.PUNE
Website - www.nihva.com

	NAME	SIGNATURE	DATE		
DRAWN	V.W.		28-08-2025	PROJECT NO - NTPL-244-PM	REVISION - 00
CHK'D	S.P.		04-09-2025	SITE LOCATION - GUJARAT	WEIGHT -
APPV'D	V.T.		05-09-2025	MATRIAL -	QTY - 1

PRODUCT - RETRACTABLE ROOF

If any queries contact - Design@nihva.com


ALL DIMENSION ARE IN mm | A2


PROJECTION METHOD:


SCALE :


DRAWING

ITEM NO.	PART NUMBER	DESCRIPTION	QTY.
1	.REV_02_PANEEL MODIFY-03..		1

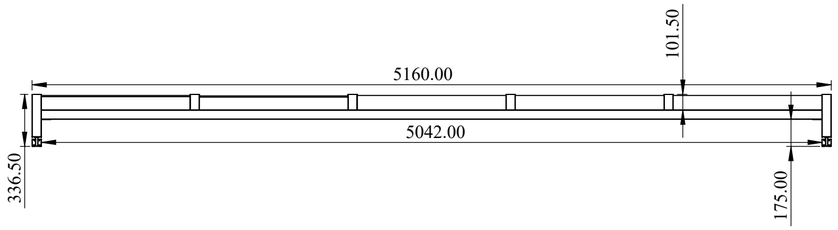

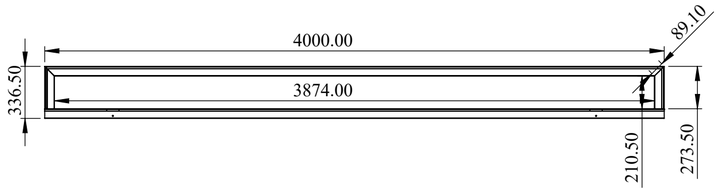

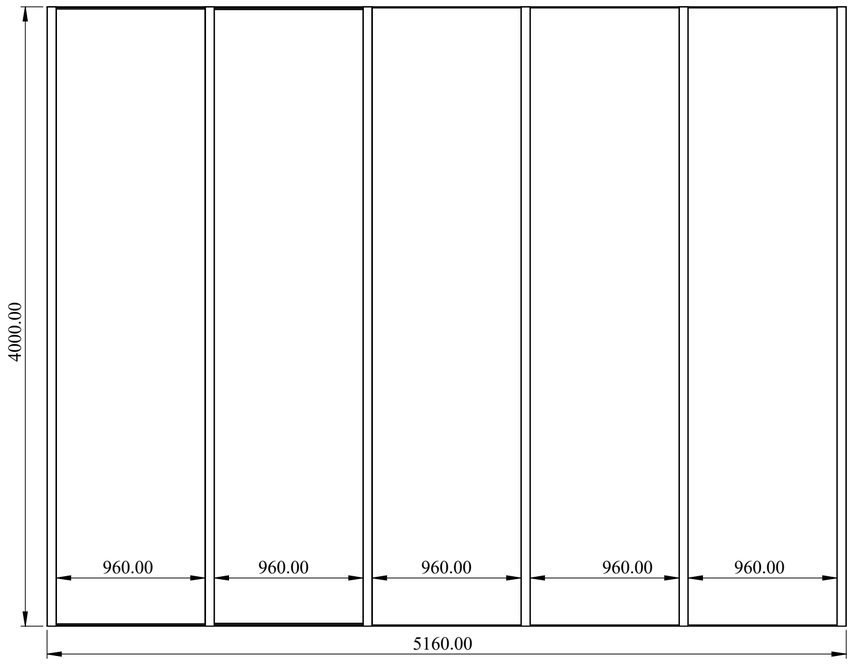

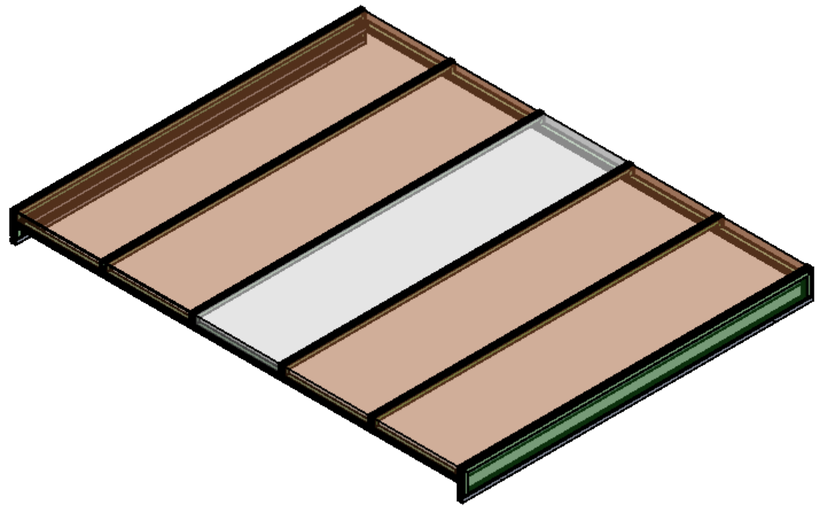

REV DESCRIPTION	DATE	REV NO
	08-08-2025	REV 00
1.		

NOTE :

SECTION NO 2 - PANEL
QTY - 02 No's

SPECIAL INSTRUCTION'S :

TITLE - ROOF AUTOMATION

DWG NO - NTPL-244-PM-001-00-00-00

NIHVA TECHNOLOGIES PVT.LTD.PUNE
Website - www.nihva.com


	NAME	SIGNATURE	DATE
DRAWN	V.W.		28-08-2025
CHK'D	S.P.		04-08-2025
APPV'D	V.T.		05-08-2025


PRODUCT - RETRACTABLE ROOF
PROJECT NO - NTPL-244-PM
REVISION - 00
SITE LOCATION - GUJARAT
WEIGHT -
MATRIAL -
QTY - 1
If any queries contact - Design@nihva.com
PROJECTION METHOD:
SCALE :
ALL DIMENSION ARE IN mm
A2

DRAWING

ITEM NO.	PART NUMBER	DESCRIPTION	QTY.
1	MS PROFILE	REC - 50X50X2T	1
2	.Rev_02_NP-PLT01..	AL - 90X40X3T	2

REV DESCRIPTION	DATE	REV NO
	28-08-2025	REV 00
1.		

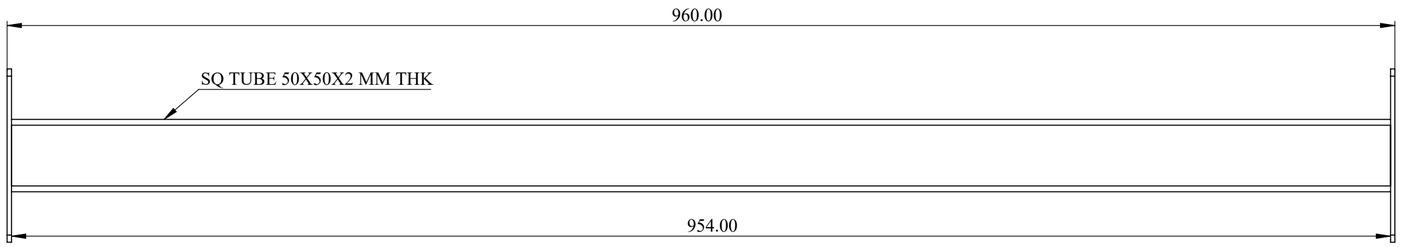

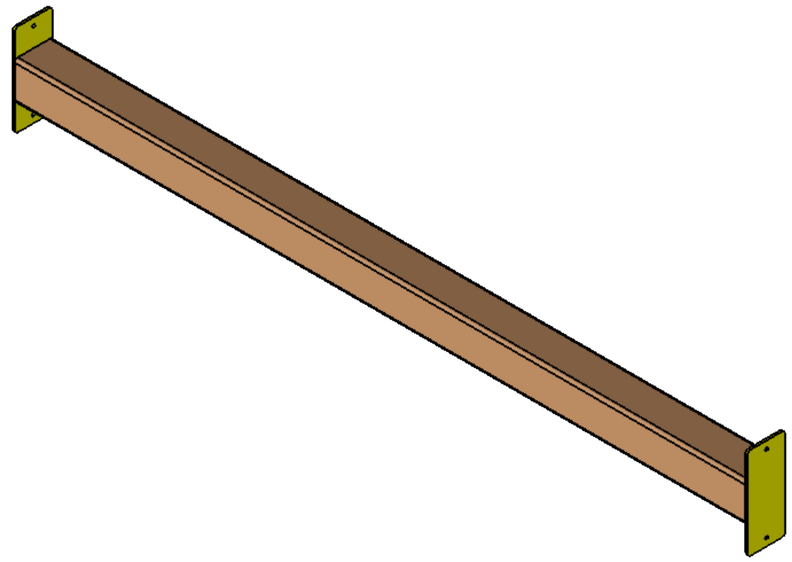

NOTE :

NAME : INTERMEDIATE SUPPORT TUBE
SIZE : 50X50X2 MM THK - 960 MM L
QTY : ONE PANEL REQ QTY - 15 NOS
TOTAL QTY REQ - 30 NOS
MTL : AL

SPECIAL INSTRUCTION'S :

TITLE - ROOF AUTOMATION

DWG NO - NTPL-244-PM-001-00-00-00

NIHVA TECHNOLOGIES PVT.LTD.PUNE
Website - www.nihva.com


	NAME	SIGNATURE	DATE
DRAWN	V.W.		28-08-2025
CHK'D	S.P.		04-09-2025
APPV'D	V.T.		05-09-2025


PRODUCT - RETRACTABLE ROOF
PROJECT NO - NTPL-244-PM
REVISION - 00
SITE LOCATION - GUJARAT
WEIGHT -
MATRIAL -
QTY - 1
SCALE :
PROJECTION METHOD:
If any queries contact - Design@nihva.com
ALL DIMENSION ARE IN mm
A2


DRAWING

REV DESCRIPTION	DATE	REV NO
	28-08-2025	REV 00
1.		

ITEM NO.	PART NUMBER	DESCRIPTION	QTY.
1	NYLON WHEEL	NYLON WHEEL ∅65X18	04

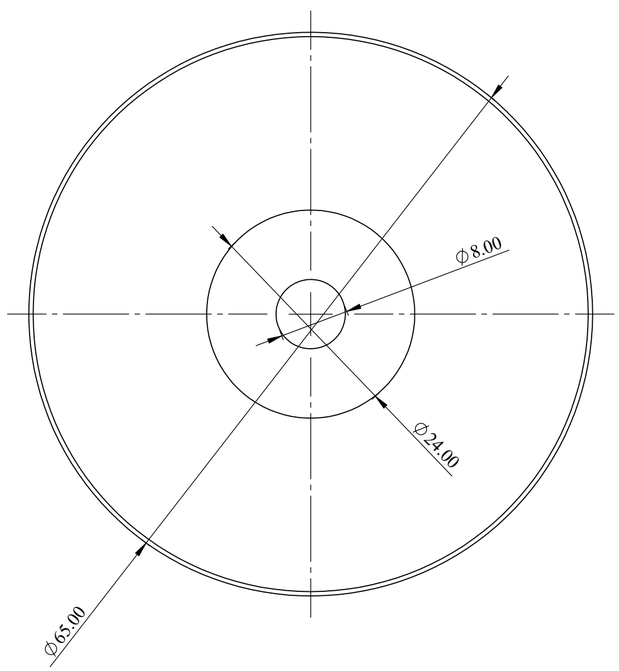

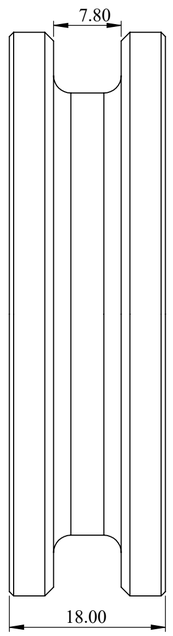

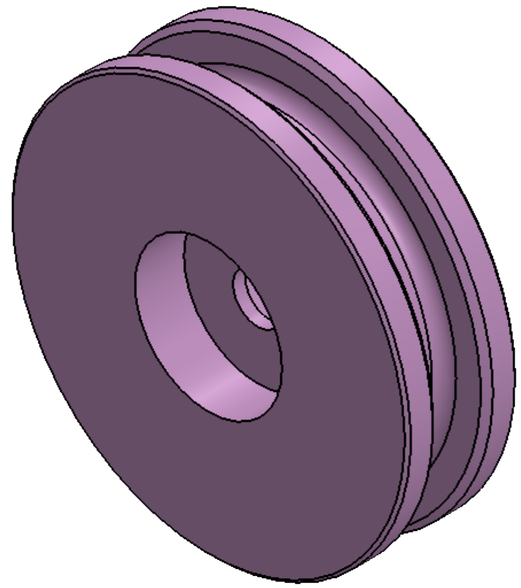

NOTE :

NYLON WHEEL - DIA 65X W 18 MM
ONE PANEL REQ QTY - 04 No'S.
TOTAL REQ QTY - 24 No'S

SPECIAL INSTRUCTION'S :

TITLE - ROOF AUTOMATION

DWG NO - NTPL-244-PM-001-00-00-00

NIHVA Technologies Pvt. Ltd.

NIHVA TECHNOLOGIES PVT.LTD.PUNE
Website - www.nihva.com


	NAME	SIGNATURE	DATE
DRAWN	V.W.		28-08-2025
CHK'D	S.P.		04-09-2025
APPV'D	V.T.		05-09-2025


PRODUCT - RETRACTABLE ROOF
PROJECT NO - NTPL-244-PM | REVISION - 00
SITE LOCATION - GUJARAT | WEIGHT -
MATRIAL - | QTY - 1
If any queries contact - Design@nihva.com | PROJECTION METHOD: | SCALE :
ALL DIMENSION ARE IN mm | A2 | SHEET 6 OF 14

DRAWING

REV DESCRIPTION	DATE	REV NO
	28-08-2025	REV 00
1.		

ITEM NO.	PART NUMBER	DESCRIPTION	QTY.
1	L PLATE	91X106X3 MM THK	8

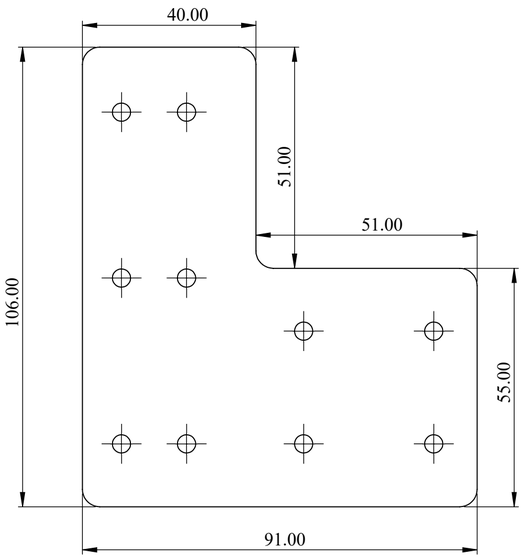

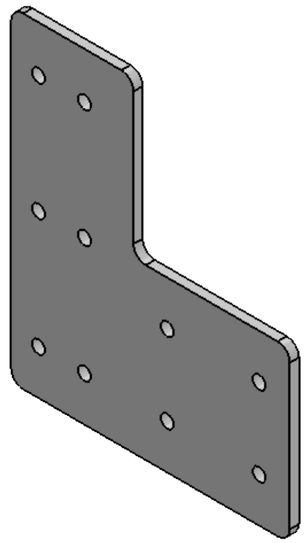

NOTE :

NAME - L PLATE
SIZE - 106X91X3 MM THK
THK - 3 MM
ONE PANEL REQ QTY - 8 No'S
TOTAL REQ QTY - 48 No'S
MTL - SS.

SPECIAL INSTRUCTION'S :

TITLE - ROOF AUTOMATION

DWG NO - NTPL-244-PM-001-00-00-00

NIHVA Technologies Pvt. Ltd.

NIHVA TECHNOLOGIES PVT.LTD.PUNE
Website - www.nihva.com


	NAME	SIGNATURE	DATE
DRAWN	V.W.		28-08-2025
CHK'D	S.P.		04-09-2025
APPV'D	V.T.		05-09-2025


PRODUCT - RETRACTABLE ROOF
PROJECT NO - NTPL-244-PM
REVISION - 00
SITE LOCATION - GUJARAT
WEIGHT -
MATRIAL -
QTY - 1
SCALE :
PROJECTION METHOD:
If any queries contact - Design@nihva.com
ALL DIMENSION ARE IN mm
A2

DRAWING

REV DESCRIPTION	DATE	REV NO
	28-08-2025	REV 00
1.		

ITEM NO.	PART NUMBER	DESCRIPTION	QTY.
1	L ANGLE PLATE	17X52X3 MM THK	08

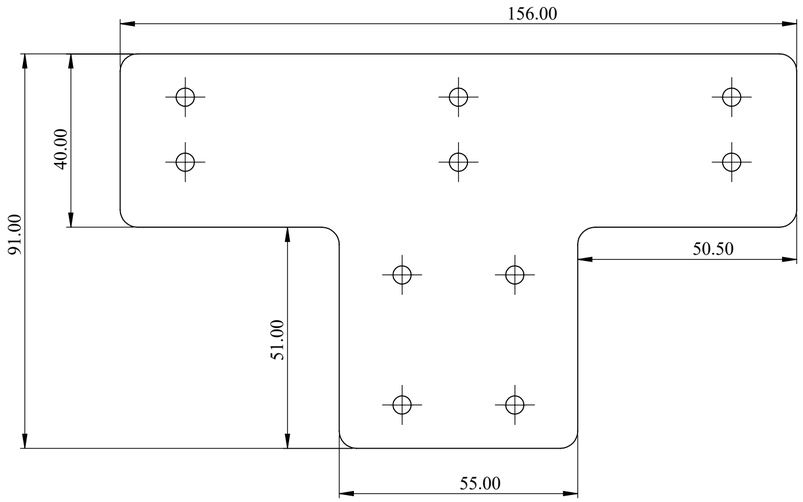

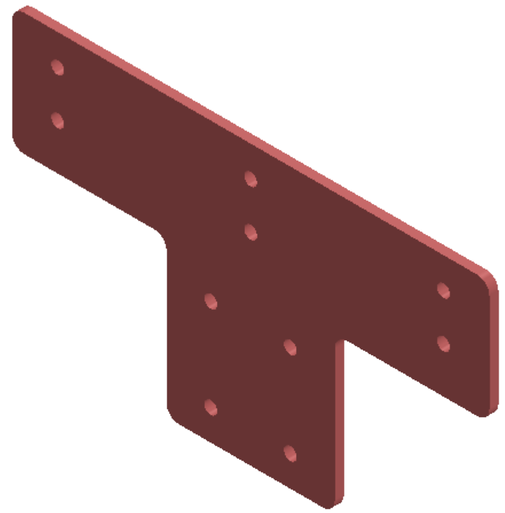

NOTE :

NAME - T PLATE
SIZE - 156X91X3 MM THK
THK - 3 MM
MTL - SS
ONE PANEL REQ QTY - 08 No'S
TOTAL REQ QTY - 48 No'S.

SPECIAL INSTRUCTION'S :

TITLE - ROOF AUTOMATION

DWG NO - NTPL-244-PM-001-00-00-00

NIHVA Technologies Pvt. Ltd.

NIHVA TECHNOLOGIES PVT.LTD.PUNE
Website - www.nihva.com

	NAME	SIGNATURE	DATE
DRAWN	V.W.		28-08-2025
CHK'D	S.P.		04-09-2025
APPV'D	V.T.		05-09-2025


PRODUCT - RETRACTABLE ROOF
PROJECT NO - NTPL-244-PM
REVISION - 00
SITE LOCATION - GUJARAT
WEIGHT -
MATRIAL -
QTY - 1
SCALE :
PROJECTION METHOD:
SHEET 8 OF 14


If any queries contact - Design@nihva.com
ALL DIMENSION ARE IN mm
A2


DRAWING

ITEM NO.	PART NUMBER	DESCRIPTION	QTY.
1	BUSBAR MTG PLATE FOR RACK SUPPORT		8

REV DESCRIPTION	DATE	REV NO
	28-08-2025	REV 00
1.		

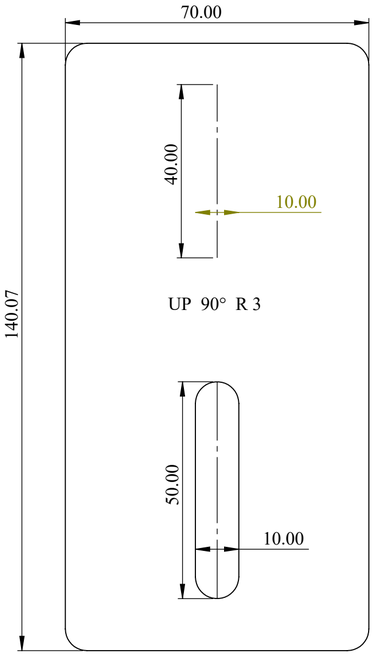

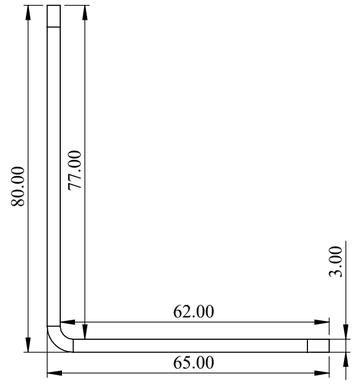

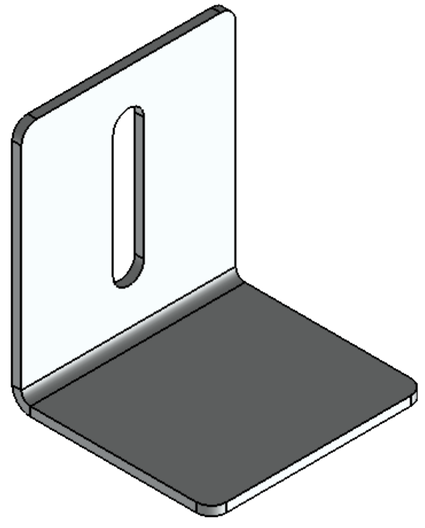

NOTE :

NAME - RACK SUPPORT PLATE
SIZE - 140.07X70X3 MM THK
THK - 3 MM
MTL - MS
ONE PANEL PANEL REQ QTY -8 No'S
TOTAL REQ QTY - 48 No'S.

SPECIAL INSTRUCTION'S :

TITLE - ROOF AUTOMATION

DWG NO - NTPL-244-PM-001-00-00-00

NIHVA Technologies Pvt. Ltd.


NIHVA TECHNOLOGIES PVT.LTD.PUNE
Website - www.nihva.com


	NAME	SIGNATURE	DATE		
				PRODUCT - RETRACTABLE ROOF	
DRAWN	V.W.		28-08-2025	PROJECT NO - NTPL-244-PM	REVISION - 00
CHK'D	S.P.		04-09-2025	SITE LOCATION - GUJARAT	WEIGHT -
APPV'D	V.T.		05-09-2025	MATRIAL -	QTY - 1
If any queries contact - Design@nihva.com				PROJECTION METHOD:	SCALE :
ALL DIMENSION ARE IN mm			A2		SHEET 9 OF 14

DRAWING

REV DESCRIPTION	DATE	REV NO
	28-08-2025	REV 00
1.		

ITEM NO.	PART NUMBER	DESCRIPTION	QTY.
1	.REV_02_RACK..		4

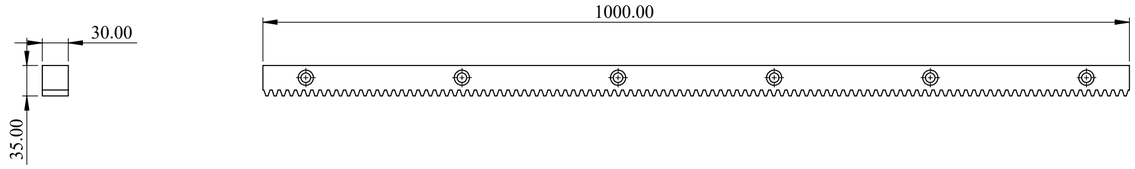

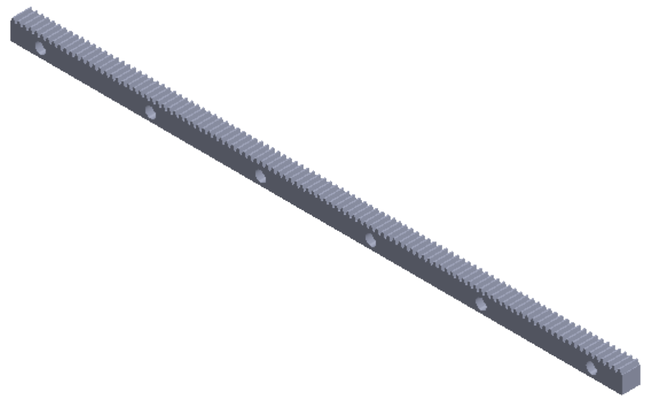

NOTE :

NAME - RACK
ONE PANEL REQ QTY - 4 No'S
TOTAL REQ QTY - 24 No'S.

SPECIAL INSTRUCTION'S :

TITLE - ROOF AUTOMATION

DWG NO - NTPL-244-PM-001-00-00-00

NIHVA Technologies Pvt. Ltd.

NIHVA TECHNOLOGIES PVT.LTD.PUNE
Website - www.nihva.com

	NAME	SIGNATURE	DATE	
DRAWN	V.W.		28-08-2025	PRODUCT - RETRACTABLE ROOF
CHK'D	S.P.		04-09-2025	PROJECT NO - NTPL-244-PM / REVISION - 00
APPV'D	V.T.		05-09-2025	SITE LOCATION - GUJARAT / WEIGHT -
				MATRIAL - / QTY - 1


If any queries contact - Design@nihva.com


ALL DIMENSION ARE IN mm | A2


PROJECTION METHOD:


SCALE :

DRAWING

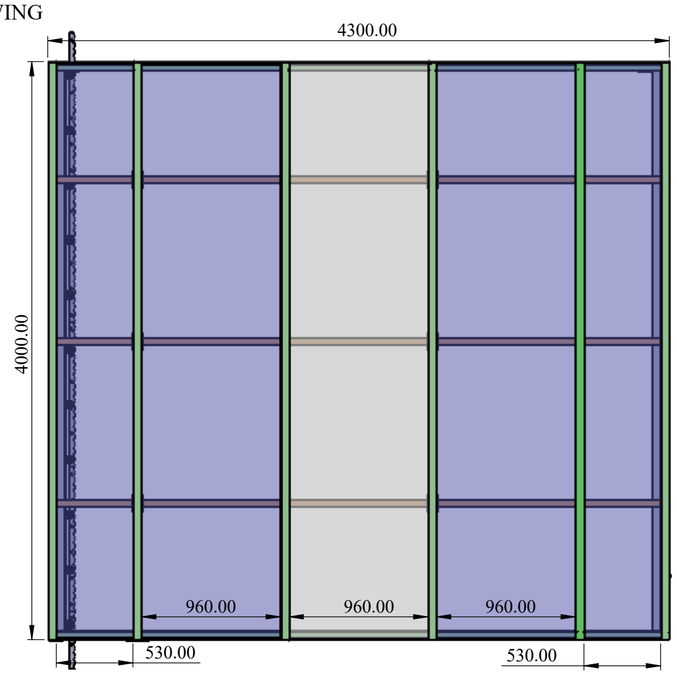

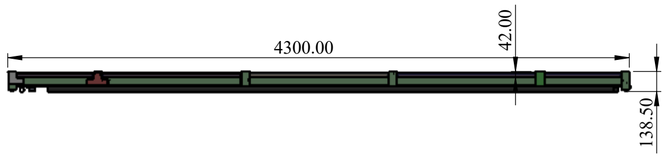

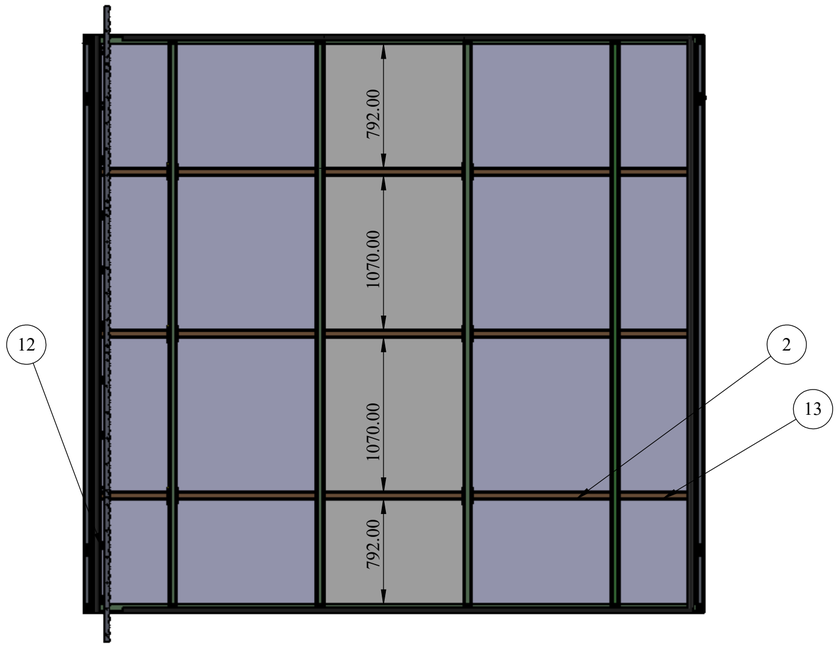

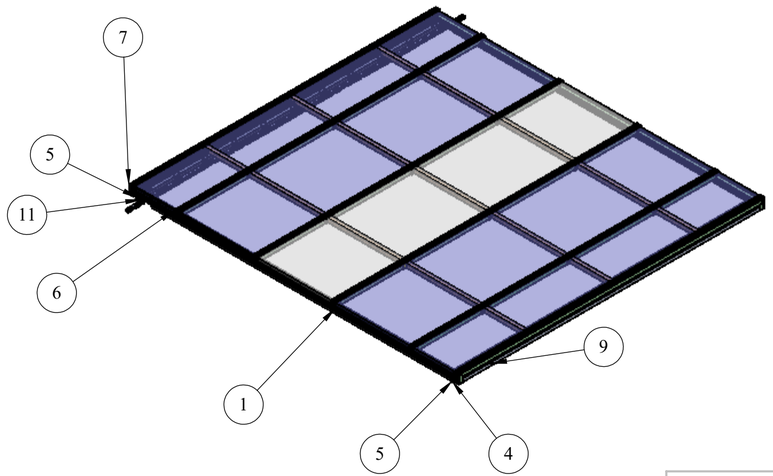

ITEM NO.	PART NUMBER	DESCRIPTION	QTY.
1	.Rev_02_paneel modify-03.		1
2	.Rev_02_panel modifiy-03 intermediate support assembly.		9
3	.Rev_02_SS WHEEL.	SS WHEEL ∅65X18	4
4	NP-PROF01	MS50X50X4T	2
5	NP-PROF01	MS50X50X4T	2
6	T PLATE	156X91X3 MM THK	1
7	L PLATE	91X106X3 MM THK	1
8	.Rev_02_AL INSIDE CORNER WELD PLATE.	196X40X3 MM THK	4
9	C-MSBL12-35.SLDASM	SHOULDER BOLT	1
10	.rev0202RACK.		4
11	RACK CUT 200MM L.		1
12	RACK SUPPORT PLATE.		11
13	SQ TUBE 50X50X2 MM THK - 530 MM L		6

REV DESCRIPTION	DATE	REV NO
	28-08-2025	REV 00
1.		

NOTE :

NAME - SECTION-2 PANEL NO 2 ASM
QTY - 04 NOS.

SPECIAL INSTRUCTION'S :

TITLE - ROOF AUTOMATION

DWG NO - NTPL-244-PM-001-00-00-00


NIHVA Technologies Pvt. Ltd.

NIHVA TECHNOLOGIES PVT.LTD.PUNE
Website - www.nihva.com


	NAME	SIGNATURE	DATE
DRAWN	V.W.		28-08-2025
CHK'D	S.P.		04-09-2025
APPV'D	V.T.		05-09-2025

PRODUCT - RETRACTABLE ROOF
PROJECT NO - NTPL-244-PM | REVISION - 00
SITE LOCATION - GUJARAT | WEIGHT -
MATRIAL - | QTY - 1
If any queries contact - Design@nihva.com
ALL DIMENSION ARE IN mm | A2
PROJECTION METHOD:
SCALE :
SHEET 11 OF 14


DRAWING

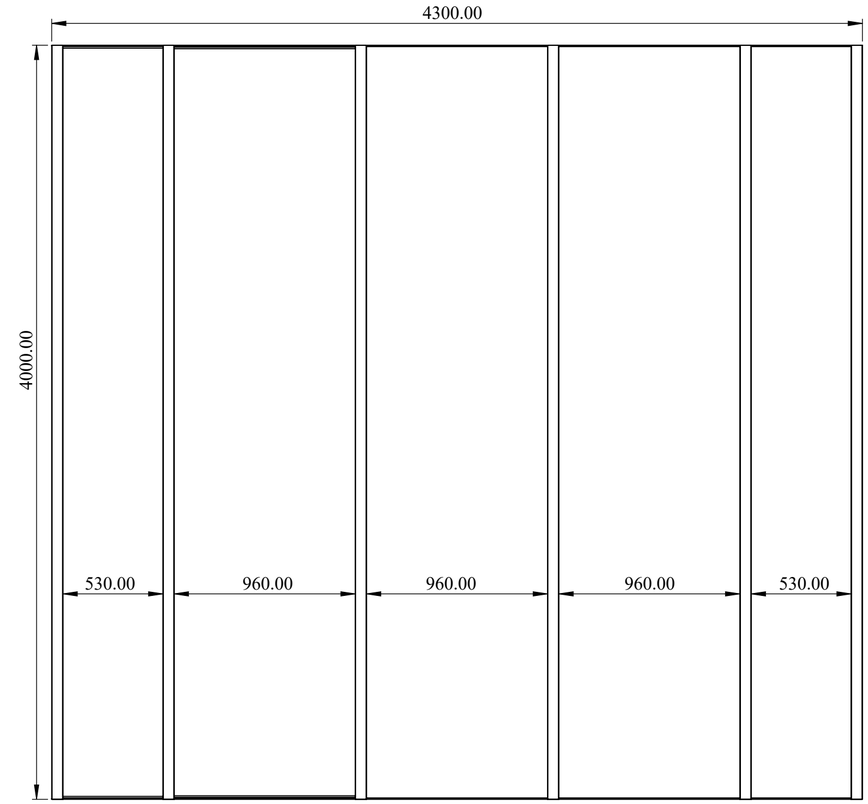



ITEM NO.	PART NUMBER	DESCRIPTION	QTY.
1	.Rev_02_paneel modify-03.		04

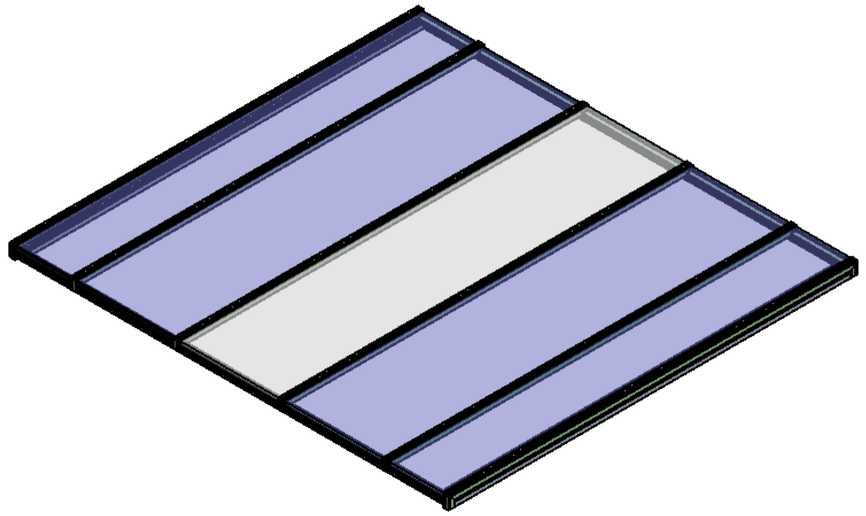


REV DESCRIPTION	DATE	REV NO
	28-08-2025	REV 00
1.		

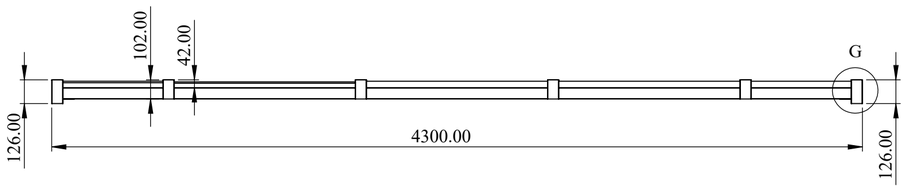

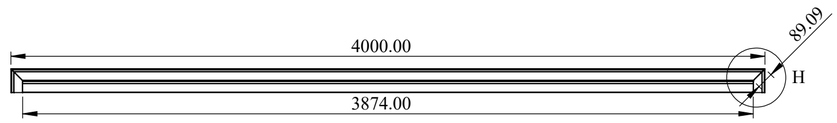

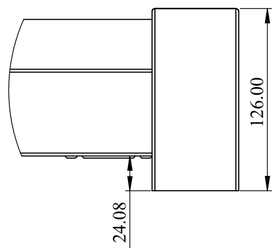

DETAIL G
SCALE 1 : 3

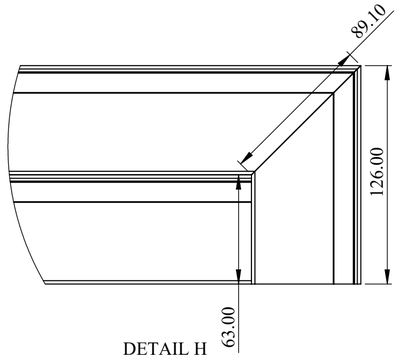

DETAIL H
SCALE 2 : 5

NOTE :

NAME : SECTION 2 - PANEL 02
QTY : 04 NOS.

SPECIAL INSTRUCTION'S :

TITLE - ROOF AUTOMATION

DWG NO - NTPL-244-PM-001-00-00-00


NIHVA Technologies Pvt. Ltd.


NIHVA TECHNOLOGIES PVT.LTD.PUNE
Website - www.nihva.com

	NAME	SIGNATURE	DATE		
DRAWN	V.W.		28-08-2025	PRODUCT - RETRACTABLE ROOF	
CHK'D	S.P.		04-09-2025	PROJECT NO - NTPL-244-PM	REVISION - 00
APPV'D	V.T.		05-09-2025	SITE LOCATION - GUJARAT	WEIGHT -
				MATRIAL -	QTY - 1
If any queries contact - Design@nihva.com				PROJECTION METHOD:	SCALE :
ALL DIMENSION ARE IN mm			A2		SHEET 12 OF 14

DRAWING

ITEM NO.	PART NUMBER	DESCRIPTION	QTY.
1	AL PROFILE	REC - 50X50X2T	1
2	.rev0202NP-PLT01.	AL - 120X50X3T	2

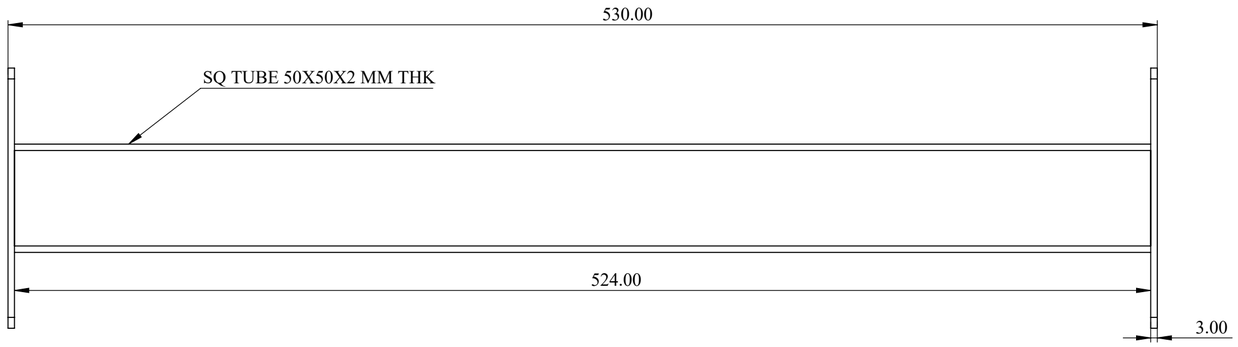

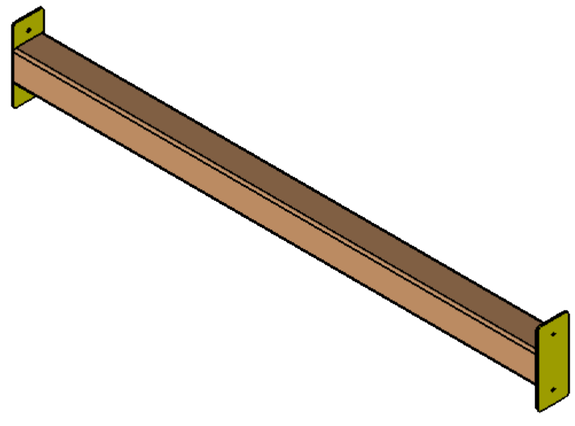

REV DESCRIPTION	DATE	REV NO
	28-08-2025	REV 00
1.		

NOTE :

NAME : INTERMEDIATE SUPPORT TUBE
SIZE : 50X50X2 MM THK - 530 MM L
QTY : ONE PANEL REQ QTY - 6 NOS
TOTAL QTY REQ - 24 NOS

SPECIAL INSTRUCTION'S :

TITLE - ROOF AUTOMATION

DWG NO - NTPL-244-PM-001-00-00-00

NIHVA TECHNOLOGIES PVT.LTD.PUNE
Website - www.nihva.com


	NAME	SIGNATURE	DATE
DRAWN	V.W.		28-08-2025
CHK'D	S.P.		04-09-2025
APPV'D	V.T.		05-09-2025


PRODUCT - RETRACTABLE ROOF
PROJECT NO - NTPL-244-PM | REVISION - 00
SITE LOCATION - GUJARAT | WEIGHT -
MATRIAL - | QTY - 1
If any queries contact - Design@nihva.com | PROJECTION METHOD: | SCALE :
ALL DIMENSION ARE IN mm | A2 | SHEET 13 OF 14

DRAWING

ITEM NO.	PART NUMBER	DESCRIPTION	QTY.
1	MS PROFILE	REC - 50X50X2T	1
2	.Rev_02_NP-PLT01..	AL - 90X40X3T	2

REV DESCRIPTION	DATE	REV NO
	28-08-2025	REV 00
1.		

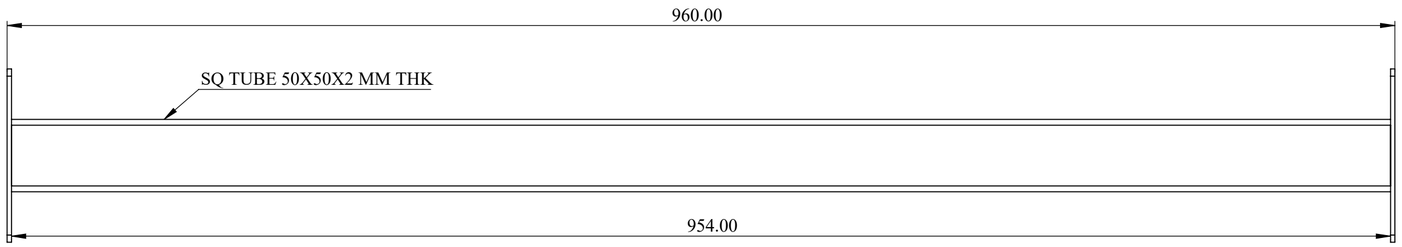

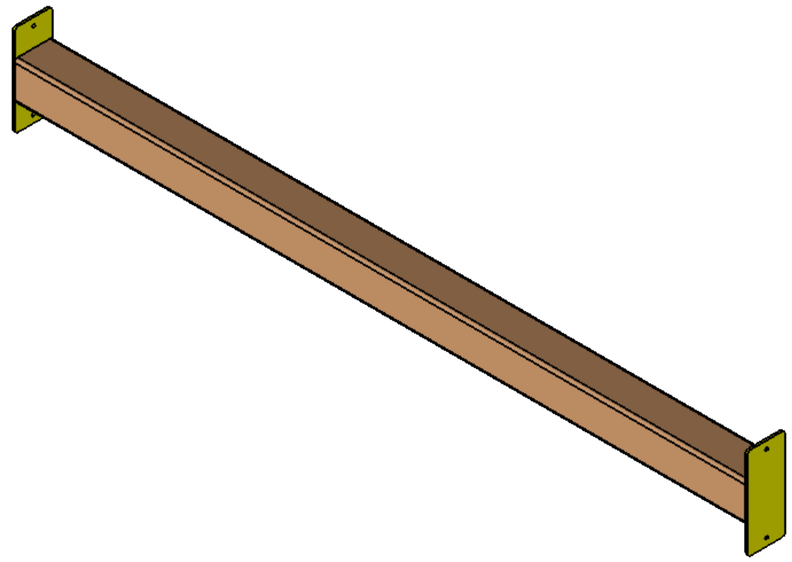

NOTE :

NAME : INTERMEDIATE SUPPORT TUBE
SIZE : 50X50X2 MM THK - 960 MM L
QTY : ONE PANEL REQ QTY - 9 NOS
TOTAL QTY REQ - 36 NOS
MTL : AL

SPECIAL INSTRUCTION'S :

TITLE - ROOF AUTOMATION

DWG NO - NTPL-244-PM-001-00-00-00

NIHVA TECHNOLOGIES PVT.LTD.PUNE
Website - www.nihva.com

	NAME	SIGNATURE	DATE
DRAWN	V.W.		28-08-2025
CHK'D	S.P.		04-09-2025
APPV'D	V.T.		05-09-2025

PRODUCT - RETRACTABLE ROOF
PROJECT NO - NTPL-244-PM
REVISION - 00
SITE LOCATION - GUJARAT
WEIGHT -
MATRIAL -
QTY - 1
SCALE :
PROJECTION METHOD:
SHEET 14 OF 14

If any queries contact - Design@nihva.com
ALL DIMENSION ARE IN mm
A2