


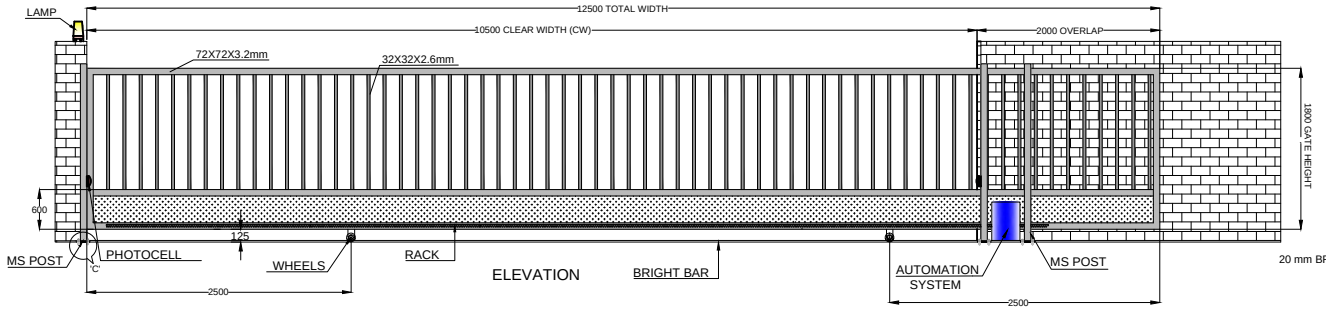


ELEVATION

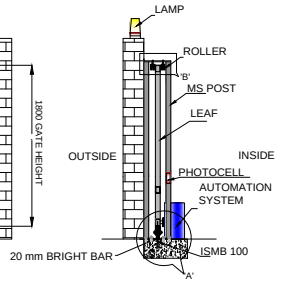


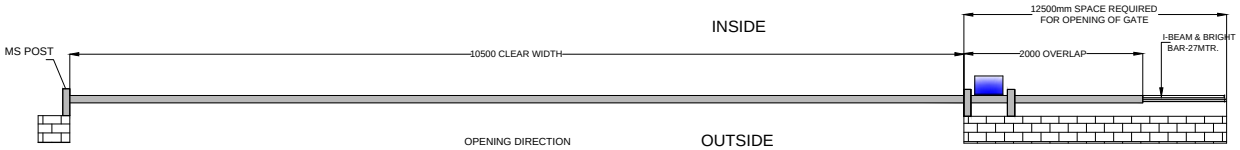


PLAN

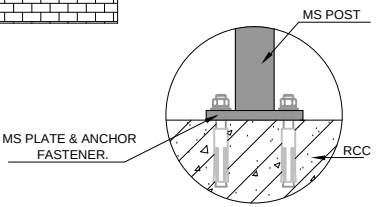

DETAIL VIEW OF C
(FIXING DETAILS)

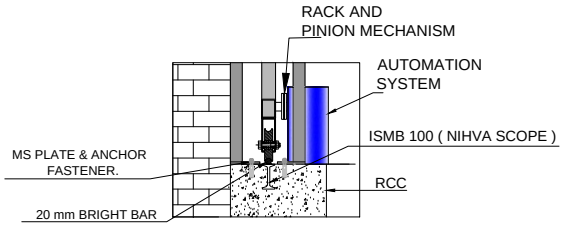

DETAIL VIEW OF A

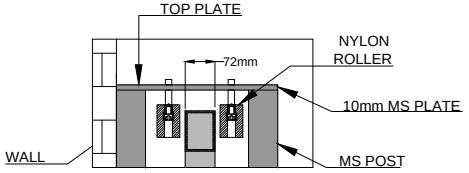

DETAIL VIEW OF B

SR NO	TUBE SPECIFICATION	
1	72X72X3.2mm MS TUBE	OUTER FRAME
2	32X32X2mm MS TUBE	INNER PATTERN
3	GAP BETWEEN TUBES	150mm
4	MS SHEET	MS SHEET
5	72X72X3.2mm MS TUBE	FOR POST

SR.NO	RAL CODE	RAL COLOR	REV NO	REV DATE	DRAWN	REMARK
04	RAL 7035	LIGHT GREY				
03	RAL 5002	ULTRAMARINE BLUE				
02	RAL 9002	GREY WHITE				
01	RAL 1004	GOLDEN YELLOW	R01	10.10.2019	P.V.A	1. CLEAR WIDTH CHANGE

TOLERANCE:- ± 10mm

CLEAR WIDTH (CW)	CLEAR HEIGHT (CH)	QUANTITY
10500mm	1800mm	1 NOS

DIMENSION :

CLEAR WIDTH	CLEAR HEIGHT	QUANTITY
10500mm	1800mm	1 NOS

MATERIAL: MS

THICKNESS :

NOTE-
1. ALL REQUIRED CIVIL WORK WILL BE IN CLIENTS SCOPE.
2.ONE COAT OF RED OXIDE & TWO COAT OF APPROVED RAL SHADE WILL BW GIVEN TO THE GATE
3.IN NECESSARY GATE LEAF WILL BE IN TWO PART FOR TRANSPORTATION AND ILL BE WELDED TOGETHER ON SITE

NIHVA TECHNOLOGIES PVT. LTD.
NIHVA TECHNOLOGIES PVT. LTD. PUNE
Website:- www.nihva.com
Email:- info@nihva.com
TEL :020 66304033

TITLE:

AUTOMATIC SINGLE LEAF SLIDING GATE

CLIENT'S APPROVAL :

CLIENT - INOX AIR PRODUCTS.

PROJECT -

SITE LOCATION -MODINAGAR,UTTAR PRADESH

DWG. NO. : NIHVA/18-19/0175/R01	REV. : R01
SCALE: NTS	WT:	SHEET:1 OF 1

DRAWN	SURAJ		DATE: 13-11-18
CHECK	PRADEEP		DATE: 13-11-18
APPROVED	R.D		DATE: 13-11-18

IF ANY QUERIES CONTACT:- design@nihva.com

NOTE: ALL DIMENSIONS ARE IN mm

THIS DRAWING & DESIGN IS THE PROPERTY OF NIHVA TECHNOLOGIES. NOT TO BE SOLD OR COPIED TO ANY OTHER CONCERN.