



SIDE VIEW


Section A-A

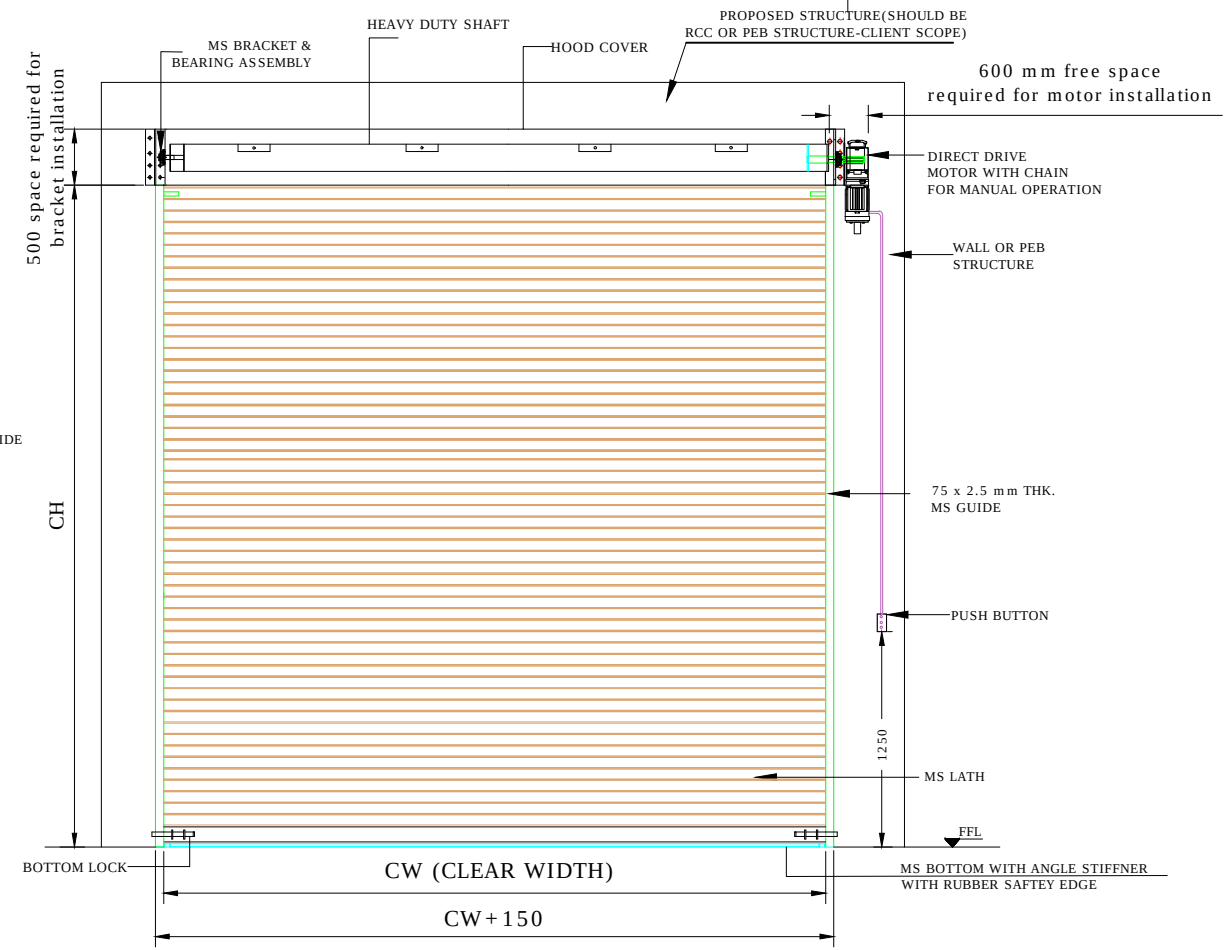


ELEVATION

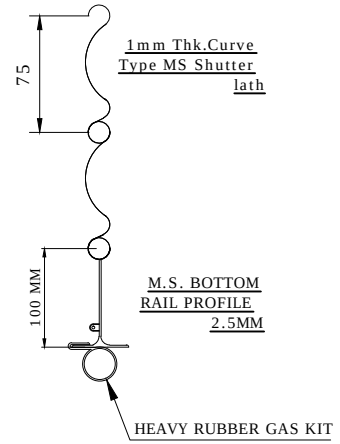

M.S. BOTTOM RAIL PROFILE 2.5MM

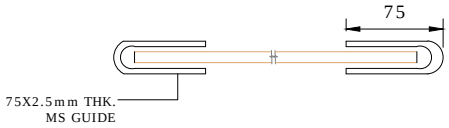

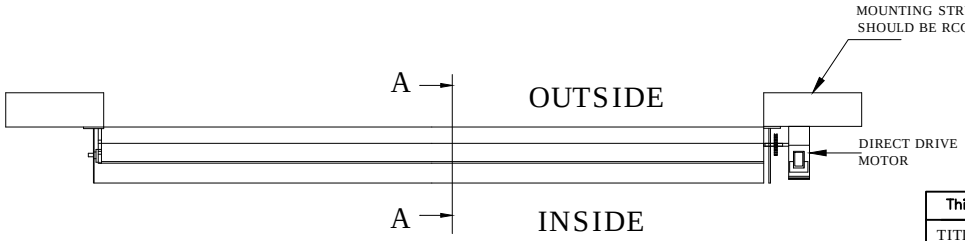

TOLERANCE - ±10mm

CLEAR WIDTH (CW)	CLEAR HEIGHT (CH)	QUANTITY
4000	4000	02 NO

This drawing & design is the property of NIHVA TECHNOLOGIES. Not to be sold or copied to any other concern.

TITLE	MOTORIZED ROLLING SHUTTER			NIHVA TECHNOLOGIES PVT. LTD. PUNE Tel : 020 66304033 Email:- info@nihva.com Website:- www.nihva.com	
	NAME	SIGN	DATE		
DRAWN	SURAJ		29.09.2018	CLIENT -	
CHECK	P.A		29.09.2018	PROJECT -	
APPRD.	R.D		29.09.2018	SITE LOCATION -	
If any queries contact : design@nihva.com				DWG. NO. : NIHVA/18-19/VDR/131	REV- 0
ALL DIMENSION ARE IN mm				SCALE: NTS	WT: SHEET: 01 OF 01

NOTE-
1.ONE COAT OF RED OXIDE WILL BE GIVEN TO SHUTTER. PAINT OF APPROVED RAL SHADE WILL BE GIVEN TO THE SHUTTER.