
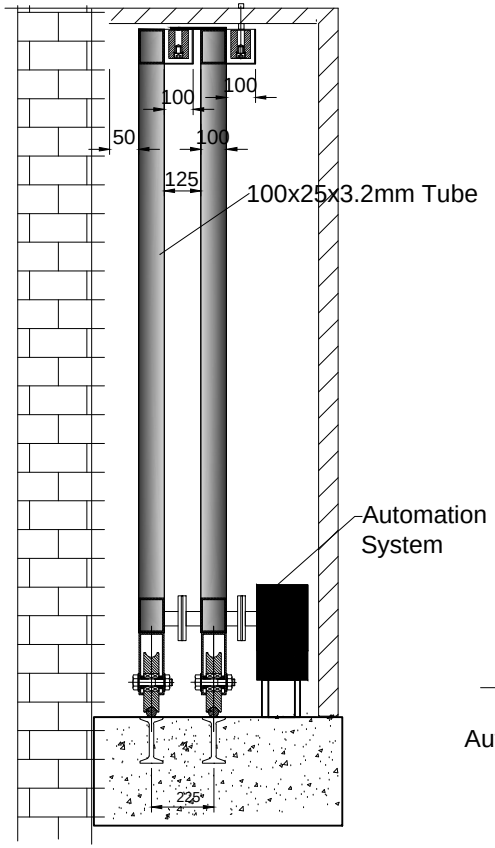



OPENING DIRECTION


6250 clear opening

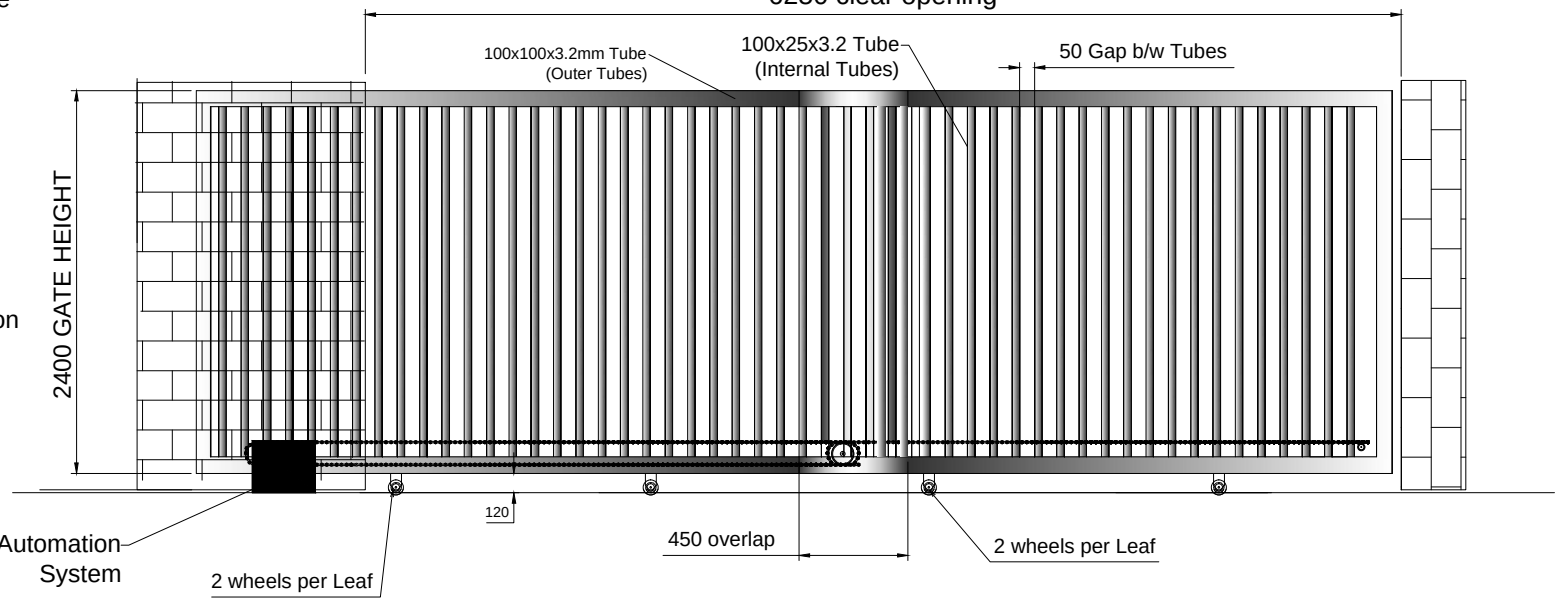

3725

OPENING DIRECTION

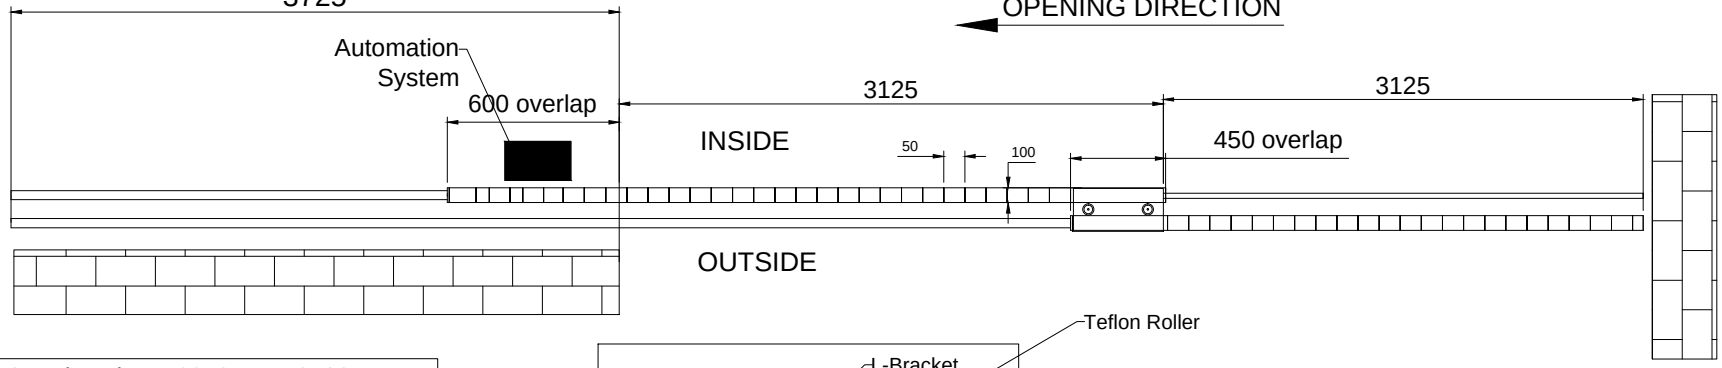

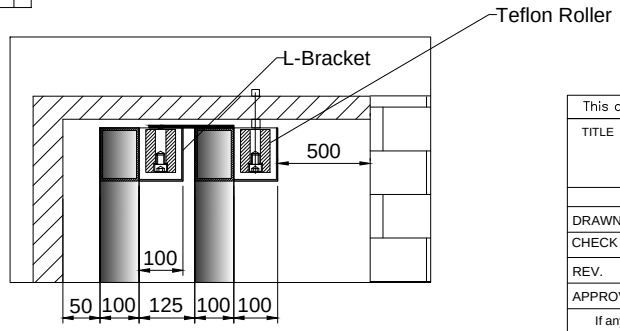

Clear Opening size - 6250mm x 2400mm
Total No. of Leaf - 2 Leaf
Factory paint finish - Red oxide primer coat
NOTE :- *ALL REQ. CIVIL WORK WILL BE IN CLIENT SCOPE.

This drawing & designing is the property of NIHVA TECHNOLOGIES. Not be sold or copy to any other concern.

TITLE	TELESCOPIC SLIDING GATE		NIHVA TECHNOLOGY PVT. LTD. PUNE
	SIGN	DATE	NIHVA TECHNOLOGIES PVT. LTD.
DRAWN	OMKAR	14/01/16	CLIENT - LUPIN
CHECK	ANIL	14/01/16	PROJECT -LUPIN
REV.	01		SITE -
APPROVAL			DWG. NO. : NIHVA/15-16/178
If any queries contact : projects@nihva.com			SCALE: 01 / WT: / SHEET: 01 OF 01
ALL DIMENSION ARE IN mm			

Tel : 020 66304033
Email:- info@nihva.com
Website:- www.nihva.com