

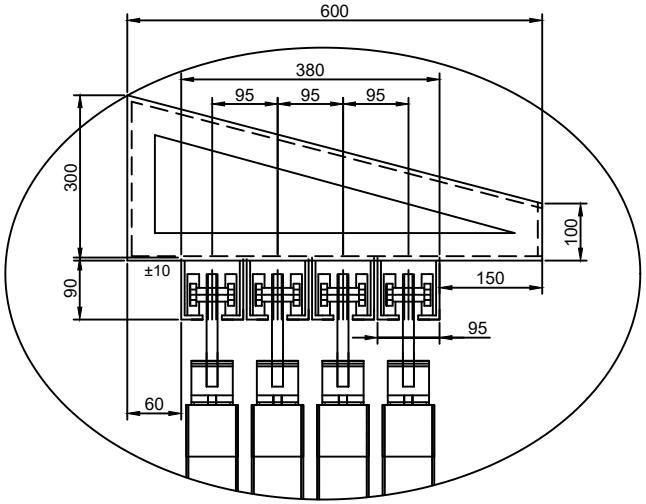



TITLE:-4LEAF BOTH SIDE SLIDING
CRM DOOR-1/Gate 9

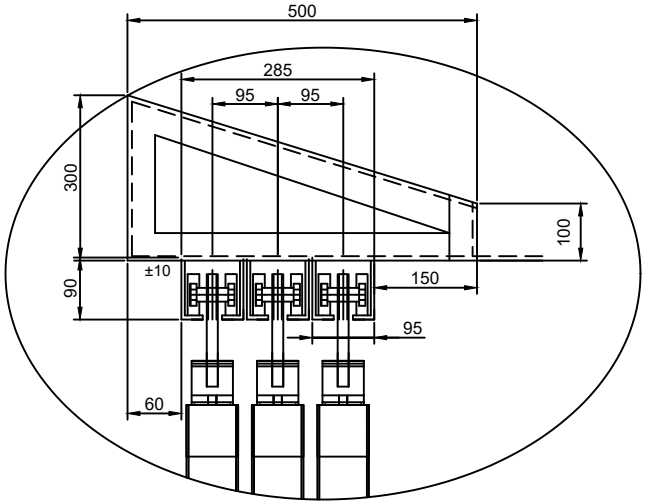


TITLE:- 3 LEAF RIGHT SIDE SLIDING

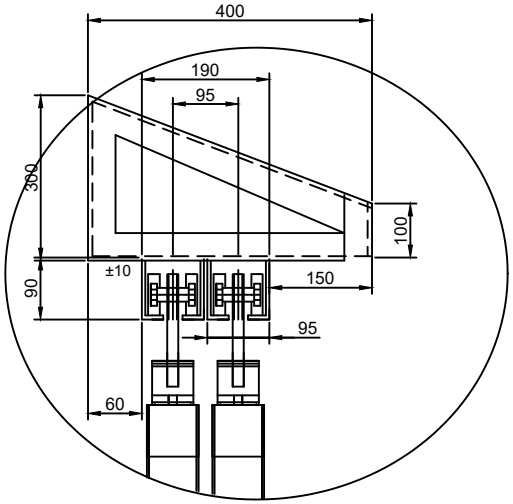


TITLE:- 4 LEAF BOTH SIDE SLIDING
CRM DOOR - 10/Gate 24

Note:-
1.All dimension are in MM
2.Manufacturing,civil and installation tolerance will be ±10mm
3.Top and Bottom track should be in parallal within ±3mm
4.Nihva Supervisor on site for Monitoring/Checking of civil work

| Rev No. | Revision | Date | Revised By |
|---|---|---|---|
| 00 | Released drawing | 29/04/2022 | MAHESH |
| | | | |

This drawing & design is the property of NIHVA TECHNOLOGIES. Not to be sold or copied to any other concern.

TITLE:-CANNOPY FOR 5 DOORS

NIHVA TECHNOLOGIES PVT. LTD.

NIHVA TECHNOLOGIES PVT. LTD. PUNE
Tel : 020 66304033
Email:- info@nihva.com
Website:- www.nihva.com

| | NAME | DATE | SIGN |
|---|---|---|---|
| DRAWN | M.SUTAR | 05/05/2022 | |
| CHECK | M.SUTAR | 05/05/2022 | |
| APPRD. | V.TARAK | 05/05/2022 | |

If any queries contact : design@nihva.com

ALL DIMENSION ARE IN mm

CLIENT - LESTECH
LOCATION - POSCO MANGAON
PRODUCT - SLIDING DOOR
DWG NO:-NIHVA/22-23/CLT/0017 REV- 1
SCALE: NTS SCALE:-- 1:1 SHEET: 01 OF 01