


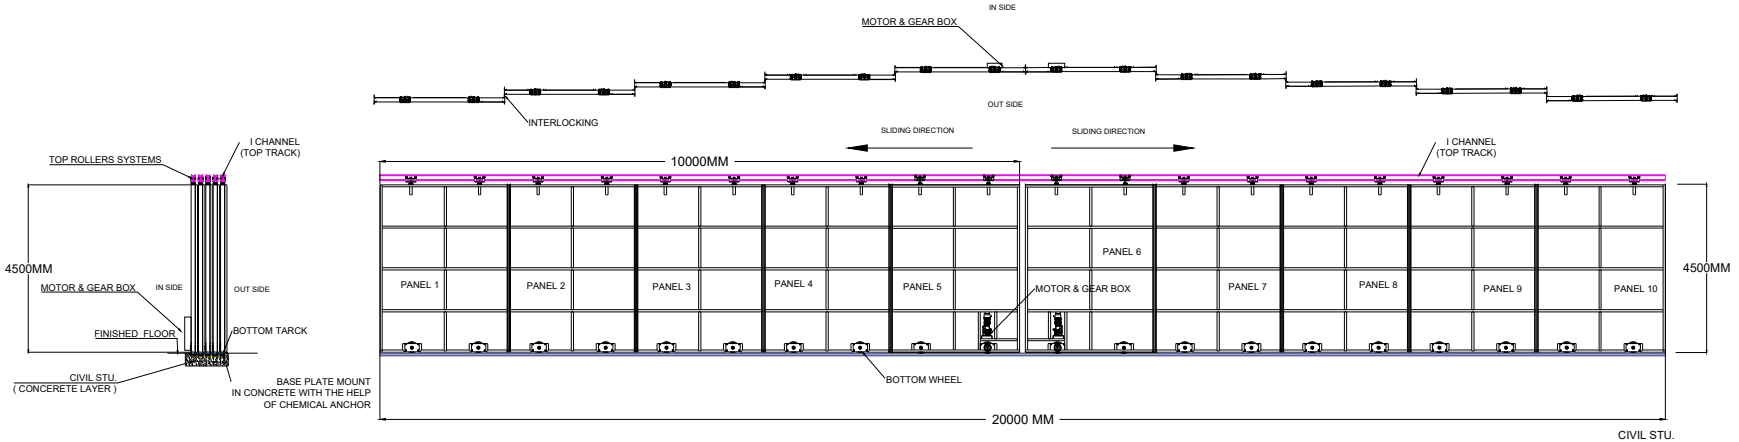


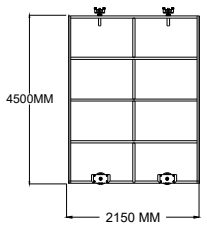

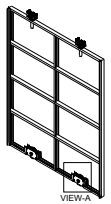

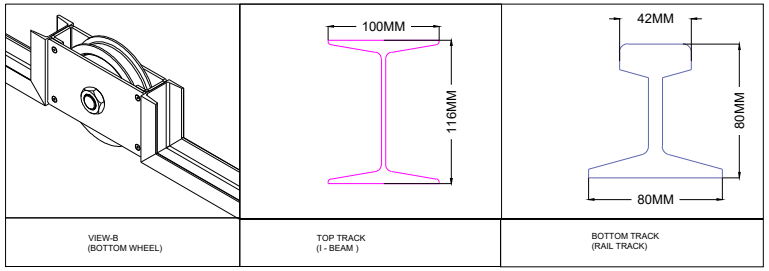

TECHANICAL SPECIFICATION -

DOOR SIZE - 20000MM X 4500MM
NUMBER OF PANEL - 10
PANEL SIZE - 2150MM X 4500MM
NUMBER OF MOTORS - 2 Nos.

EACH DOOR LEAF IS TO BE SUPPORTED AT THE BOTTOM ON 2 Nos.
EACH DOOR LEAF IS TO BE SUPPORTED AT THE TOP ON 2 Nos.
MOTOR MOUNTING ON PANEL NO. 5 & 6.

This drawing & designing is the property of NIHVA TECHNOLOGIES. Not be sold or copy to any other concern.

TITLE	BI-PARTING HANGER DOOR	NIHVA	NIHVA TECHNOLOGY PVT. LTD. PUNE
	SIGN.	DATE	Email:- Sales@nihva.com Website:- www.nihva.com
DRAWN	J.P	06/11/25	CLIENT - ARCEDGES BUILDING INDIA LLP
CHECK	B.S	07/11/25	PROJECT -BI-PARTING HANGER DOOR
REV.	00		SITE - HYDERABAD
APPROVAL	V.T	07/11/25	DWG. NO. - NIHVA/15-16/178
If any queries contact : projects@nihva.com			SCALE: 01 / WT: / SHEET: 01 OF 01
ALL DIMENSION ARE IN mm			