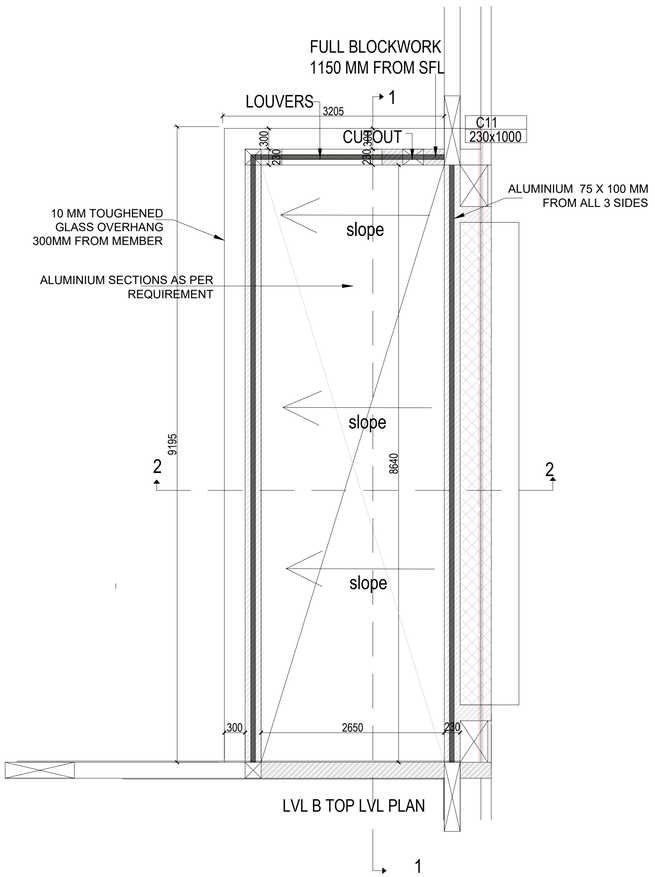
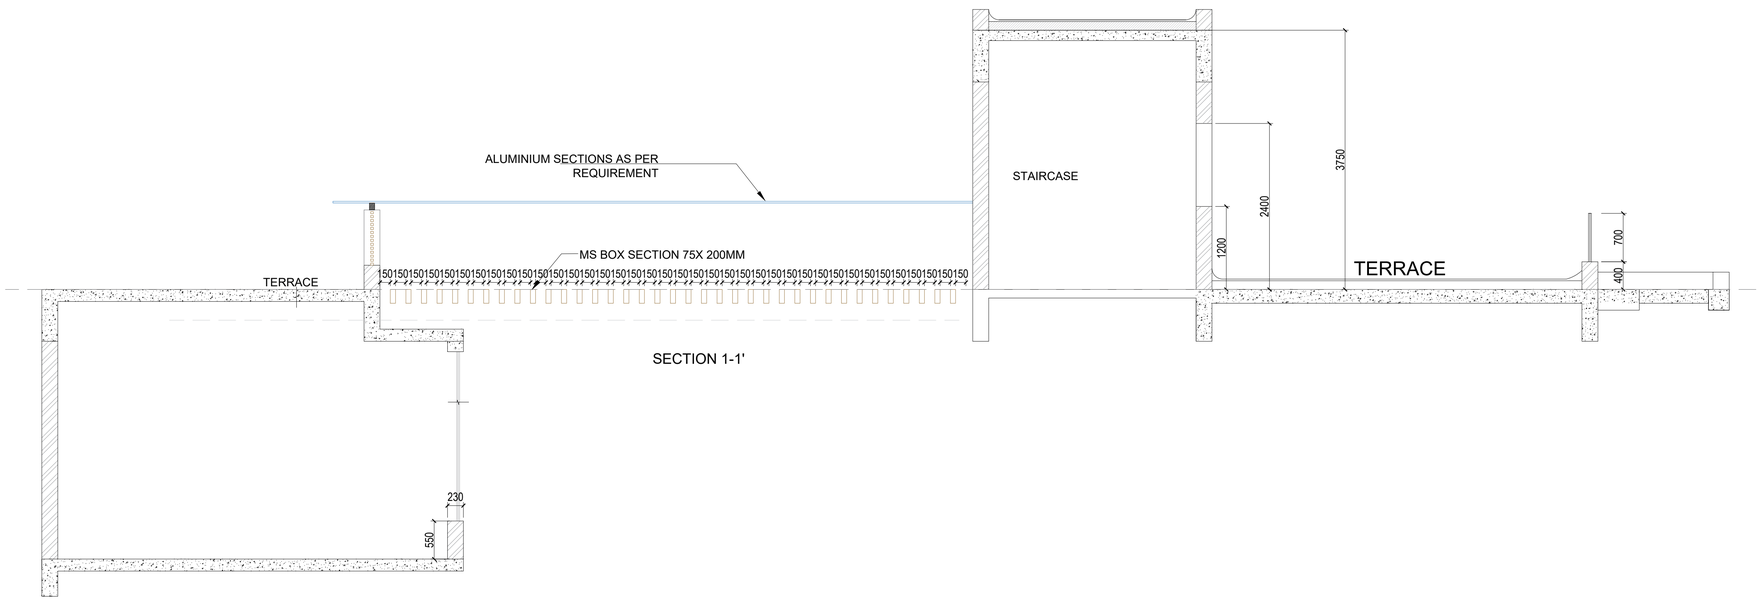
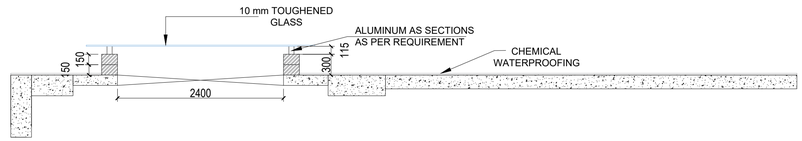
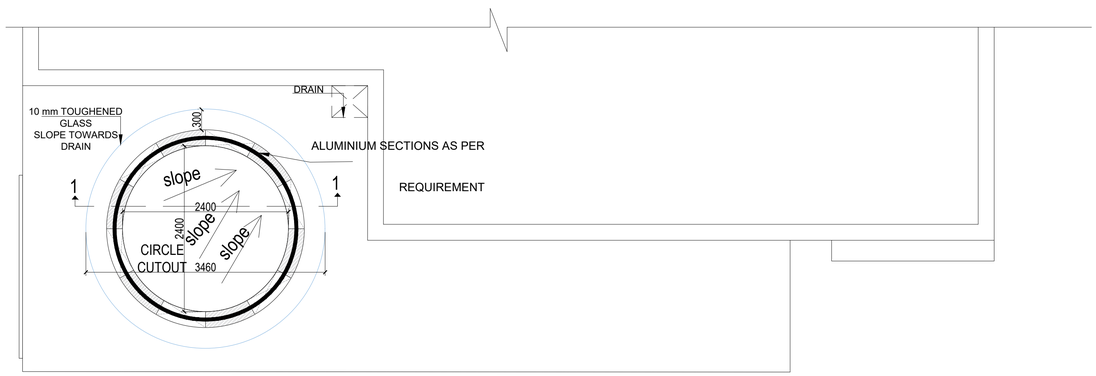

FULL BLOCKWORK
1150 MM FROM SFL
LOUVERS
3205
1
C11
230x1000
CUTOUT
300
200
200
10 MM TOUGHENED
GLASS OVERHANG
300MM FROM MEMBER
ALUMINIUM 75 X 100 MM
FROM ALL 3 SIDES
slope
ALUMINIUM SECTIONS AS PER
REQUIREMENT
slope
slope
9195
8640
2
2
300
2650
230
LVL B TOP LVL PLAN
1


ALUMINIUM SECTIONS AS PER
REQUIREMENT
STAIRCASE
3750
2400
1200
700
400
TERRACE
MS BOX SECTION 75X 200MM
TERRACE
150150150150150150150150150150150150150150150150150150150150150150150150150150150150150150150150150150150
230
550
SECTION 1-1'


10 mm TOUGHENED
GLASS
ALUMINUM AS SECTIONS
AS PER REQUIREMENT
CHEMICAL
WATERPROOFING
150
150
115
300
2400


DRAIN
10 mm TOUGHENED
GLASS
SLOPE TOWARDS
DRAIN
300
ALUMINIUM SECTIONS AS PER
REQUIREMENT
1
1
slope
2400
2400
slope
slope
CIRCLE
CUTOUT
3460