


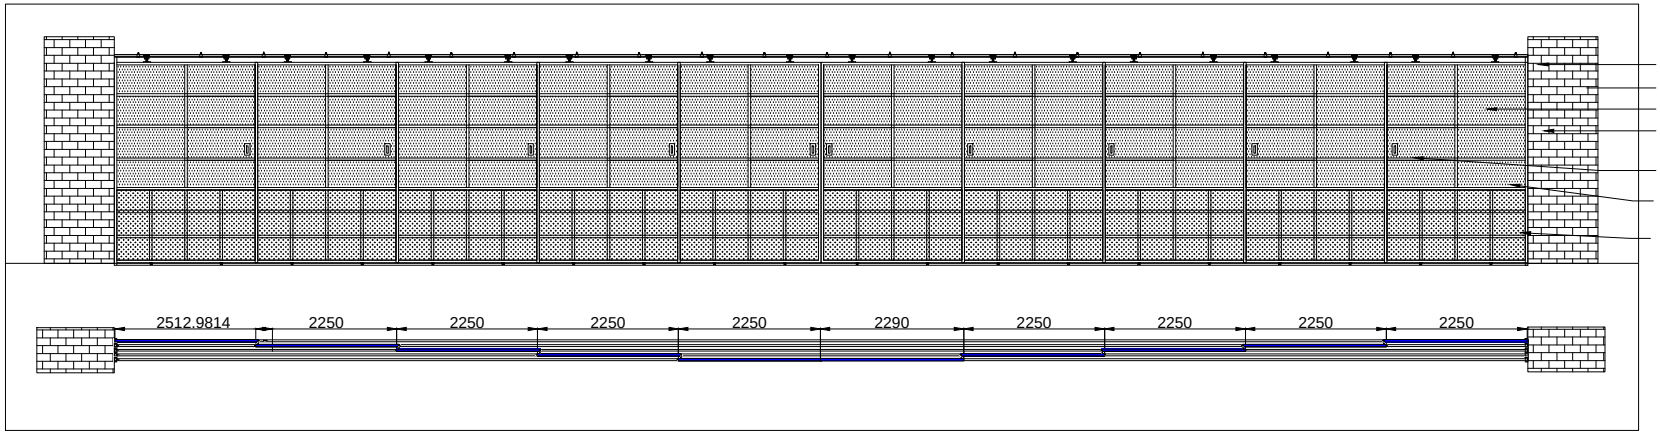


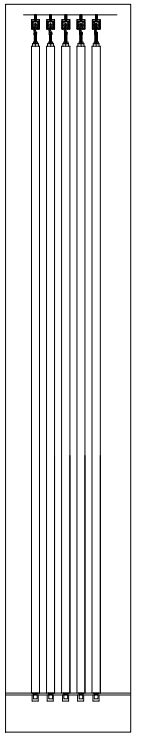



SIDE VIEW


NOTATION	DW	DH	PANELS	RAILS	QUANTITY
SD1	16400	3200	10	5	1
SD2	22500	3200	10	5	1
SD3	13300	3200	10	5	1
SD4	10000	3200	8	4	1
SD5	12000	3200	10	5	1
SD6	5950	3200	4	4	1
SD7	2500	2400	2	2	1
SD8	1800	2400	2	2	2
SD9	4795	3200	4	4	1
SD	5940	3200	4	4	1
SD1	19200	3200	10	5	5
SD2	12400	3200	10	5	3
SD3	19080	3200	10	5	6
SD4	17600	3200	10	5	1
SD5	17700	3200	10	5	5
SD6	9200	3200	8	4	1
SD7	13900	3200	10	5	2
SD8	10100	3200	8	4	1
SD9	15300	3200	10	5	1
SD10	14300	3200	10	5	1
SD11	4850	3200	4	4	1
SD12	2500	2400	2	2	1
SD13	4330	2400	2	2	1
SD14	4000	3200	2	2	1
SD15	2000	3200	2	2	1
SD16	3000	3000	2	2	1
SD17	13780	3200	10	5	1
SD18	9000	3200	8	4	1
SD19	19300	3200	10	5	1

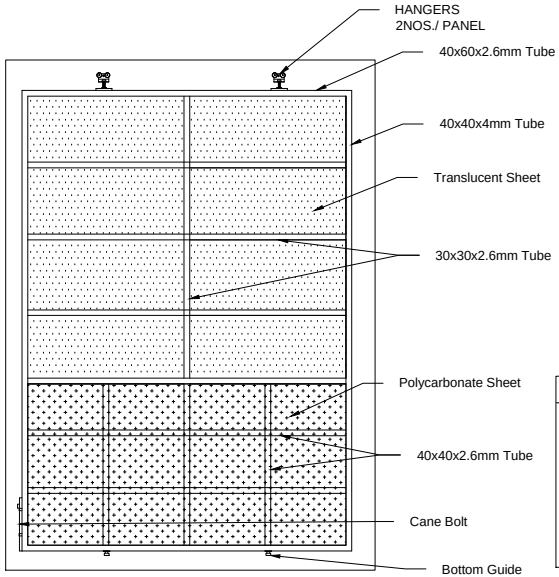

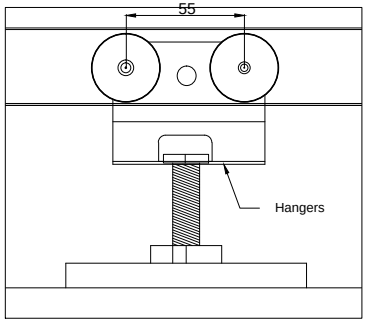

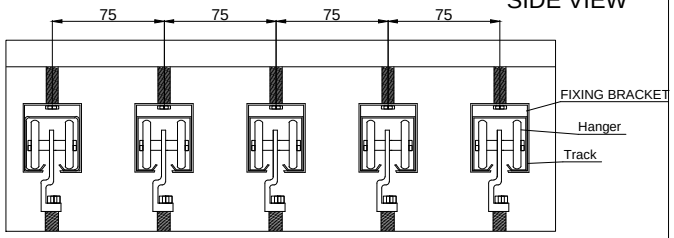

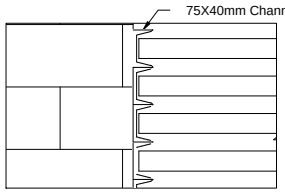

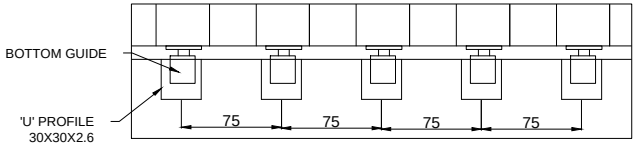

This drawing & designing is the property of NIHVA TECHNOLOGIES. Not be sold or copy to any other concern.

TITLE

SLIDING DOOR

CLIENT APPROVAL

ALL DIMENSION ARE IN mm

	SIGN	DATE
DRAWN	ABHIJIT	03/10/15
CHECK	ANIL	03/10/15
ENG		
APPRD.		
MFG		
Ref. No.		

NIHVA
NIHVA TECHNOLOGIES PVT. LTD.
NIHVA TECHNOLOGY PVT. LTD. PUNE
Tel : 020 66304033
Email:- info@nihva.com
Website:- www.nihva.com

CLIENT - Shapoorji-Palonji

PROJECT-Maruti-Suzuki

SITE -

DWG. NO. - NIHVA/15-16/101

SCALE: 01 | WT: | SHEET: 01

If any queries contact : projects@nihva.com