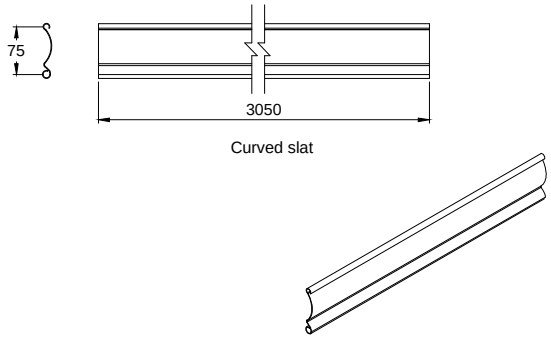

Curved slat

Slat profile- curved type.
Material- MS
Thickness - 1mm
Length of slats - 3050mm
Total no of slat - 50

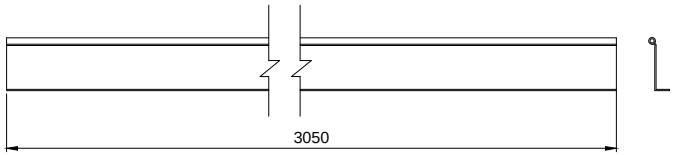

Material- MS
Thickness - 2.5mm
Length of bottom profile - 3050mm
Quantity- 1 Nos.

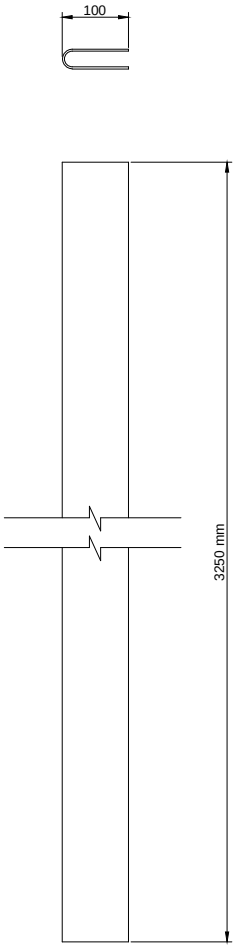

Material- MS
Thickness - 3mm
Length of guide - 3250mm
Quantity- 2 Nos.

This drawing & design is the property of NIHVA TECHNOLOGIES. Not to be sold or copied to any other concern.

TITLE

SLAT GUIDE & BOTTOM

NIHVA TECHNOLOGIES PVT. LTD.
NIHVA TECHNOLOGIES PVT. LTD. PUNE
Tel : 020 66304033
Email:- info@nihva.com
Website:- www.nihva.com

	SIGN	DATE
DRAWN	OMKAR	05/04/17
CHECK	SAGAR P.	05/04/17
REV.		
APPROVAL	R.K.	05/04/17

If any queries contact : projects@nihva.com

ALL DIMENSION ARE IN mm

CLIENT -

PROJECT -

SITE -

DWG. NO. : NIHVA/17-18/MFG/001

SCALE: NTS | WT: | SHEET: 01 OF 01