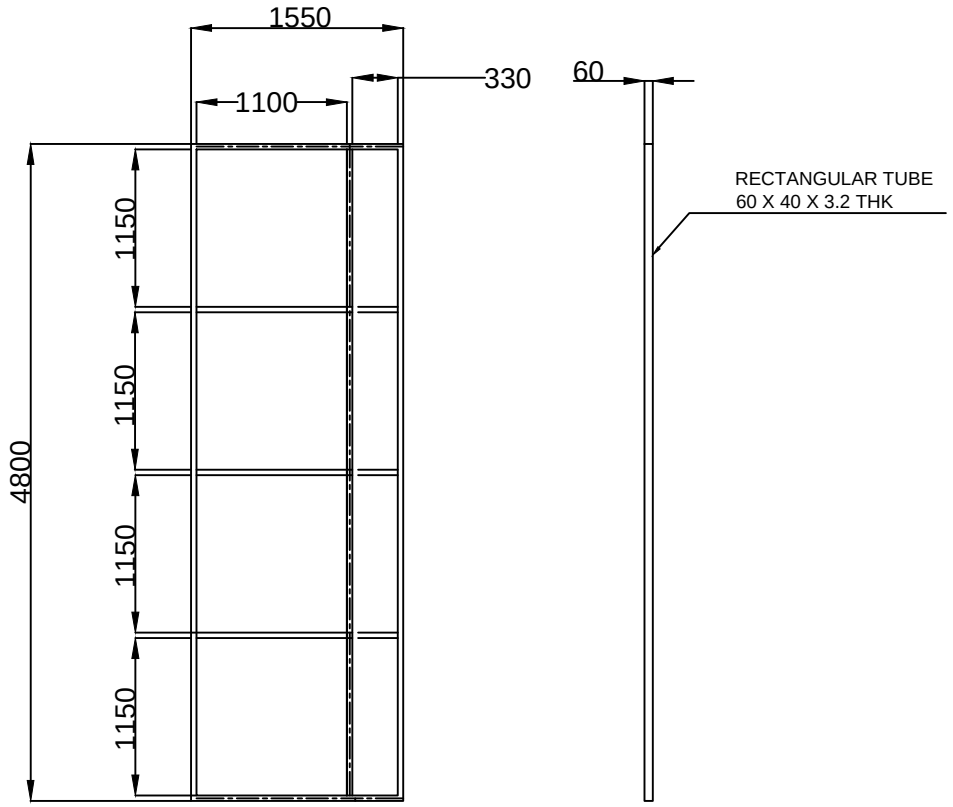

QTY=02 NOS

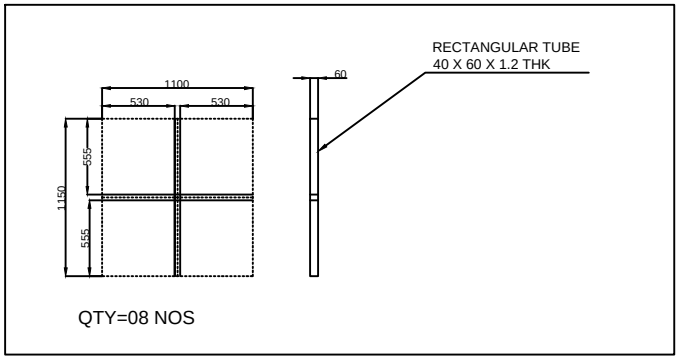

QTY=08 NOS

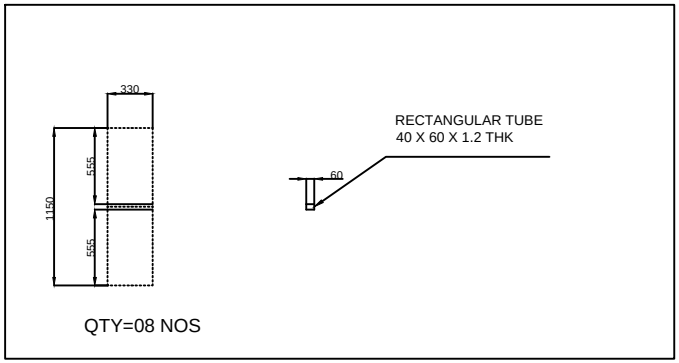

QTY=08 NOS

This drawing & design is the property of NIHVA TECHNOLOGIES. Not to be sold or copied to any other concern.

TITLE:- 4 LEAF BOTH SIDE CRM DOOR 013

NIHVA TECHNOLOGIES PVT. LTD. PUNE
Tel : 020 66304033
Email:- info@nihva.com
Website:- www.nihva.com

	NAME	DATE	SIGN
DRAWN	KISHAN	14/05/2022	
CHECK	M.SUTAR	14/05/2022	
APPRD.			

If any queries contact : design@nihva.com

ALL DIMENSION ARE IN mm

CLIENT - LESTECH

LOCATION - POSCO MANGAON

PRODUCT - SLIDING DOOR

DWG NO:-NIHVA/22-23/MFG/0021 | REV- 0

SCALE: NTS | SCALE:-- 1:1 | SHEET: 01 OF 02

	Date	Revised By